АЛА-ТОО РЕЗОРТ · ЖЫРГАЛАН · УЧАСТОК 27


Апарт-резиденция «Family Active Residence»

Эскизный проект · раздел АР · 17.10.2026

Площадь застройки (по облицовке на уровне земли + рёбра-опоры)	**480,3**
Площадь здания (сумма этажей в пределах внутренних граней наружных стен)	**2 574,7**
Количество апартаментов	**34**
Общая площадь апартаментов (без летних помещений)	**1 477,5**
Строительный объём, всего	**10 925**
Высота до конька от уровня земли	**24,50**

Все листы — сечения и проекции IFC-модели Ala-Too_lot27_residence.ifc. Альбом А3: листы А2 в масштабе 1:100 уменьшены в √2 раза (≈ 1:141). Для печати в масштабе — альбом А2.



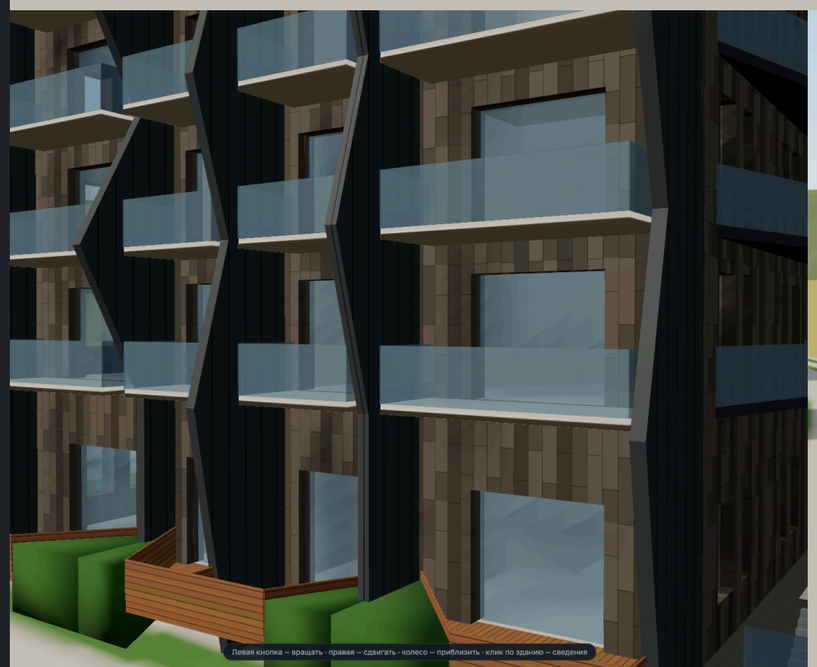



Состав альбома

Лист	Наименование
АР-1	Общие данные: ТЭП, ведомости
АР-2	План полуцоколя на отм. −3,200
АР-3	План 1 этажа на отм. ±0,000
АР-4	План 2–4 этажей (типовой) на отм. +4,500; +7,800; +11,100
АР-5	План мансардного (5) этажа на отм. +14,400
АР-6	План кровли
АР-7	Фасад 1–5 (южный)
АР-8	Фасад 5–1 (северный)
АР-9	Фасад А–Д (восточный)
АР-10	Фасад Д–А (западный)
АР-11	Разрез 1-1
АР-12	Разрез 2-2

Онлайн: 3D-модель с переключением фасадов, поэтажные планы, ревизия планировок, ТЭП и чек-лист норм — https://ayupov0.github.io/ala-too/

Ведомость листов комплекта АР (стадия ЭП)

Лист	Наименование
АР-1	Общие данные: ТЭП, ведомости
АР-2	План полуцоколя на отм. −3,200
АР-3	План 1 этажа на отм. ±0,000
АР-4	План 2–4 этажей (типовой) на отм. +4,500; +7,800; +11,100
АР-5	План мансардного (5) этажа на отм. +14,400
АР-6	План кровли
АР-7	Фасад 1–5 (южный)
АР-8	Фасад 5–1 (северный)
АР-9	Фасад А–Д (восточный)
АР-10	Фасад Д–А (западный)
АР-11	Разрез 1-1
АР-12	Разрез 2-2

Общие указания

1. Эскизный проект выполнен по IFC-модели Ala-Too_lot27_residence.ifc; все листы — её сечения и проекции.
2. Отметка ±0,000 = чистый пол 1-го этажа = 2249,37 м (Балтийская, по DEM); земля −1,200.
3. Конструкции: монолитный ж/б каркас-стены, ядро жёсткости; сейсмичность и фундаменты — по изысканиям.
4. Наружные стены 350 мм + вентфасад 220 мм (минвата 150, керамогранит / гранит цоколя).
5. Вентфасад и рёбра выходят за границу участка (пятно = контур несущих стен). Нужно согласование, как для балконов; иначе облицовка внутрь — минус ~0,3 м² на квартиру.
6. Открытые вопросы: одна лестница; второй выход из полуцоколя; функциональный класс — решения местного проектировщика и пожарного эксперта до стадии П.
7. Площади — по внутренним граням стен; мансарда учтена полностью (потолок ≥ 1,8 м).

Технико-экономические показатели

Показатель	Ед.	Значение
Площадь участка (по генплану, пятно)	м²	458,92
Площадь застройки (по облицовке на уровне земли + рёбра-опоры)	м²	480,3
в т.ч. выход вентфасада за границу участка (0,22 м по периметру)	м²	19,2
крыльцо, наружные лестницы (дополнительно)	м²	10,0
Этажность (5-й — мансардный) / количество этажей с полуцоколем	эт.	5 / 6
Высота до конька от уровня земли	м	24,50
Площадь здания (сумма этажей в пределах внутренних граней наружных стен)	м²	2 574,7
в т.ч. надземная часть	м²	2 145,6
в т.ч. полуцоколь	м²	429,1
Количество апартаментов	шт.	34
Общая площадь апартаментов (без летних помещений)	м²	1 477,5
Общая площадь апартаментов с летними (лоджия 0,5; балкон, терраса 0,3)	м²	1 593,6
Жилая площадь апартаментов (гостиные, спальни, детские)	м²	977,1
Площадь общих и служебных помещений (лобби, коридоры, ядро, служебные, полуцоколь)	м²	904,6
Мест размещения: основных / дополнительных	мест	92 / 52
Строительный объём, всего	м³	10 925
в т.ч. выше отметки ±0,000	м³	9 395
в т.ч. ниже отметки ±0,000	м³	1 530
Коэффициент К1 = жилая / общая площадь апартаментов	–	0,66
Коэффициент планировочный: площадь апартаментов / надземная площадь здания	–	0,69
Площадь кровли (фальц, по скатам)	м²	745,8
Площадь наружных стен (керамогранит + гранит цоколя, за вычетом проёмов)	м²	1 564,1

Квартирография

Тип	Шт.	Площадь, м²	Средняя, м²	Места
Студия	8	251,2	31,4	16 + 0
1 спальня	14	561,9	40,1	28 + 28
Семейная (2 спальни)	10	459,7	46,0	40 + 20
Пентхаус	2	204,7	102,3	8 + 4
Итого	34	1 477,5	–	92 + 52

Ведомость отделки фасада (вариант Б3)

Материал	Площадь, м² ≈
Керамогранит 300×1200, тёмный тёплый базальт, 3 тона, на вентфасаде	1 284,7
Гранит термообработанный, цоколь	279,4
Фальц сталь 0,6 мм PVDF графит — кровля	745,8
Фальц сталь 0,6 мм PVDF графит — южные рёбра (обе стороны)	523,9
Кассеты алюминиевые графит — рёбра севера, изломы, козырёк	588,7
Окна, балконные блоки, витражи, мансардные окна (по ведомости)	326,8
Безрамное остекление лоджий, панорамный фронтон	435,8
Ограждения балконов — стекло триплекс	317,3
Лиственница — террасы 1-го этажа и кафе (настил)	114,0


Ведомость заполнения оконных проёмов

Марка	Окна и балконные блоки	Шир.	Выс.	Шт.	м²
ОК-1	Балконный блок / дверь на лоджию, алюминий, тройной стеклопакет	2,80	2,70	2	15,1
ОК-2	Балконный блок / дверь на лоджию, алюминий, тройной стеклопакет	2,60	2,70	2	14,0
ОК-3	Балконный блок / дверь на лоджию, алюминий, тройной стеклопакет	2,80	2,50	6	42,0
ОК-4	Балконный блок / дверь на лоджию, алюминий, тройной стеклопакет	2,60	2,50	6	39,0
ОК-5	Балконный блок / дверь на лоджию, алюминий, тройной стеклопакет	1,30	2,50	6	19,5
ОК-6	Балконный блок / дверь на лоджию, алюминий, тройной стеклопакет	1,00	2,70	1	2,7
ОК-7	Балконный блок / дверь на лоджию, алюминий, тройной стеклопакет	1,00	2,50	6	15,0
ОК-8	Балконный блок / дверь на лоджию, алюминий, тройной стеклопакет	0,90	2,50	6	13,5
ОК-9	Балконный блок / дверь на лоджию, алюминий, тройной стеклопакет	0,80	2,50	6	12,0
ОК-10	Балконный блок / дверь на лоджию, алюминий, тройной стеклопакет	0,80	2,30	2	3,7
ОК-11	Витраж лобби, алюминий с терморазрывом	2,00	3,30	2	13,2
ОК-12	Витраж лобби, алюминий с терморазрывом	1,60	3,30	2	10,6
ОК-13	Окно мансардное в скате, тройное остекление	0,78	1,62	7	8,8
ОК-14	Окно мансардное в скате, тройное остекление	0,78	1,34	8	8,4
ОК-15	Окно полуцоколя в приямке	1,60	0,80	2	2,6
ОК-16	Окно, алюминий с терморазрывом, графит, тройной стеклопакет	1,40	1,60	6	13,4
ОК-17	Окно, алюминий с терморазрывом, графит, тройной стеклопакет	1,20	1,85	2	4,4
ОК-18	Окно, алюминий с терморазрывом, графит, тройной стеклопакет	0,94	2,20	1	2,1
ОК-19	Окно, алюминий с терморазрывом, графит, тройной стеклопакет	1,40	1,40	1	2,0
ОК-20	Окно, алюминий с терморазрывом, графит, тройной стеклопакет	1,30	1,50	2	3,9
ОК-21	Окно, алюминий с терморазрывом, графит, тройной стеклопакет	1,20	1,60	12	23,0
ОК-22	Окно, алюминий с терморазрывом, графит, тройной стеклопакет	1,00	1,85	4	7,4
ОК-23	Окно, алюминий с терморазрывом, графит, тройной стеклопакет	1,40	1,20	3	5,0
ОК-24	Окно, алюминий с терморазрывом, графит, тройной стеклопакет	1,00	1,60	18	28,8
ОК-25	Окно, алюминий с терморазрывом, графит, тройной стеклопакет	1,30	1,20	1	1,6
ОК-26	Окно, алюминий с терморазрывом, графит, тройной стеклопакет	0,80	1,85	2	3,0
ОК-27	Окно, алюминий с терморазрывом, графит, тройной стеклопакет	1,20	1,20	1	1,4
ОК-28	Окно, алюминий с терморазрывом, графит, тройной стеклопакет	0,75	1,85	2	2,8
ОК-29	Окно, алюминий с терморазрывом, графит, тройной стеклопакет	0,75	1,60	6	7,2
ОК-30	Окно, алюминий с терморазрывом, графит, тройной стеклопакет	0,80	0,92	1	0,7

Ведомость заполнения дверных проёмов

Марка	Двери	Шир.	Выс.	Шт.	
Д-1	Дверь в лестничную клетку, EI 30, с доводчиком	1,00	2,10	6	
Д-2	Дверь входная в квартиру, EI 30, утеплённая	1,00	2,10	1	
Д-3	Дверь входная в квартиру, EI 30, утеплённая	0,90	2,10	33	
Д-4	Дверь лифта (поставка с лифтом)	0,90	2,10	6	
Д-5	Дверь межкомнатная / служебная, ламинированная	1,20	2,10	2	
Д-6	Дверь межкомнатная / служебная, ламинированная	1,00	2,10	1	
Д-7	Дверь межкомнатная / служебная, ламинированная	0,90	2,10	8	
Д-8	Дверь межкомнатная / служебная, ламинированная	0,80	2,10	17	
Д-9	Дверь межкомнатная / служебная, ламинированная	0,75	2,10	27	
Д-10	Дверь наружная, алюминий с терморазрывом, остеклённая	1,80	2,70	1	
Д-11	Дверь наружная, алюминий с терморазрывом, остеклённая	1,60	2,70	1	
Д-12	Дверь наружная, алюминий с терморазрывом, остеклённая	1,20	2,10	1	
Д-13	Дверь санузла, ламинированная, с вентрешёткой	0,70	2,10	33	
Д-14	Дверь санузла, ламинированная, с вентрешёткой	0,65	2,10	3	

					ЖР-27 · Ала-Тоо Резорт, Жыргалан · АР	
					Апарт-резиденция «Family Active Residence», участок 27	
					Жилое здание 5 эт. (мансарда) с полуцоколем, 34 апартамента	
Изм.	Кол.	Лист	№док	Подп.	Общие данные	Стадия: ЭП; Лист: 1; Листов: 12
Разраб.		ИИ-ассист.		10.26		
Рук. пр.		Аюпов Р.		10.26		
ГАП				10.26	АР-1	М 1:100
Н. контр.				10.26		

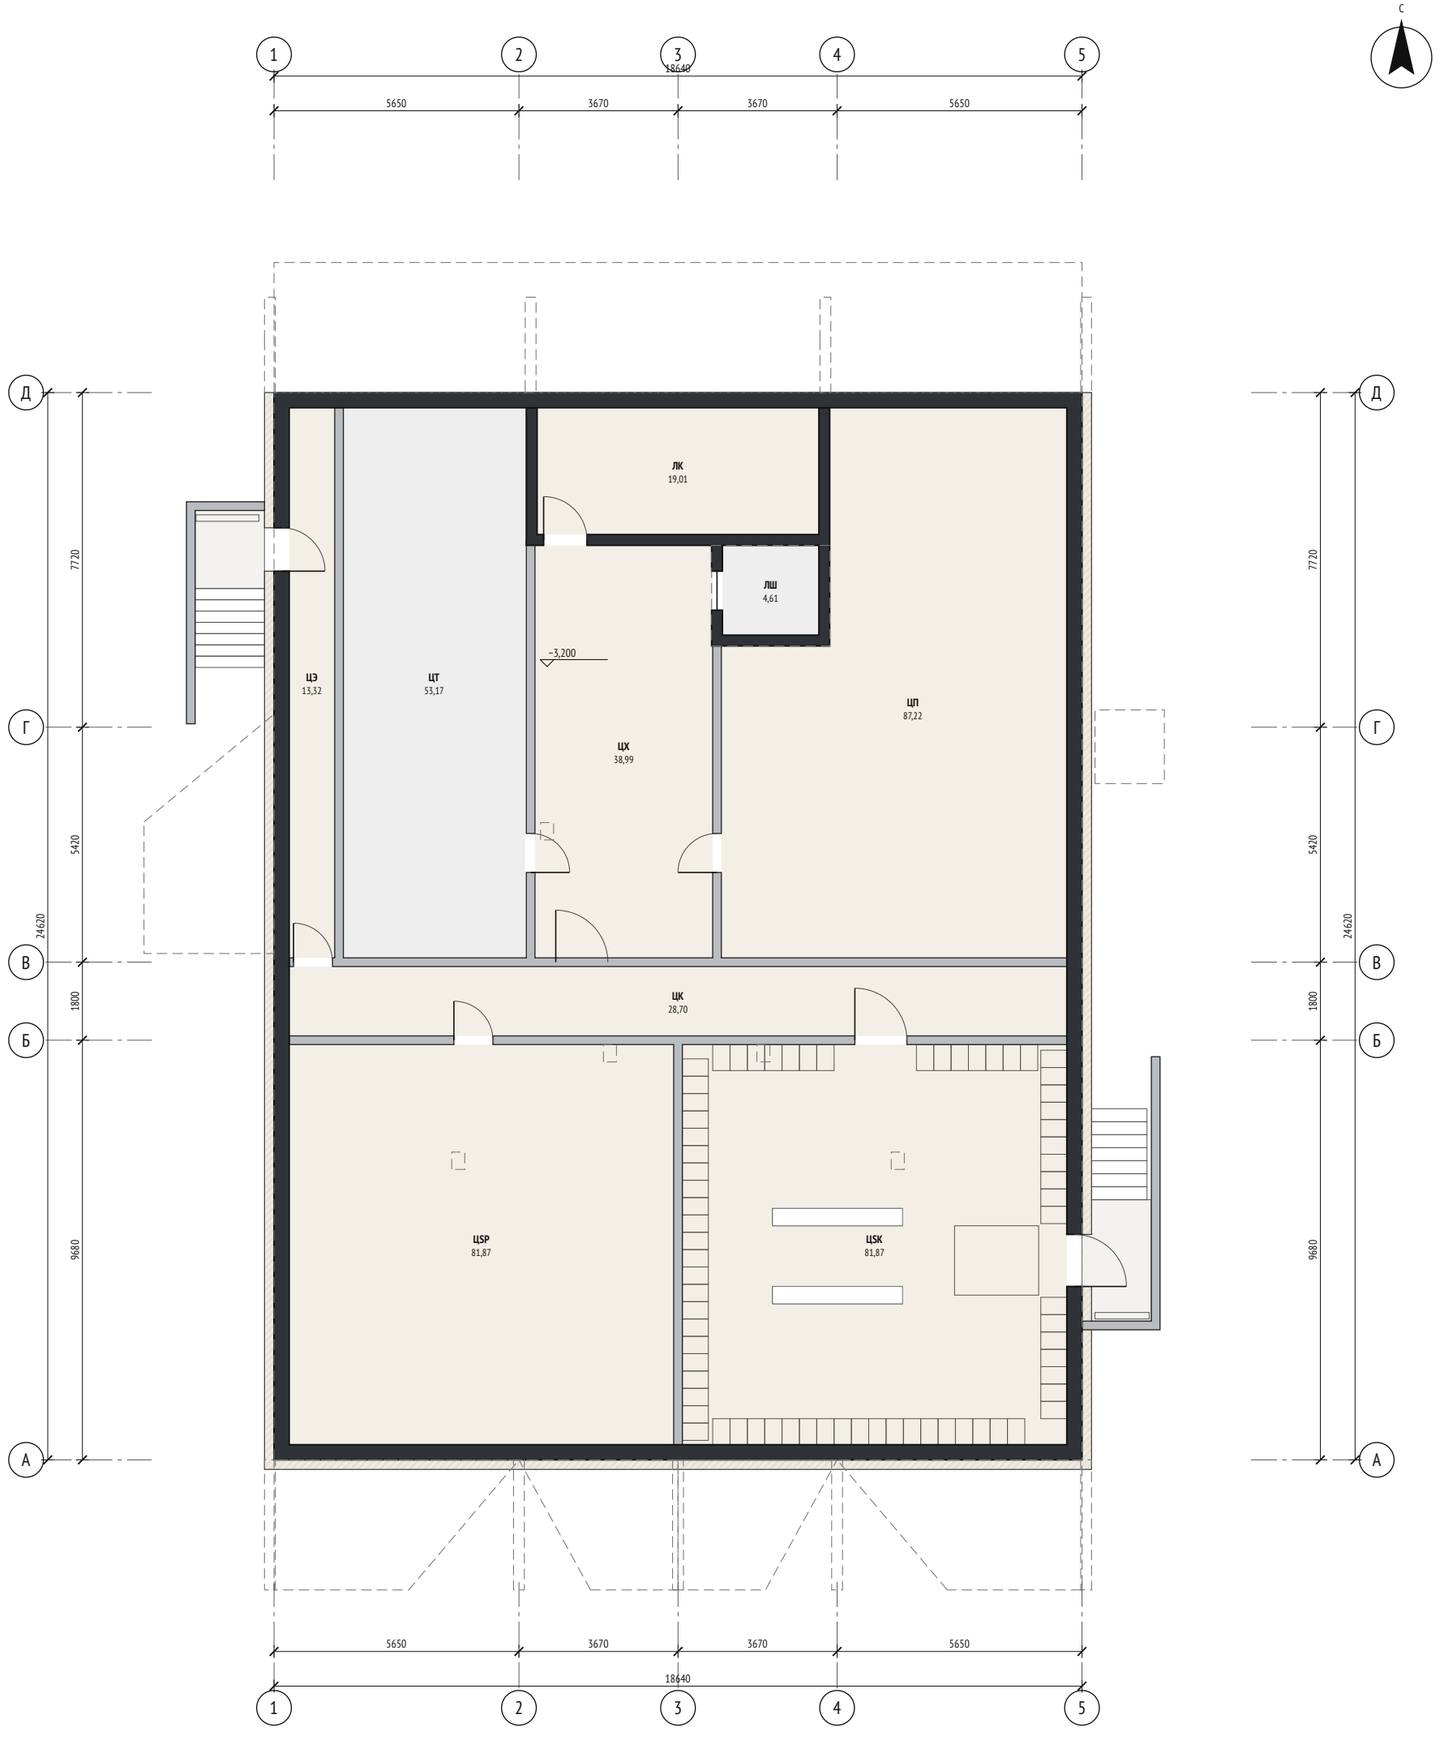

С

План полуцоколя

на отм. −3,200

Сечение IFC-модели на высоте +1,3 м от пола. Площади — по внутренним граням стен, м².

Экспликация помещений

№	Наименование	Площадь, м²	С коэф., м²
Общие и служебные помещения			
ЛШ	Шахта лифта	4,61	
ЛК	Кладовая уборочного инвентаря и белья (в объёме клетки, без марша)	19,01	
ЦSK	Ski & bike room, сушка	81,87	
ЦТ	Техпомещения: ИТП, электрощитовая, насосная	53,17	
ЦSP	Сауна, купель, отдых (резерв)	81,87	
ЦЭ	Эвакуационный коридор ко второму выходу	13,32	
ЦК	Коридор	28,70	
ЦП	Персонал, бельё, склад продуктов и холодильные шкафы кухни	87,22	
ЦХ	Лифтовый холл полуцоколя	38,99	

Обозначения: тёмная заливка — несущие наружные стены и ядро; светло-серая — перегородки; серый пунктир — консоли и плиты выше; косая штриховка снаружи — вентфасад (минвата 150 + облицовка); красный пунктир — граница квартиры.

Изм.	Кол.	Лист	№док	Подп.
Разраб.		ИИ-ассист.		10.26
Рук. пр.		Аюпов Р.		10.26
ГАП				10.26
Н. контр.				10.26

ЖР-27 · Ала-Тоо Резорт, Жыргалан · АР

Апарт-резиденция «Family Active Residence», участок 27


Жилое здание 5 эт. (мансарда) с полуцоколем, 34 апартамента

План полуцоколя на отм. −3,200

Стадия	Лист	Листов
ЭП	**2**	**12**

АР-2

М 1:100

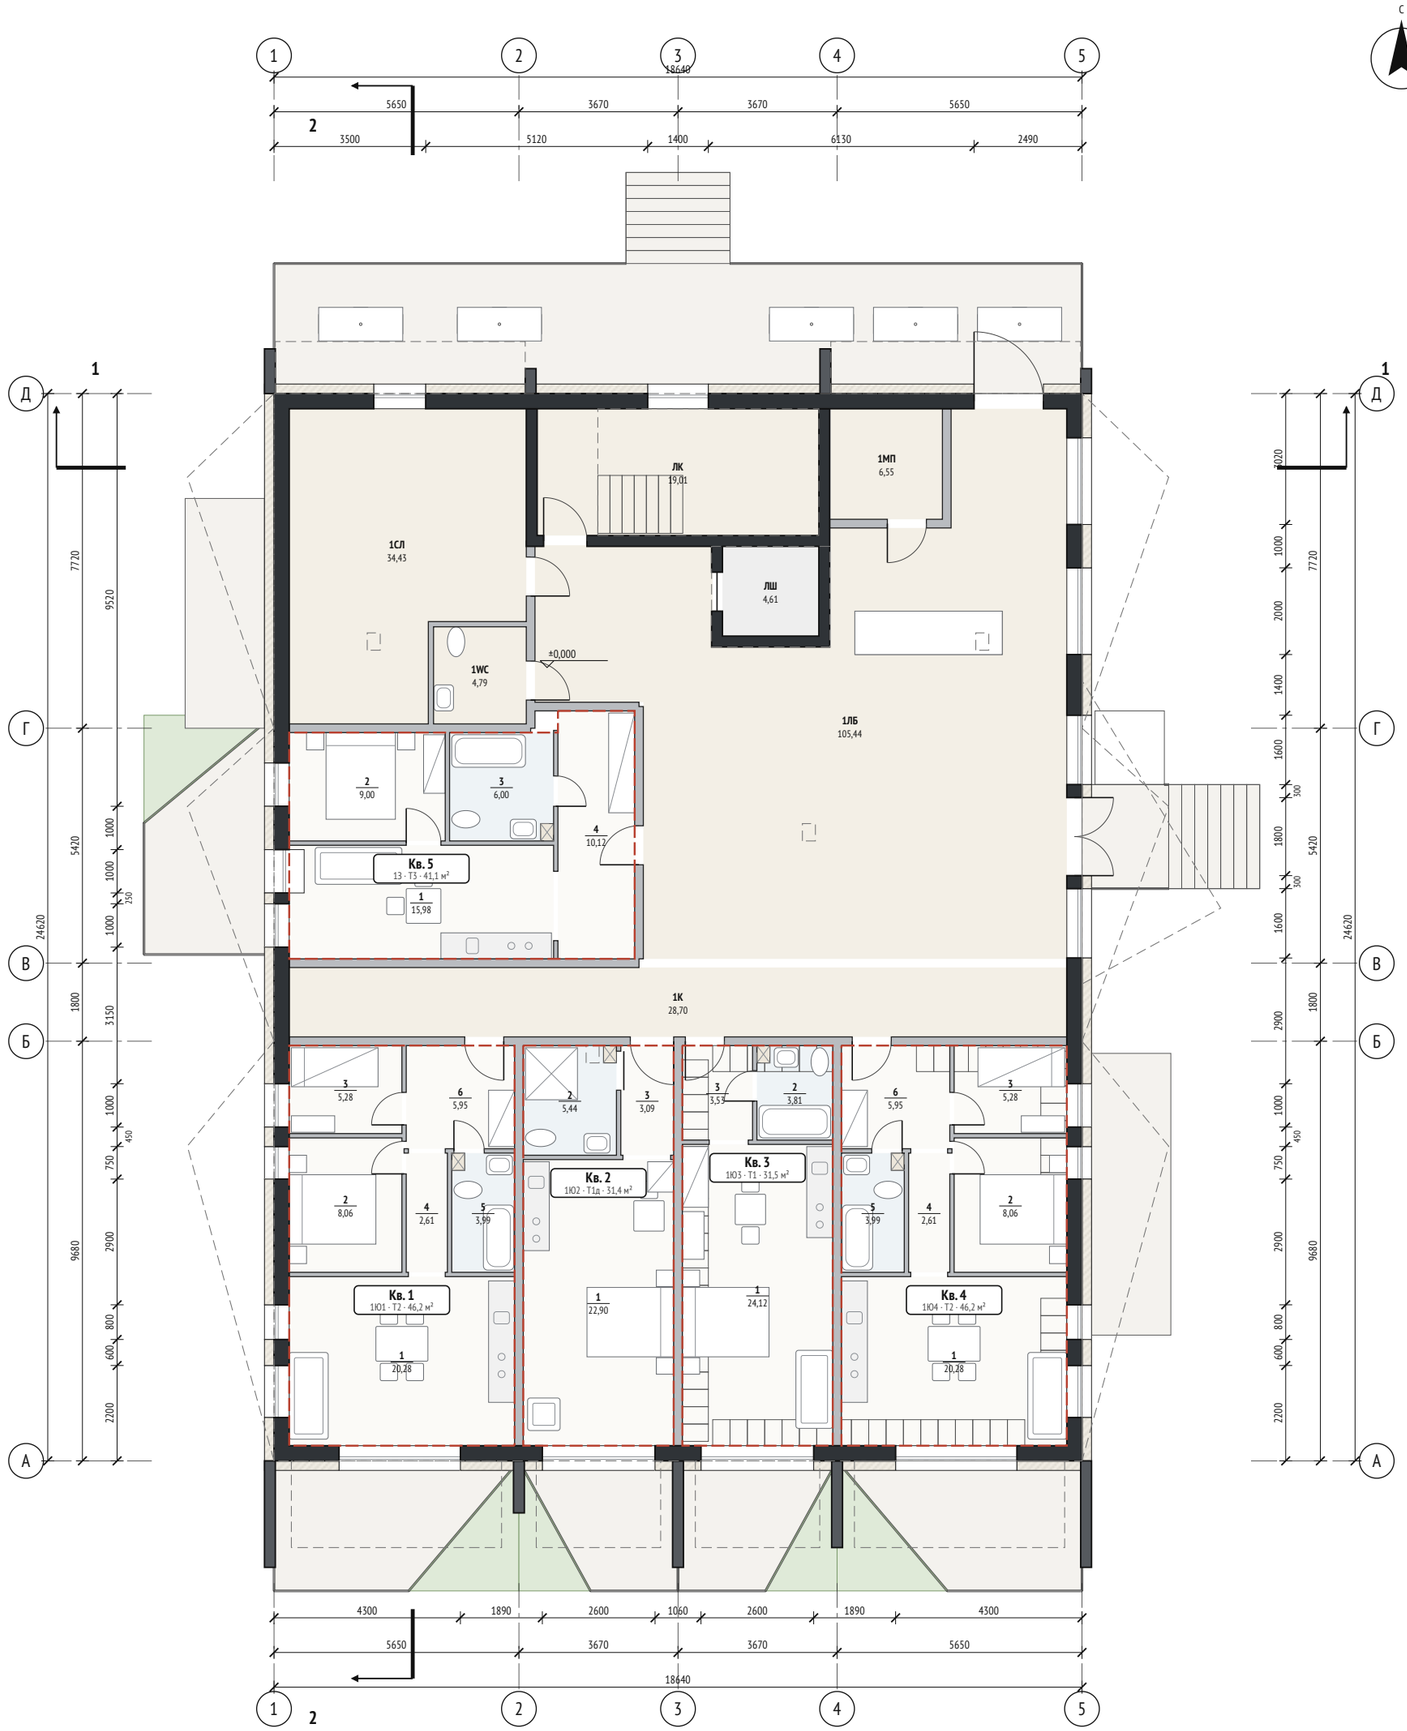

План 1 этажа

на отм. ±0,000

Сечение IFC-модели на высоте +1,3 м от пола. Площади — по внутренним граням стен, м².

Экспликация помещений


№	Наименование	Площадь, м²	С коэф., м²
Кв. 1	**1Ю1 · Т2 · Семейная угловая · 4 + 2 мест**	**46,17**	**46,17**
1	Гостиная-кухня-столовая	20,28	
2	Спальня	8,06	
3	Детская (2-ярусная кровать)	5,28	
4	Коридор	2,61	
5	Санузел (ванна)	3,99	
6	Прихожая	5,95	
	Терраса на отм. земли (не входит)	13,14	–
Кв. 2	**1Ю2 · Т1д · Студия доступная (МГН) · 2 мест**	**31,43**	**31,43**
1	Жилая комната с кухней	22,90	
2	Санузел универсальный (душ в уровне пола)	5,44	
3	Прихожая	3,09	
	Терраса на отм. земли (не входит)	8,53	–
Кв. 3	**1Ю3 · Т1 · Студия · 2 мест**	**31,46**	**31,46**
1	Жилая комната с кухней-нишей	24,12	
2	Санузел (ванна)	3,81	
3	Прихожая	3,53	
	Терраса на отм. земли (не входит)	8,53	–
Кв. 4	**1Ю4 · Т2 · Семейная угловая · 4 + 2 мест**	**46,17**	**46,17**
1	Гостиная-кухня-столовая	20,28	
2	Спальня	8,06	
3	Детская (2-ярусная кровать)	5,28	
4	Коридор	2,61	
5	Санузел (ванна)	3,99	
6	Прихожая	5,95	
	Терраса на отм. земли (не входит)	13,14	–
Кв. 5	**1З · Т3 · 1 спальня боковая · 2 + 2 мест**	**41,10**	**41,10**
1	Гостиная-кухня	15,98	
2	Спальня	9,00	
3	Санузел (ванна)	6,00	
4	Прихожая	10,12	
	Терраса на отм. земли (не входит)	12,83	–
Общие и служебные помещения			
ЛК	Лестничная клетка	19,01	
ЛШ	Шахта лифта	4,61	
1WC	Санузел универсальный общественный (МГН)	4,79	
1МП	Мойка посуды и хранение (закрытая)	6,55	
1К	Коридор	28,70	
1ЛБ	Лобби, ресепшен, лаунж-завтраки с открытой кухней-островом	105,44	
1СЛ	Персонал, бельё, багаж, офис	34,43	


Итого квартир на этаже: 5; площадь квартир 196,33 м², с летними помещениями (с коэф.) 196,33 м²

Коэффициенты летних помещений: лоджия 0,5; балкон и терраса 0,3; терраса на земле в площадь не входит.

Обозначения: тёмная заливка — несущие наружные стены и ядро; светло-серая — перегородки; серый пунктир — консоли и плиты выше; косая штриховка снаружи — вентфасад (минвата 150 + облицовка); красный пунктир — граница квартиры.

					ЖР-27 · Ала-Тоо Резорт, Жыргалан · АР
					Апарт-резиденция «Family Active Residence», участок 27
					Жилое здание 5 эт. (мансарда) с полуцоколем, 34 апартамента
Изм.	Кол.	Лист	№док	Подп.	**План 1 этажа на отм. ±0,000**
Разраб.		ИИ-ассист.		10.26	Стадия: **ЭП** · Лист: **3** · Листов: **12**
Рук. пр.		Аюпов Р.		10.26	
ГАП				10.26	**АР-3**
Н. контр.				10.26	**М 1:100**

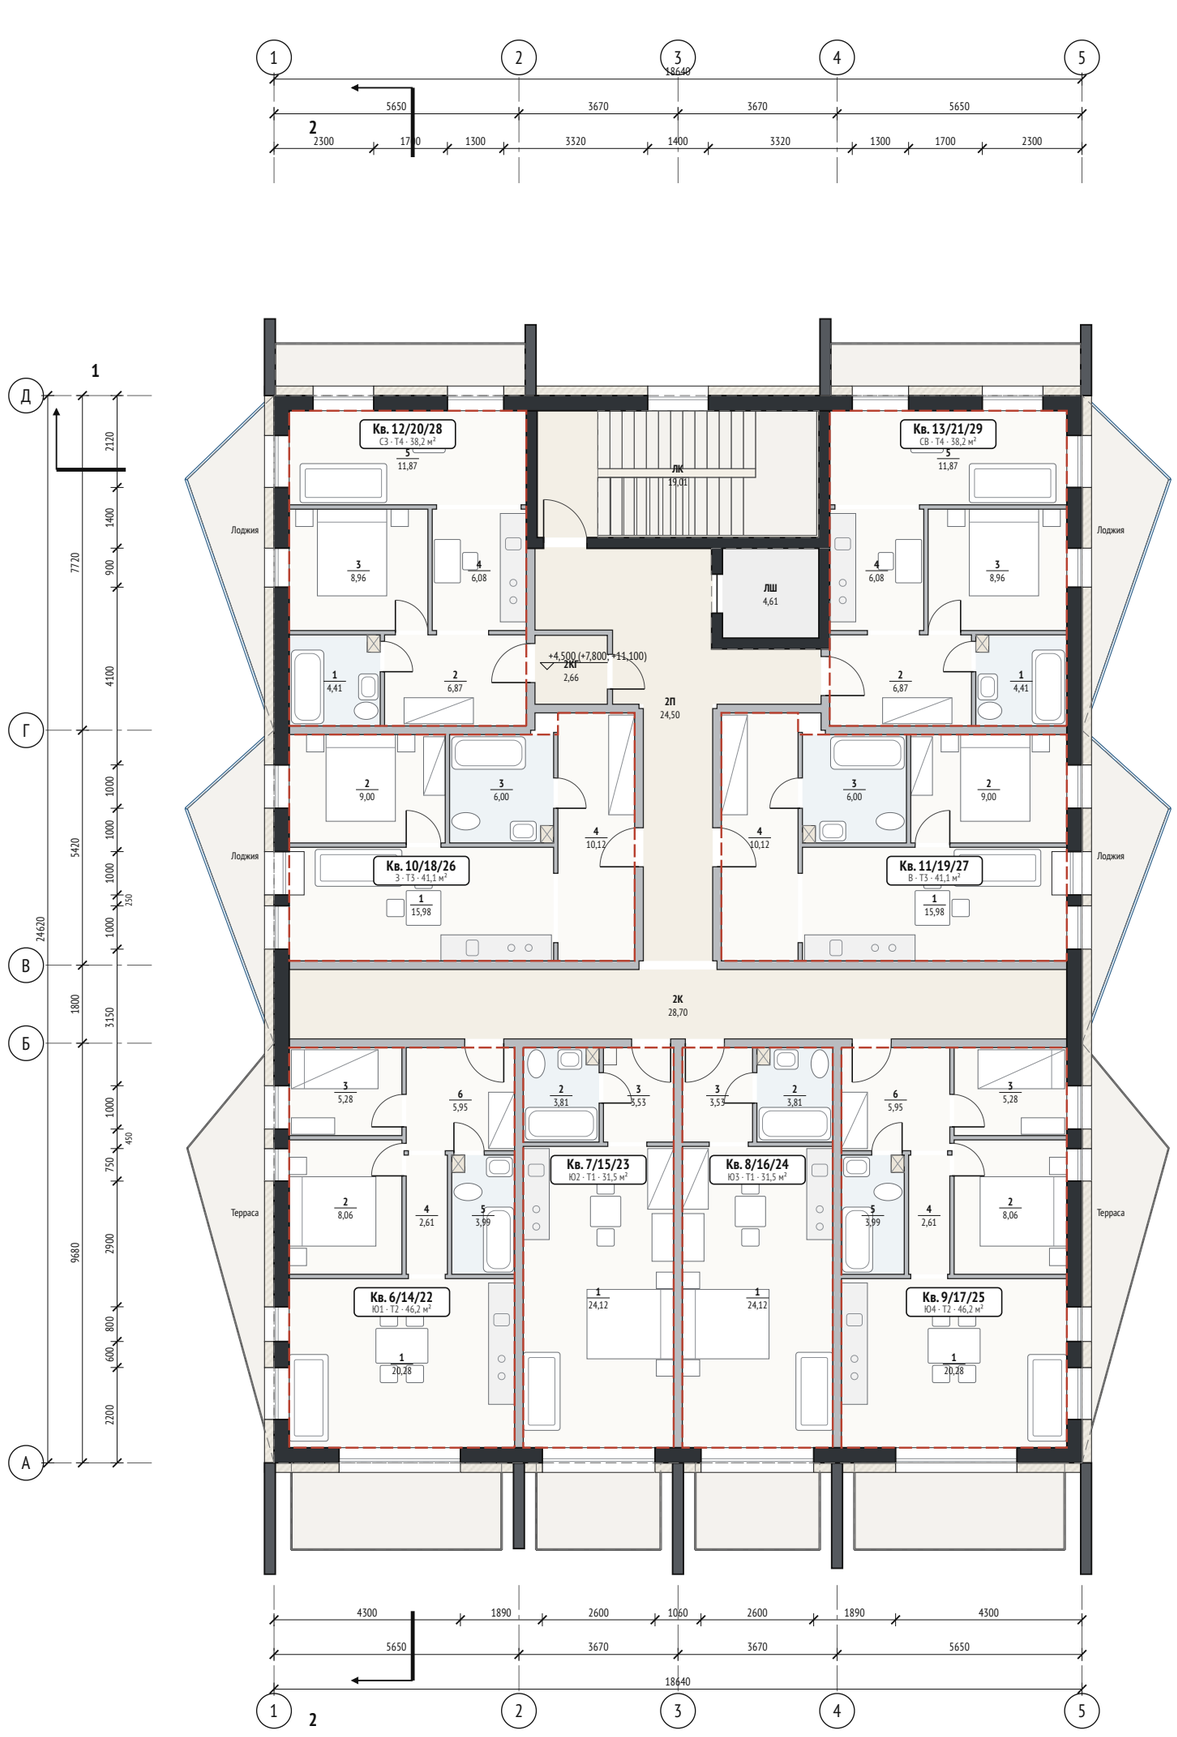

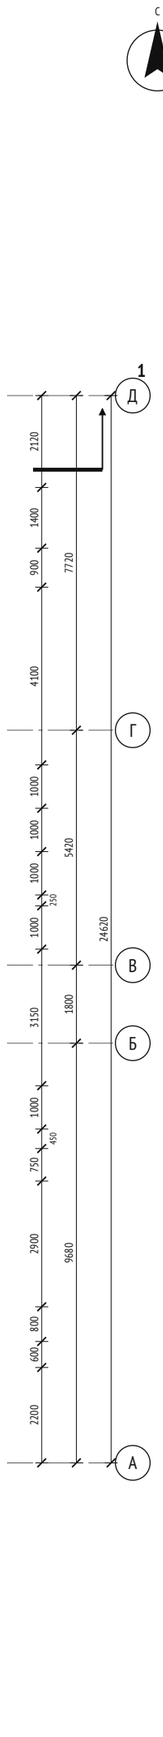

План 2–4 этажей (типовой)

на отм. +4,500; +7,800; +11,100

Сечение IFC-модели на высоте +1,3 м от пола. Площади — по внутренним граням стен, м².

Планировки 2, 3 и 4 этажей одинаковы; номера квартир указаны через дробь: 2-й/3-й/4-й этаж.

Экспликация помещений

№	Наименование	Площадь, м²	С коэф., м²
Кв. 6/14/22	**Ю1 · Т2 · Семейная угловая · 4 + 2 мест**	**46,17**	**51,98**
1	Гостиная-кухня-столовая	20,28	
2	Спальня	8,06	
3	Детская (2-ярусная кровать)	5,28	
4	Коридор	2,61	
5	Санузел (ванна)	3,99	
6	Прихожая	5,95	
	Терраса угловая (к=0.3)	9,68	2,90
	Балкон консольный (к=0.3)	9,70	2,91
Кв. 7/15/23	**Ю2 · Т1 · Студия · 2 мест**	**31,46**	**33,18**
1	Жилая комната с кухней-нишей	24,12	
2	Санузел (ванна)	3,81	
3	Прихожая	3,53	
	Балкон консольный (к=0.3)	5,74	1,72
Кв. 8/16/24	**Ю3 · Т1 · Студия · 2 мест**	**31,46**	**33,18**
1	Жилая комната с кухней-нишей	24,12	
2	Санузел (ванна)	3,81	
3	Прихожая	3,53	
	Балкон консольный (к=0.3)	5,74	1,72
Кв. 9/17/25	**Ю4 · Т2 · Семейная угловая · 4 + 2 мест**	**46,17**	**51,98**
1	Гостиная-кухня-столовая	20,28	
2	Спальня	8,06	
3	Детская (2-ярусная кровать)	5,28	
4	Коридор	2,61	
5	Санузел (ванна)	3,99	
6	Прихожая	5,95	
	Терраса угловая (к=0.3)	9,68	2,90
	Балкон консольный (к=0.3)	9,70	2,91
Кв. 10/18/26	**З · Т3 · 1 спальня боковая · 2 + 2 мест**	**41,10**	**44,71**
1	Гостиная-кухня	15,98	
2	Спальня	9,00	
3	Санузел (ванна)	6,00	
4	Прихожая	10,12	
	Лоджия холодная (к=0.5)	7,22	3,61
Кв. 11/19/27	**В · Т3 · 1 спальня боковая · 2 + 2 мест**	**41,10**	**44,71**
1	Гостиная-кухня	15,98	
2	Спальня	9,00	
3	Санузел (ванна)	6,00	
4	Прихожая	10,12	
	Лоджия холодная (к=0.5)	7,22	3,61
Кв. 12/20/28	**СЗ · Т4 · 1 спальня угловая северная · 2 + 2 мест**	**38,19**	**44,13**
1	Санузел (ванна)	4,41	
2	Прихожая	6,87	
3	Спальня	8,96	
4	Кухня-столовая	6,08	
5	Гостиная	11,87	
	Лоджия холодная (к=0.5)	7,72	3,86
	Балкон консольный (к=0.3)	6,92	2,08
Кв. 13/21/29	**СВ · Т4 · 1 спальня угловая северная · 2 + 2 мест**	**38,19**	**44,13**
1	Санузел (ванна)	4,41	
2	Прихожая	6,87	
3	Спальня	8,96	
4	Кухня-столовая	6,08	
5	Гостиная	11,87	
	Лоджия холодная (к=0.5)	7,72	3,86
	Балкон консольный (к=0.3)	6,92	2,08
Общие и служебные помещения			
ЛК	Лестничная клетка	19,01	
ЛШ	Шахта лифта	4,61	
2КГ	Кладовая горничной: бельё, тележка, инвентарь, раковина	2,66	
2К	Коридор	28,70	
2П	Проход и лифтовый холл	24,50	

Итого квартир на этаже: 8; площадь квартир 313,84 м², с летними помещениями (с коэф.) 348,00 м²

Коэффициенты летних помещений: лоджия 0,5; балкон и терраса 0,3; терраса на земле в площадь не входит.

Обозначения: тёмная заливка — несущие наружные стены и ядро; светло-серая — перегородки; серый пунктир — консоли и плиты выше; косая штриховка снаружи — вентфасад (минвата 150 + облицовка); красный пунктир — граница квартиры.

					ЖР-27 · Ала-Тоо Резорт, Жыргалан · АР
					Апарт-резиденция «Family Active Residence», участок 27
					Жилое здание 5 эт. (мансарда) с полуцоколем, 34 апартамента
Изм.	Кол.	Лист	№док	Дата	**План 2–4 этажей (типовой)** на отм. +4,500; +7,800; +11,100
Разраб.		ИИ-ассист.		10.26	Стадия: **ЭП** · Лист: **4** · Листов: **12**
Рук. пр.		Аюпов Р.		10.26	
ГАП				10.26	**АР-4**
Н. контр.				10.26	**М 1:100**



План мансардного (5) этажа

на отм. +14,400

Сечение IFC-модели на высоте +1,3 м от пола. Площади — по внутренним граням стен, м².

Экспликация помещений

№	Наименование	Площадь, м²	С коэф., м²
Кв. 30	**5П3 · Т6 · Пентхаус западный · 4 + 2 мест**	**81,36**	**86,34**
1	Гостиная с панорамным витражом	25,71	
2	Спальня 2	11,56	
3	Мастер-спальня	15,25	
4	Коридор	2,60	
5	Кухня-столовая	12,01	
6	Мастер-ванная (ванна)	4,71	
7	Гостевой санузел (душ)	3,33	
8	Прихожая	4,65	
9	Тамбур	1,54	
	Балкон консольный (к=0.3)	16,60	4,98
Кв. 31	**5ПВ · Т7 · Пентхаус-люкс восточный · 4 + 2 мест**	**123,51**	**128,49**
1	Гостиная-столовая-кухня с панорамным витражом	41,25	
2	ТВ-холл	8,76	
3	Галерея	5,35	
4	Гостевой санузел (душ)	3,19	
5	Сауна	2,42	
6	Гардеробная	2,40	
7	Мастер-спальня	16,08	
8	Мастер-ванная (ванна + душ)	8,14	
9	Прихожая и холл	10,16	
10	Спальня 2	18,68	
11	Кладовая	7,08	
	Балкон консольный (к=0.3)	16,60	4,98
Кв. 32	**53 · Т5а · Мансардная западная (1 спальня) · 2 + 2 мест**	**44,41**	**44,41**
1	Гостиная	19,52	
2	Кухня-ниша	2,40	
3	Спальня	10,15	
4	Санузел (ванна)	4,13	
5	Прихожая	8,21	
Кв. 33	**5С3 · Т5 · Семейная мансардная северо-западная · 4 + 2 мест**	**44,58**	**46,66**
1	Детская (2-ярусная кровать)	6,91	
2	Прихожая	5,91	
3	Коридор	1,62	
4	Санузел (душ)	3,26	
5	Спальня	7,56	
6	Кухня-столовая	9,36	
7	Гостиная	9,96	
	Балкон консольный (к=0.3)	6,92	2,08
Кв. 34	**5СВ · Т56 · Семейная мансардная северо-восточная · 4 + 2 мест**	**45,33**	**47,41**
1	Прихожая	6,83	
2	Детская (2-ярусная кровать)	5,81	
3	Санузел (ванна)	5,81	
4	Кухня-столовая	8,76	
5	Спальня	8,16	
6	Гостиная	9,96	
	Балкон консольный (к=0.3)	6,92	2,08
Общие и служебные помещения			
ЛШ	Шахта лифта	4,61	
ЛК	Лестничная клетка	19,01	
5П	Проход и лифтовый холл	30,25	

Итого квартир на этаже: 5; площадь квартир 339,19 м², с летними помещениями (с коэф.) 353,30 м²

Коэффициенты летних помещений: лоджия 0,5; балкон и терраса 0,3; терраса на земле в площадь не входит.

Обозначения: тёмная заливка — несущие наружные стены и ядро; светло-серая — перегородки; серый пунктир — консоли и плиты выше; косая штриховка снаружи — вентфасад (минвата 150 + облицовка); красный пунктир — граница квартиры; синий пунктир с крестом — мансардное окно в скате кровли (выше секущей).

Изм.	Кол.	Лист	№док	Подп.	Дата
Разраб.		ИИ-ассист.			10.26
Рук. пр.		Аюпов Р.			10.26
ГАП					10.26
Н. контр.					10.26

ЖР-27 · Ала-Тоо Резорт, Жыргалан · АР

Апарт-резиденция «Family Active Residence», участок 27


Жилое здание 5 эт. (мансарда) с полуцоколем, 34 апартамента

План мансардного (5) этажа на отм. +14,400

Стадия	Лист	Листов
ЭП	**5**	**12**

АР-5

М 1:100

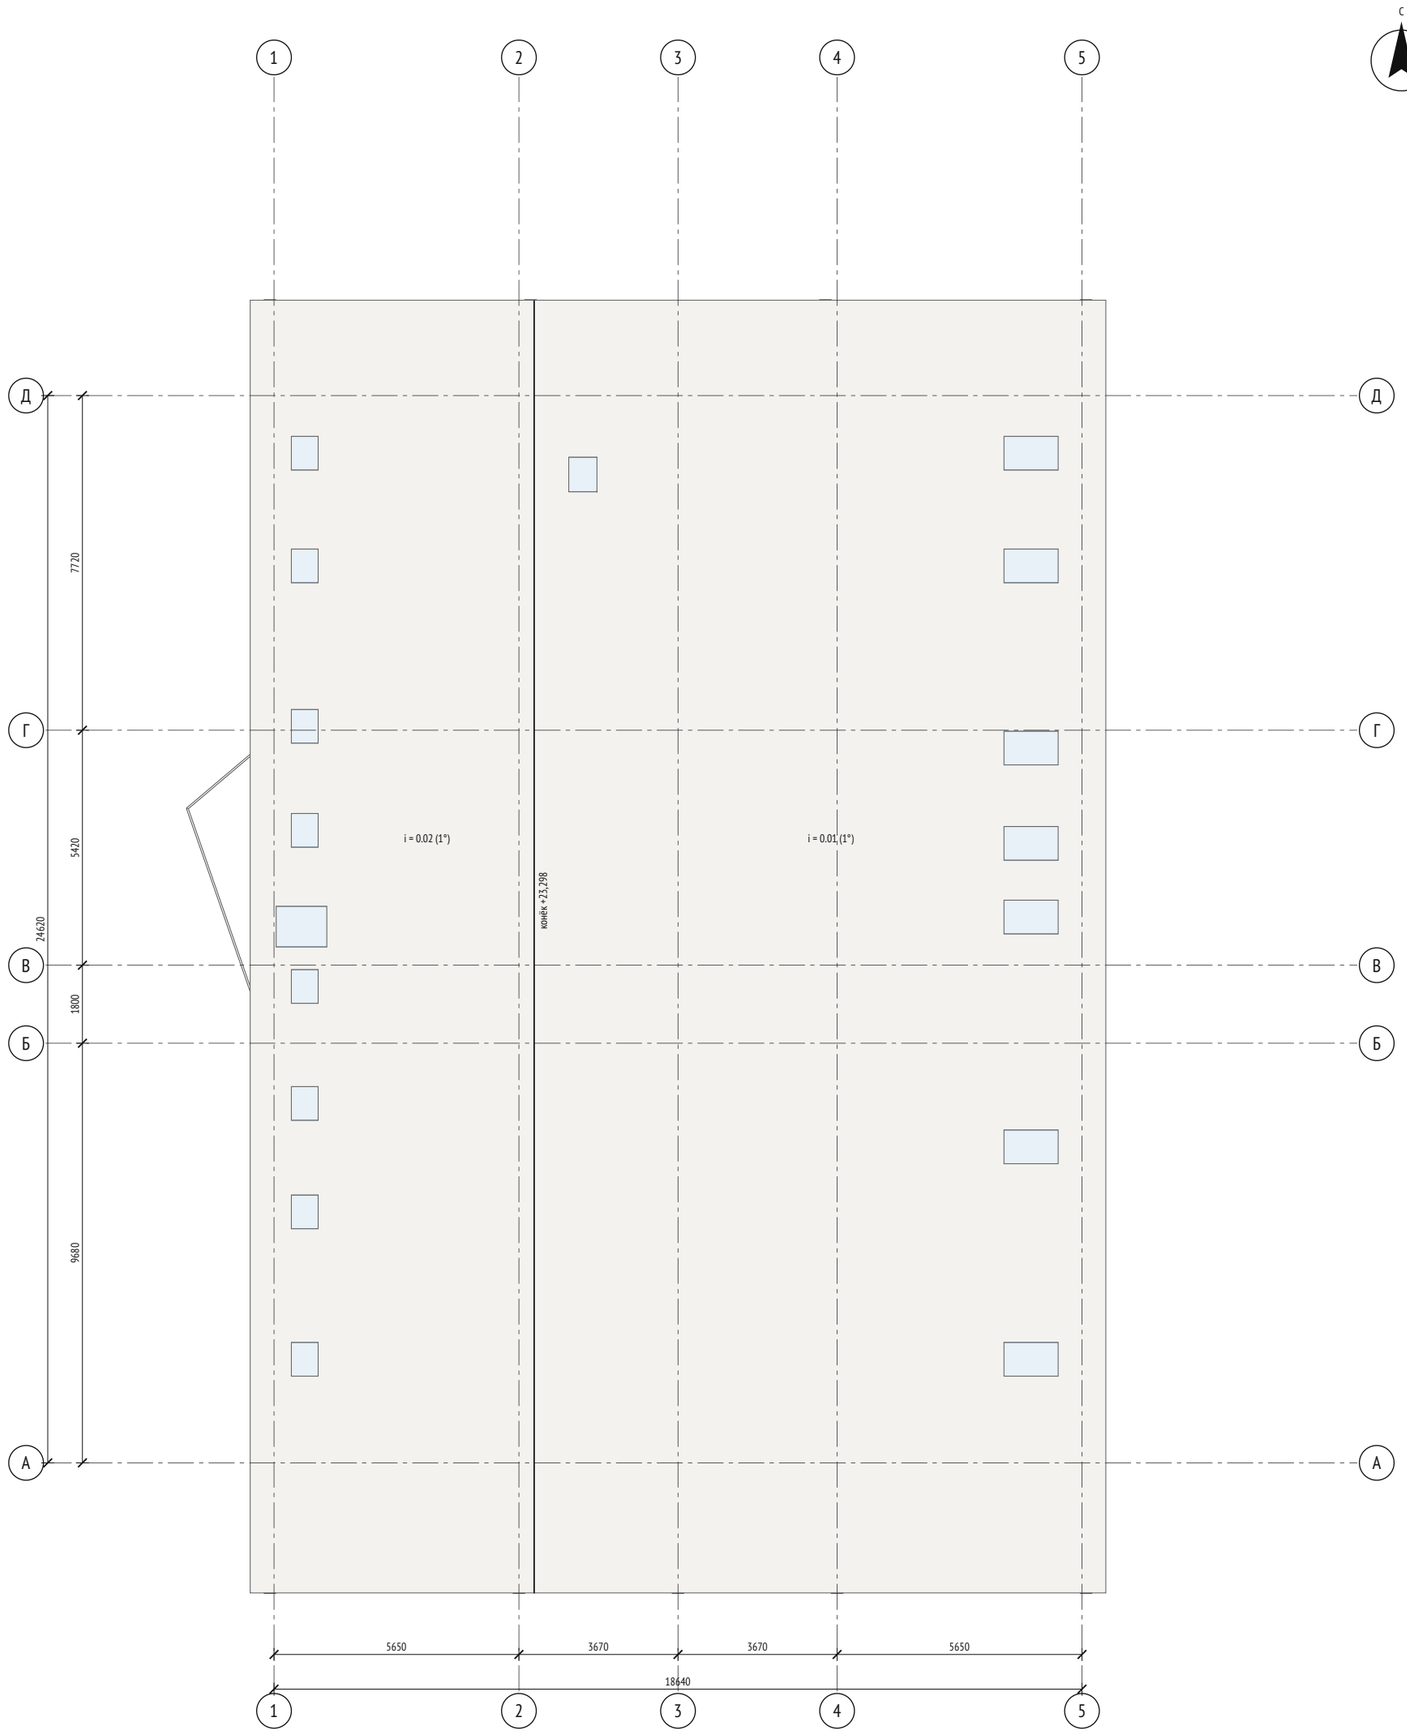

План кровли

- Асимметричная двускатная кровля: западный скат крутой, восточный 30°.
- Конёк смещён к западу на ось x = 6,00 м от оси 1.
- Отметка конька +23,298 м, от земли 24.5 м (предел 22–25 м).
- Свес кровли: юг 3,0 м, север 2,2 м — над боковинами-изломами.
- Тёмные полосы — боковины-изломы, выведенные до кровли.
- Голубым — мансардные окна в скатах.
- Водосток, снегозадержание, кровельный пирог — на стадии П.

Изм.	Кол.	Лист	№док	Подп.
Разраб.		ИИ-ассист.		10.26
Рук. пр.		Аюпов Р.		10.26
ГАП				10.26
Н. контр.				10.26

ЖР-27 · Ала-Тоо Резорт, Жыргалан · АР

Апарт-резиденция «Family Active Residence», участок 27

Жилое здание 5 эт. (мансарда) с полуцоколем, 34 апартамента

План кровли

Стадия	Лист	Листов
ЭП	**6**	**12**

АР-6


М 1:100

Фасад 1–5 (южный)

Главный фасад к склону и солнцу: тёмные рёбра-изломы выносом до 3 м, балконы между ними, панорамный фронтон пентхаусов. Снегозадержатели и обогрев водостоков — по стадии П.

Материалы фасада (вариант Б3)

1. Кровля и южные рёбра: фальц, сталь 0,6 мм PVDF, графит матовый
2. Рёбра севера, изломы, козырёк: алюминиевые кассеты, графит матовый (в тон кровли)
3. Стены: керамогранит 300×1200 вертикально вразбежку, 3 тона тёмного тёплого базальта; внизу темнее, к мансарде светлее
4. Цоколь, приямок лыжного входа: гранит термообработанный
5. Окна, витражи, остекление лоджий: алюминий с терморазрывом, графит; тройной стеклопакет
6. Ограждения балконов: закалённое стекло триплекс, поручень графит
7. Террасы, заборчики 1-го этажа, терраса кафе: лиственница термообработанная

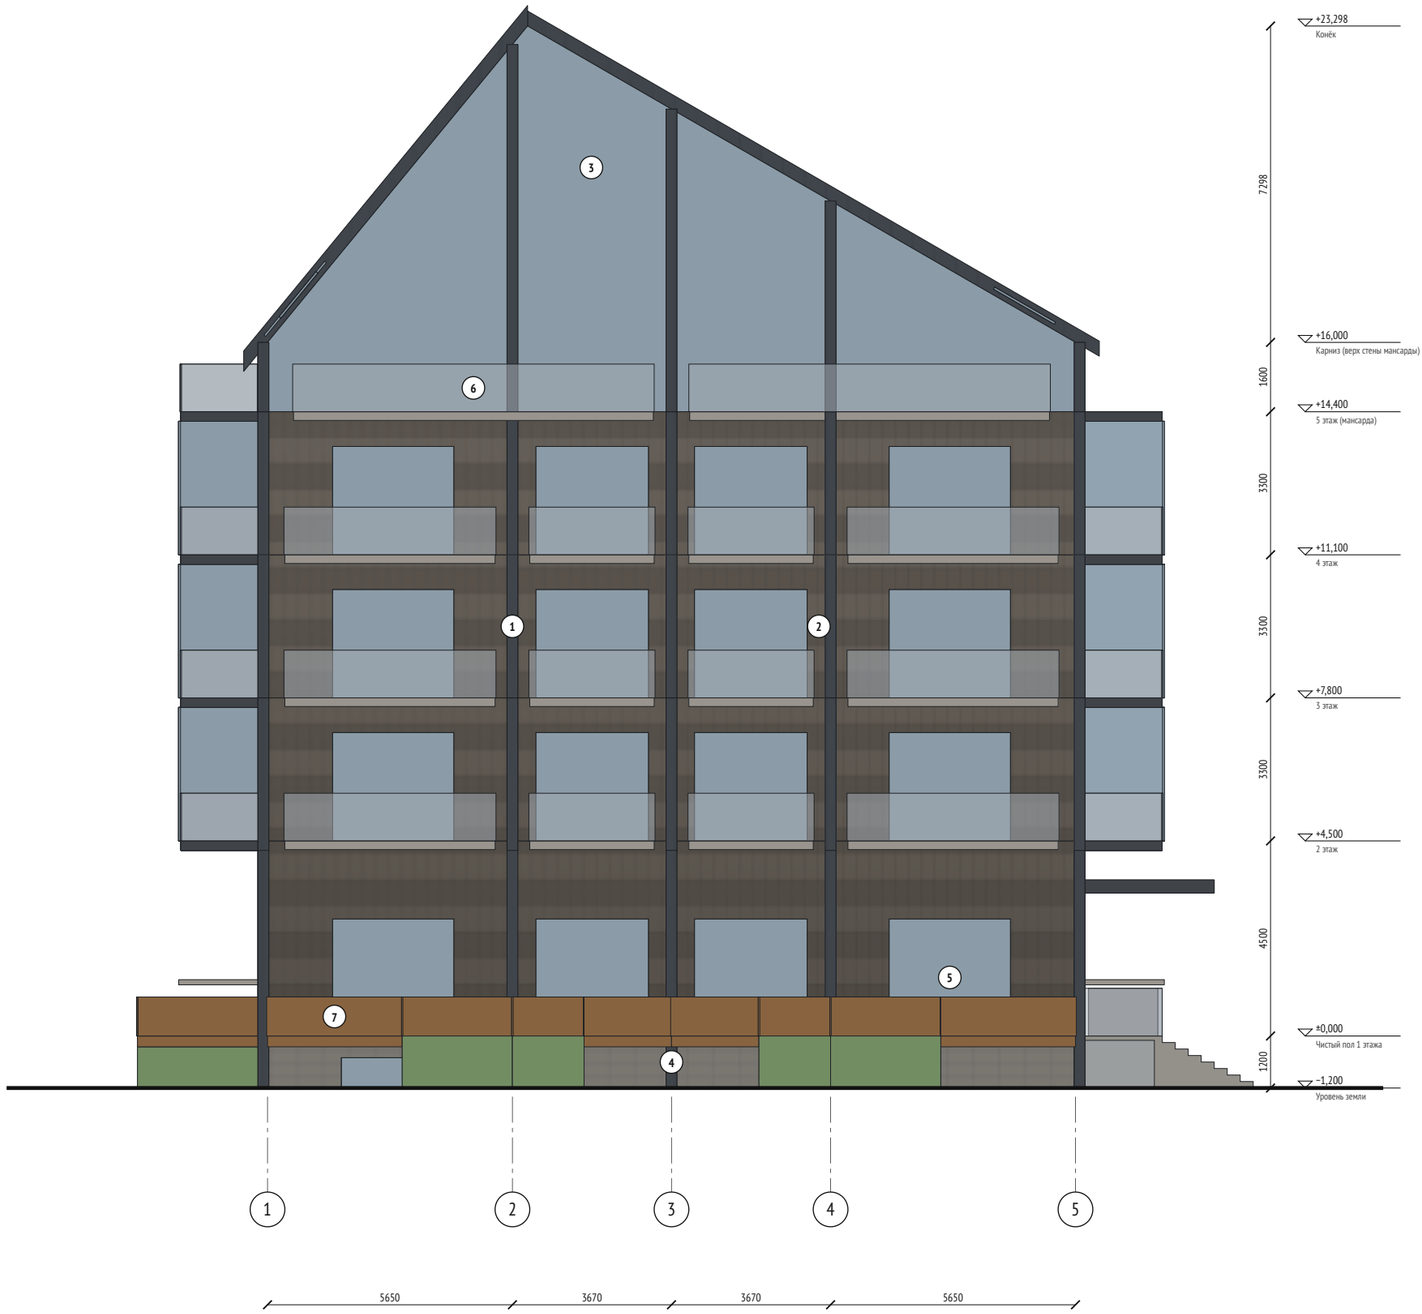


					ЖР-27 · Ала-Тоо Резорт, Жыргалан · АР
					Апарт-резиденция «Family Active Residence», участок 27
					Жилое здание 5 эт. (мансарда) с полуцоколем, 34 апартамента
Изм.	Кол.	Лист	№док	Подп.	**Фасад 1–5 (южный)**
Разраб.		ИИ-ассист.		10.26	Стадия: **ЭП** · Лист: **7** · Листов: **12**
Рук. пр.		Аюпов Р.		10.26	
ГАП				10.26	**АР-7**
Н. контр.				10.26	**М 1:100**

Фасад 5–1 (северный)

Фасад к площади №14: терраса кафе-завтраков на всю ширину, балконы между рёбрами, окна фронтона семейных квартир мансарды и лестничной клетки.

Материалы фасада (вариант Б3)

1. Кровля и южные рёбра: фальц, сталь 0,6 мм PVDF, графит матовый
2. Рёбра севера, изломы, козырёк: алюминиевые кассеты, графит матовый (в тон кровли)
3. Стены: керамогранит 300×1200 вертикально вразбежку, 3 тона тёмного тёплого базальта; внизу темнее, к мансарде светлее
4. Цоколь, приямок лыжного входа: гранит термообработанный
5. Окна, витражи, остекление лоджий: алюминий с терморазрывом, графит; тройной стеклопакет
6. Ограждения балконов: закалённое стекло триплекс, поручень графит
7. Террасы, заборчики 1-го этажа, терраса кафе: лиственница термообработанная

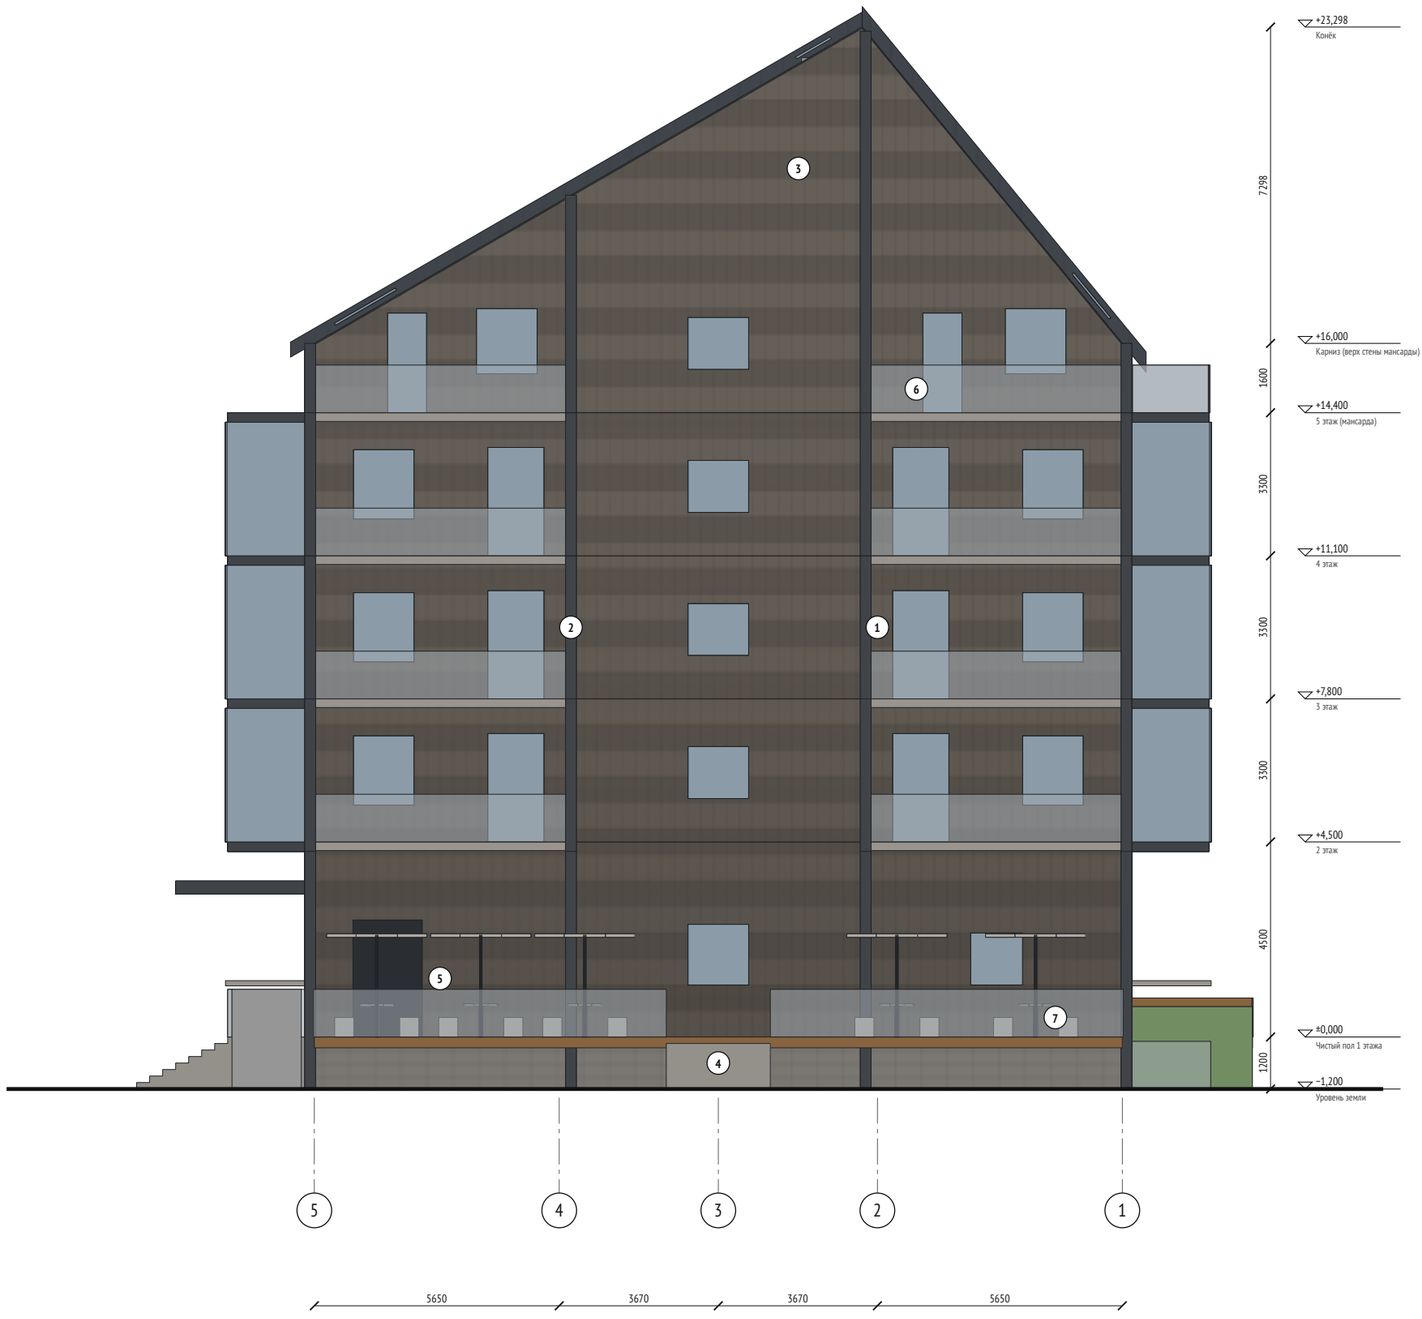

Изм.	Кол.	Лист	№док	Дата
Разраб.		ИИ-ассист.		10.26
Рук. пр.		Аюпов Р.		10.26
ГАП				10.26
Н. контр.				10.26

ЖР-27 · Ала-Тоо Резорт, Жыргалан · АР

Апарт-резиденция «Family Active Residence», участок 27

Жилое здание 5 эт. (мансарда) с полуколем, 34 апартамента

Фасад 5–1 (северный)

Стадия	Лист	Листов
ЭП	8	12

АР-8

М 1:100

Фасад А–Д (восточный)

Главный вход с треугольным козырьком и лестницей; лыжный спуск в полуцоколь у юго-восточного угла.

Пологий скат 30° над входом: снегозадержание в 2–3 ряда и защита козырька обязательны.

Материалы фасада (вариант Б3)

1. Кровля и южные рёбра: фальц, сталь 0,6 мм PVDF, графит матовый
2. Рёбра севера, изломы, козырёк: алюминиевые кассеты, графит матовый (в тон кровли)
3. Стены: керамогранит 300×1200 вертикально вразбежку, 3 тона тёмного тёплого базальта; внизу темнее, к мансарде светлее
4. Цоколь, приямок лыжного входа: гранит термообработанный
5. Окна, витражи, остекление лоджий: алюминий с терморазрывом, графит; тройной стеклопакет
6. Ограждения балконов: закалённое стекло триплекс, поручень графит
7. Террасы, заборчики 1-го этажа, терраса кафе: лиственница термообработанная



Изм.	Кол.	Лист	№док	Подп.	Дата
Разраб.		ИИ-ассист.			10.26
Рук. пр.		Аюпов Р.			10.26
ГАП					10.26
Н. контр.					10.26

ЖР-27 · Ала-Тоо Резорт, Жыргалан · АР

Апарт-резиденция «Family Active Residence», участок 27

Жилое здание 5 эт. (мансарда) с полуцоколем, 34 апартамента

Фасад А–Д (восточный)

Стадия	Лист	Листов
ЭП	9	12

АР-9

М 1:100


Фасад Д–А (западный)

Крутой скат 51°, мансардные окна в скате; плиты-изломы с лоджиями и угловой террасой.

Снег с западного ската сходит на террасы-изломы: козырьки и снегозадержание по стадии П.

Материалы фасада (вариант Б3)

1. Кровля и южные рёбра: фальц, сталь 0,6 мм PVDF, графит матовый
2. Рёбра севера, изломы, козырёк: алюминиевые кассеты, графит матовый (в тон кровли)
3. Стены: керамогранит 300×1200 вертикально вразбежку, 3 тона тёмного тёплого базальта; внизу темнее, к мансарде светлее
4. Цоколь, приямок лыжного входа: гранит термообработанный
5. Окна, витражи, остекление лоджий: алюминий с терморазрывом, графит; тройной стеклопакет
6. Ограждения балконов: закалённое стекло триплекс, поручень графит
7. Террасы, заборчики 1-го этажа, терраса кафе: лиственница термообработанная

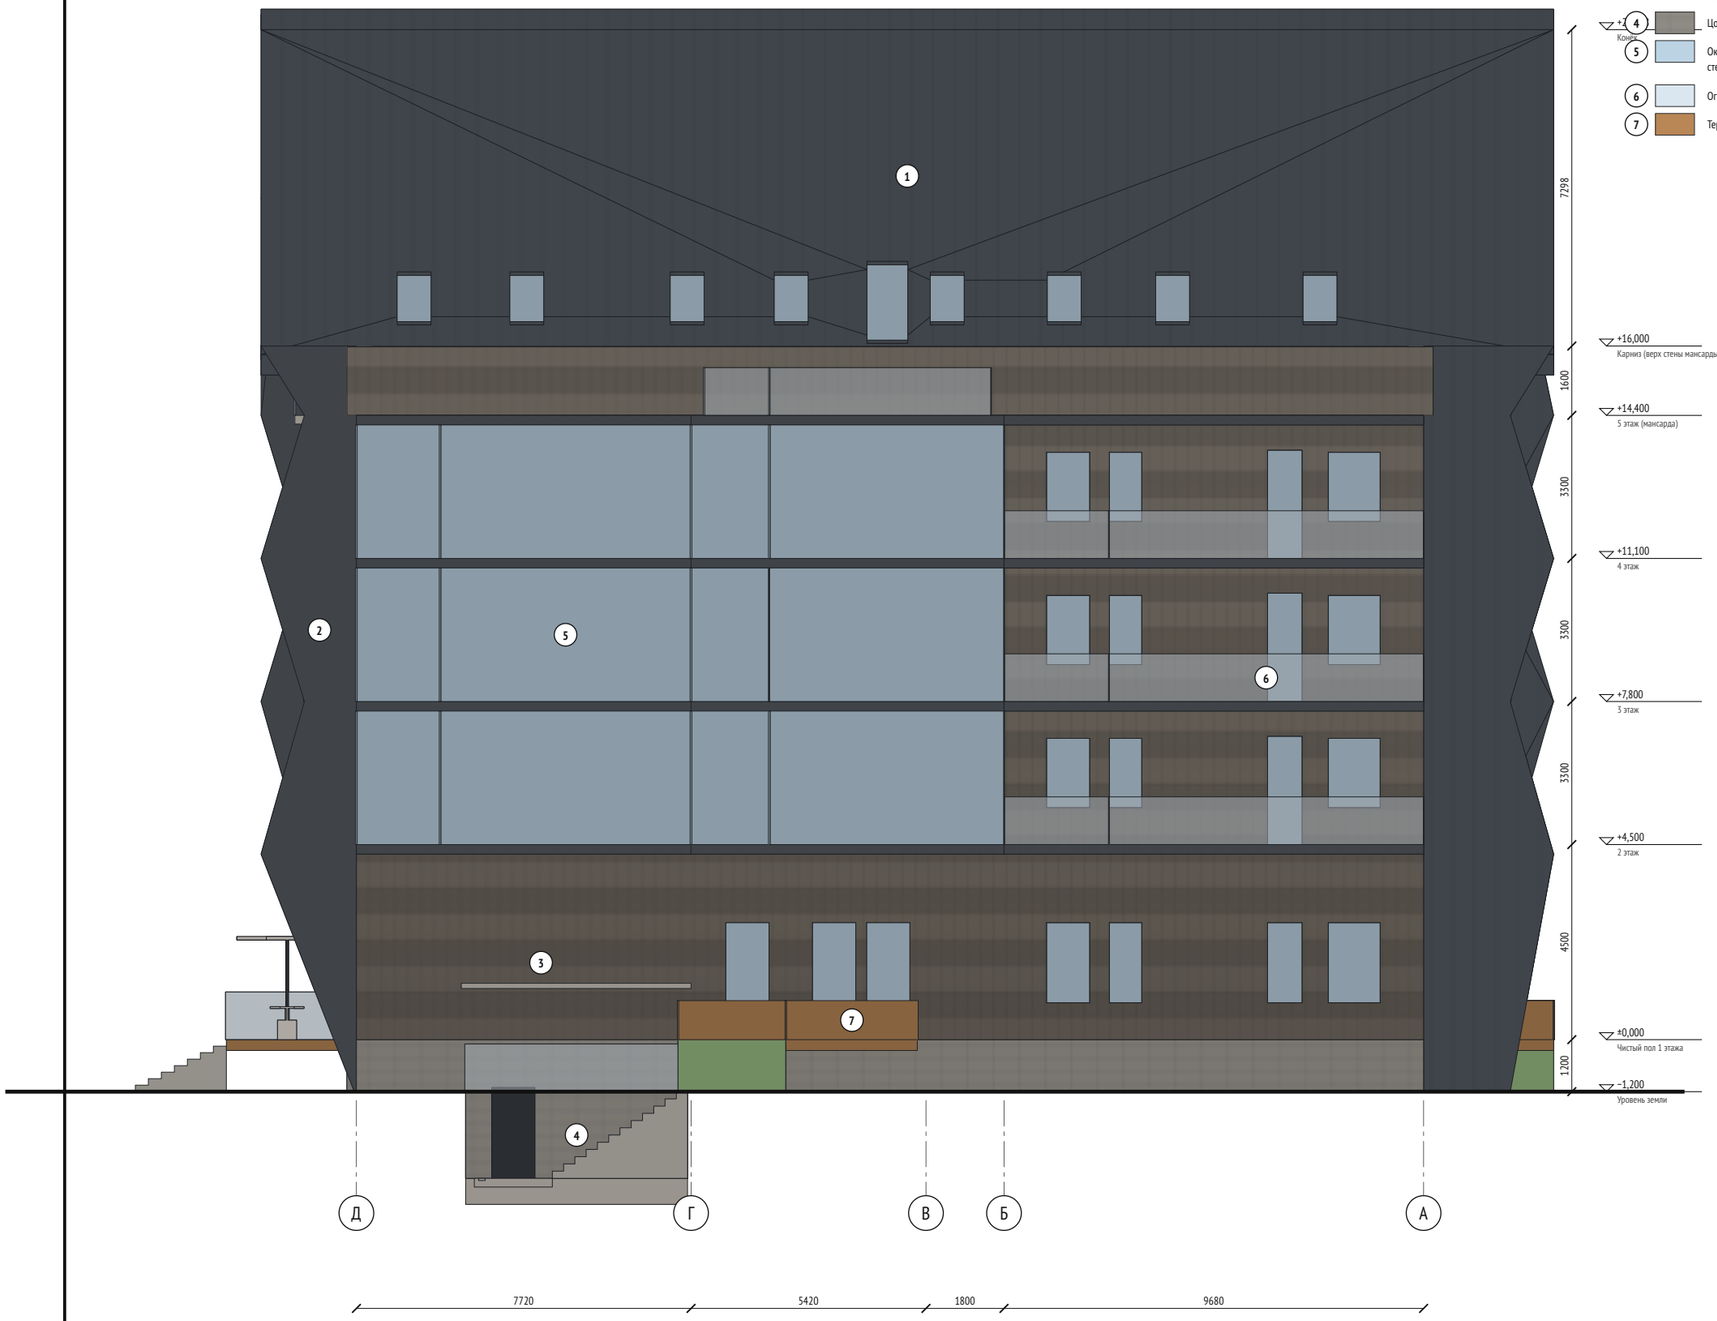

Изм.	Кол.	Лист	№док	Подп.	Дата
Разраб.		ИИ-ассист.			10.26
Рук. пр.		Аюпов Р.			10.26
ГАП					10.26
Н. контр.					10.26

ЖР-27 · Ала-Тоо Резорт, Жыргалан · АР

Апарт-резиденция «Family Active Residence», участок 27

Жилое здание 5 эт. (мансарда) с полуцоколем, 34 апартамента

Фасад Д–А (западный)

Стадия	Лист	Листов
ЭП	10	12


АР-10

М 1:100

Разрез 1-1

Поперечный разрез через лестницу и шахту лифта, вид на север.


Показаны асимметричная кровля (51° / 30°), высоты этажей, марши на полный перепад пол – пол.

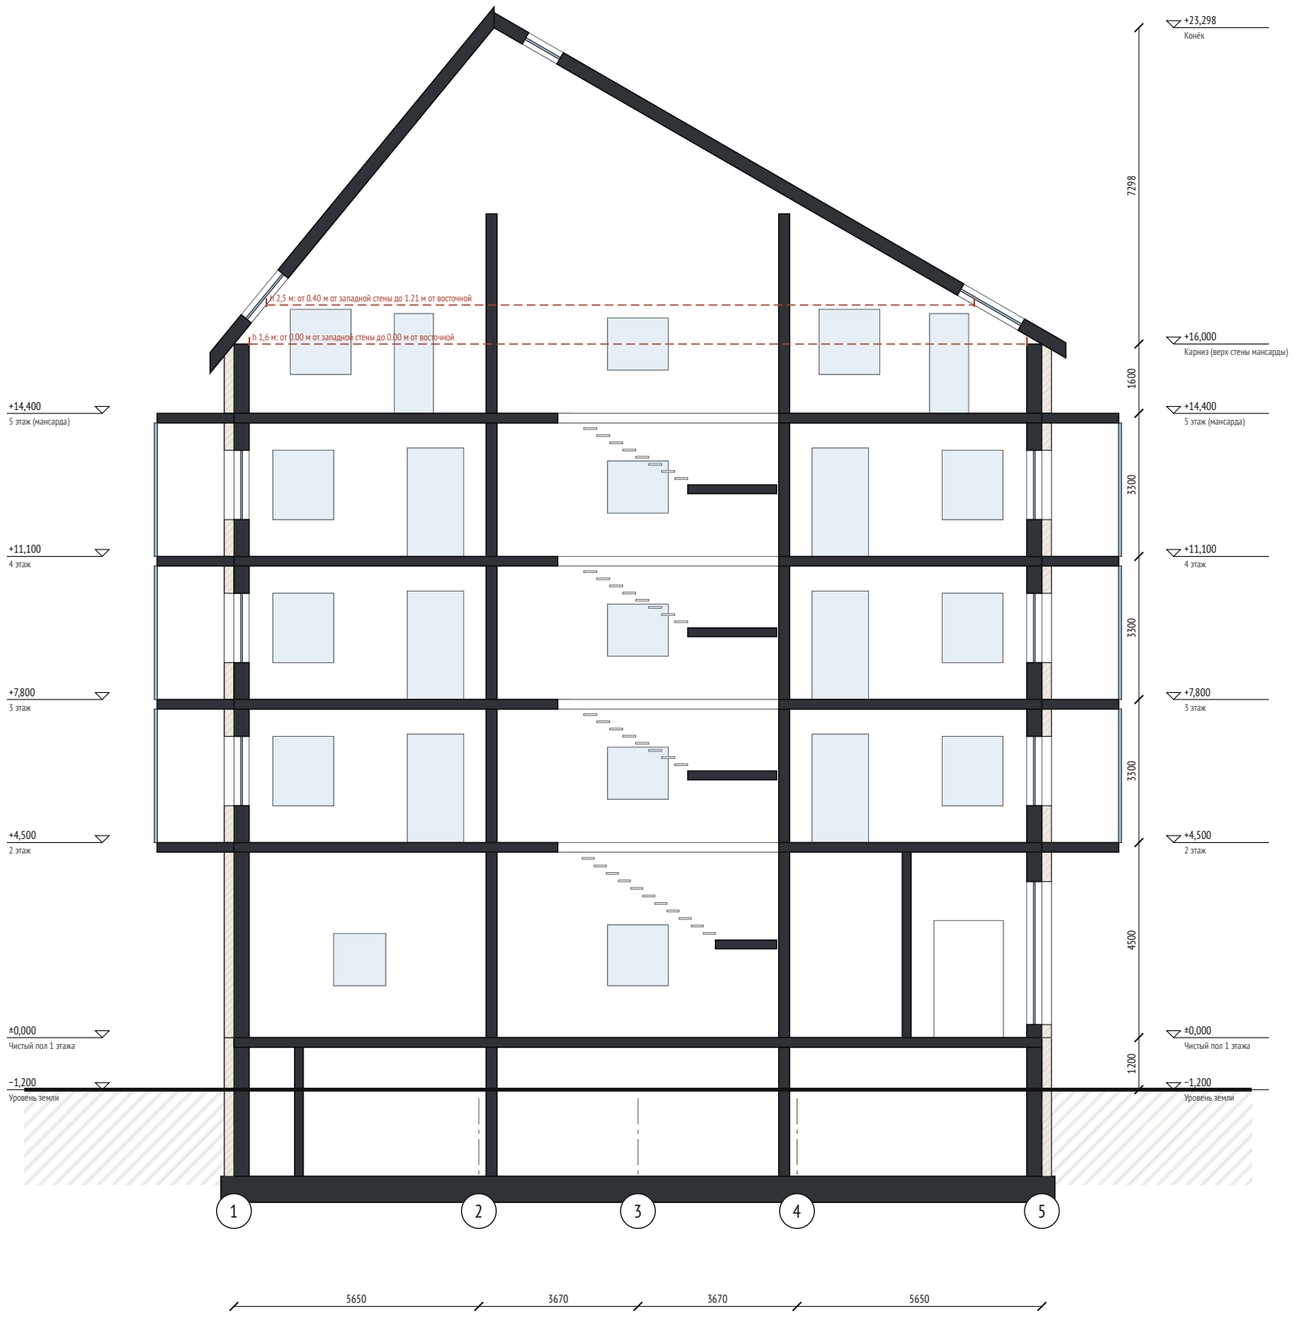

					ЖР-27 · Ала-Тоо Резорт, Жыргалан · АР	
					Апарт-резиденция «Family Active Residence», участок 27	
					Жилое здание 5 эт. (мансарда) с полуцоколем, 34 апартамента	
Изм.	Кол.	Лист	№док	Подп.	Разрез 1-1	Стадия: ЭП; Лист: 11; Листов: 12
Разраб.		ИИ-ассист.		10.26		
Рук. пр.		Аюпов Р.		10.26		
ГАП				10.26	АР-11	М 1:100
Н. контр.				10.26		

Разрез 2-2

Продольный разрез через западные квартиры, вид на запад: консоли балконов юга и севера, мансарда под крутым скатом — линии высоты 1,6 и 2,5 м для проверки площади и кроватей.

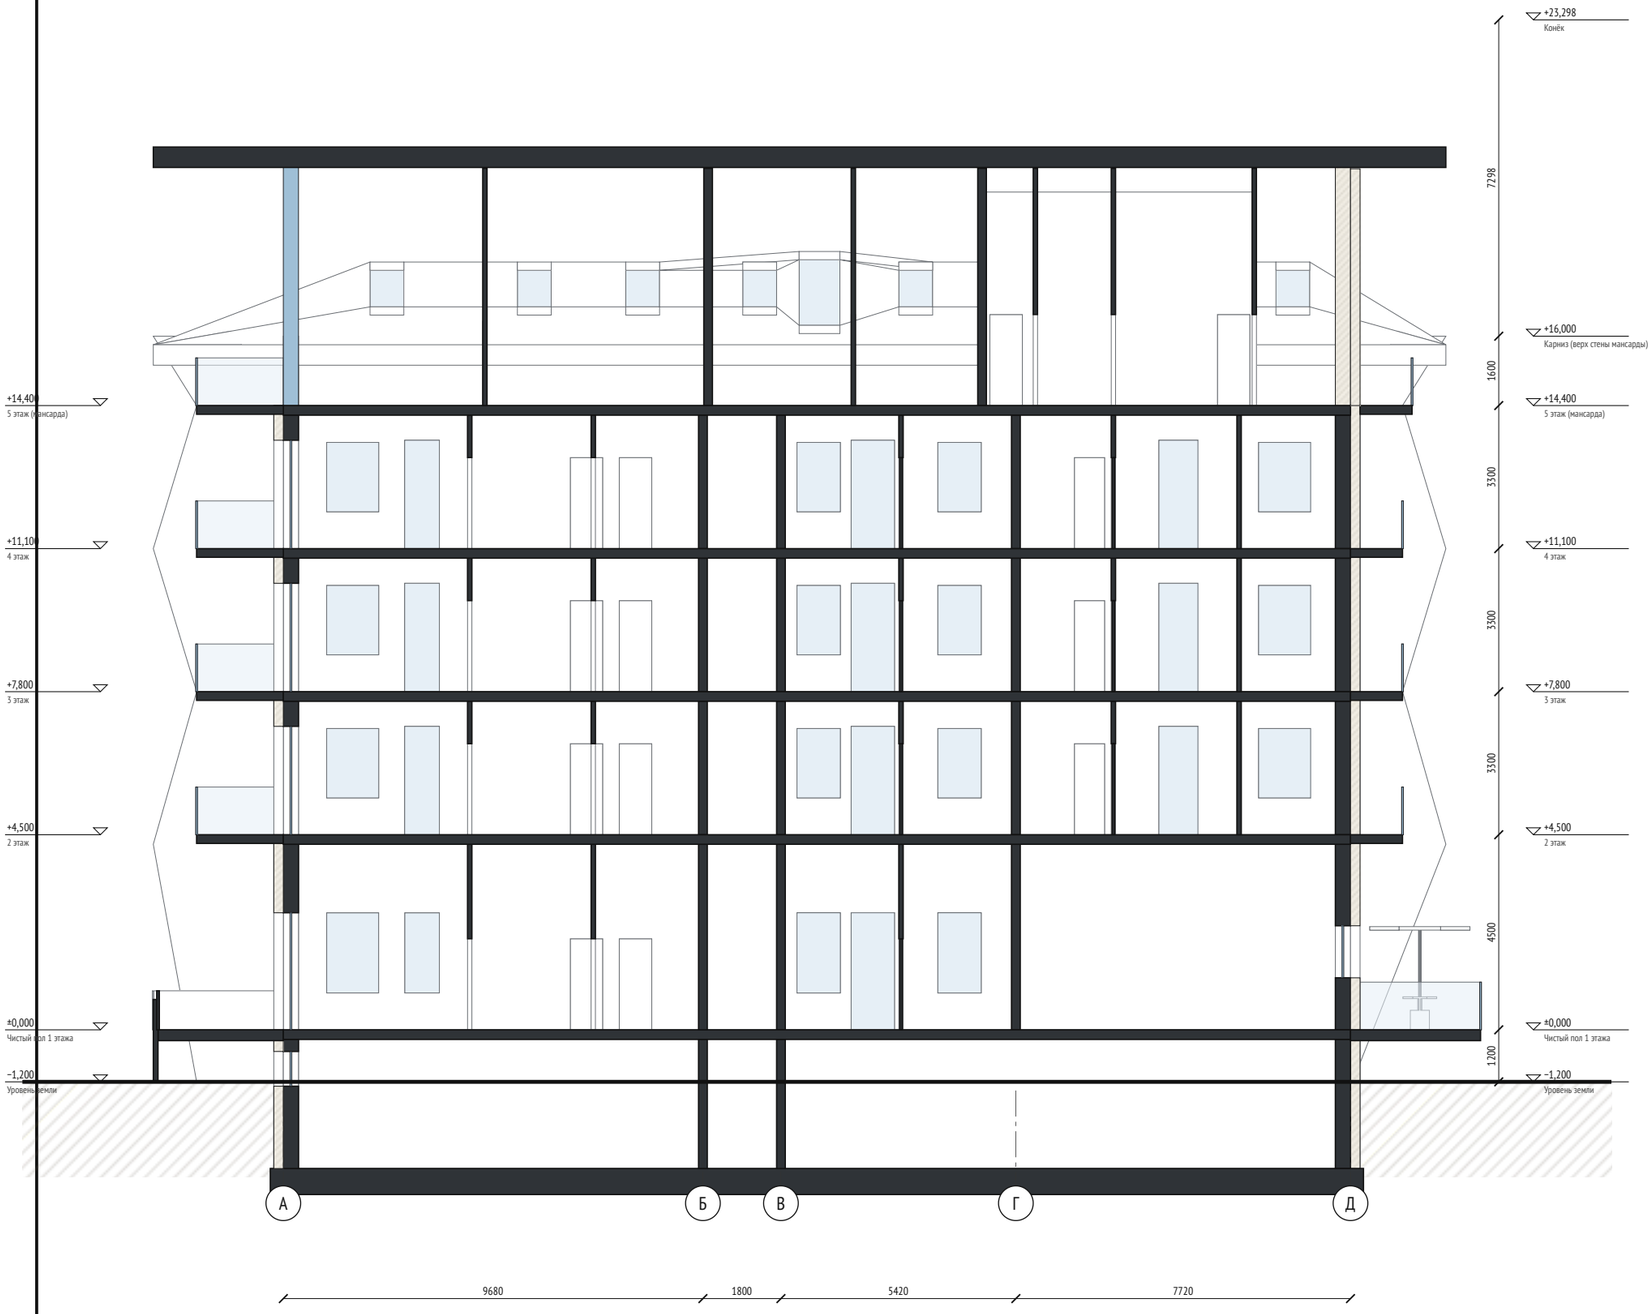

					ЖР-27 · Ала-Тоо Резорт, Жыргалан · АР	
					Апарт-резиденция «Family Active Residence», участок 27	
					Жилое здание 5 эт. (мансарда) с полуцоколем, 34 апартамента	
Изм.	Кол.	Лист	№док	Подп.	Разрез 2-2	Стадия: ЭП; Лист: 12; Листов: 12
Разраб.		ИИ-ассист.		10.26		
Рук. пр.		Аюпов Р.		10.26		
ГАП				10.26		
Н. контр.				10.26	АР-12	М 1:100