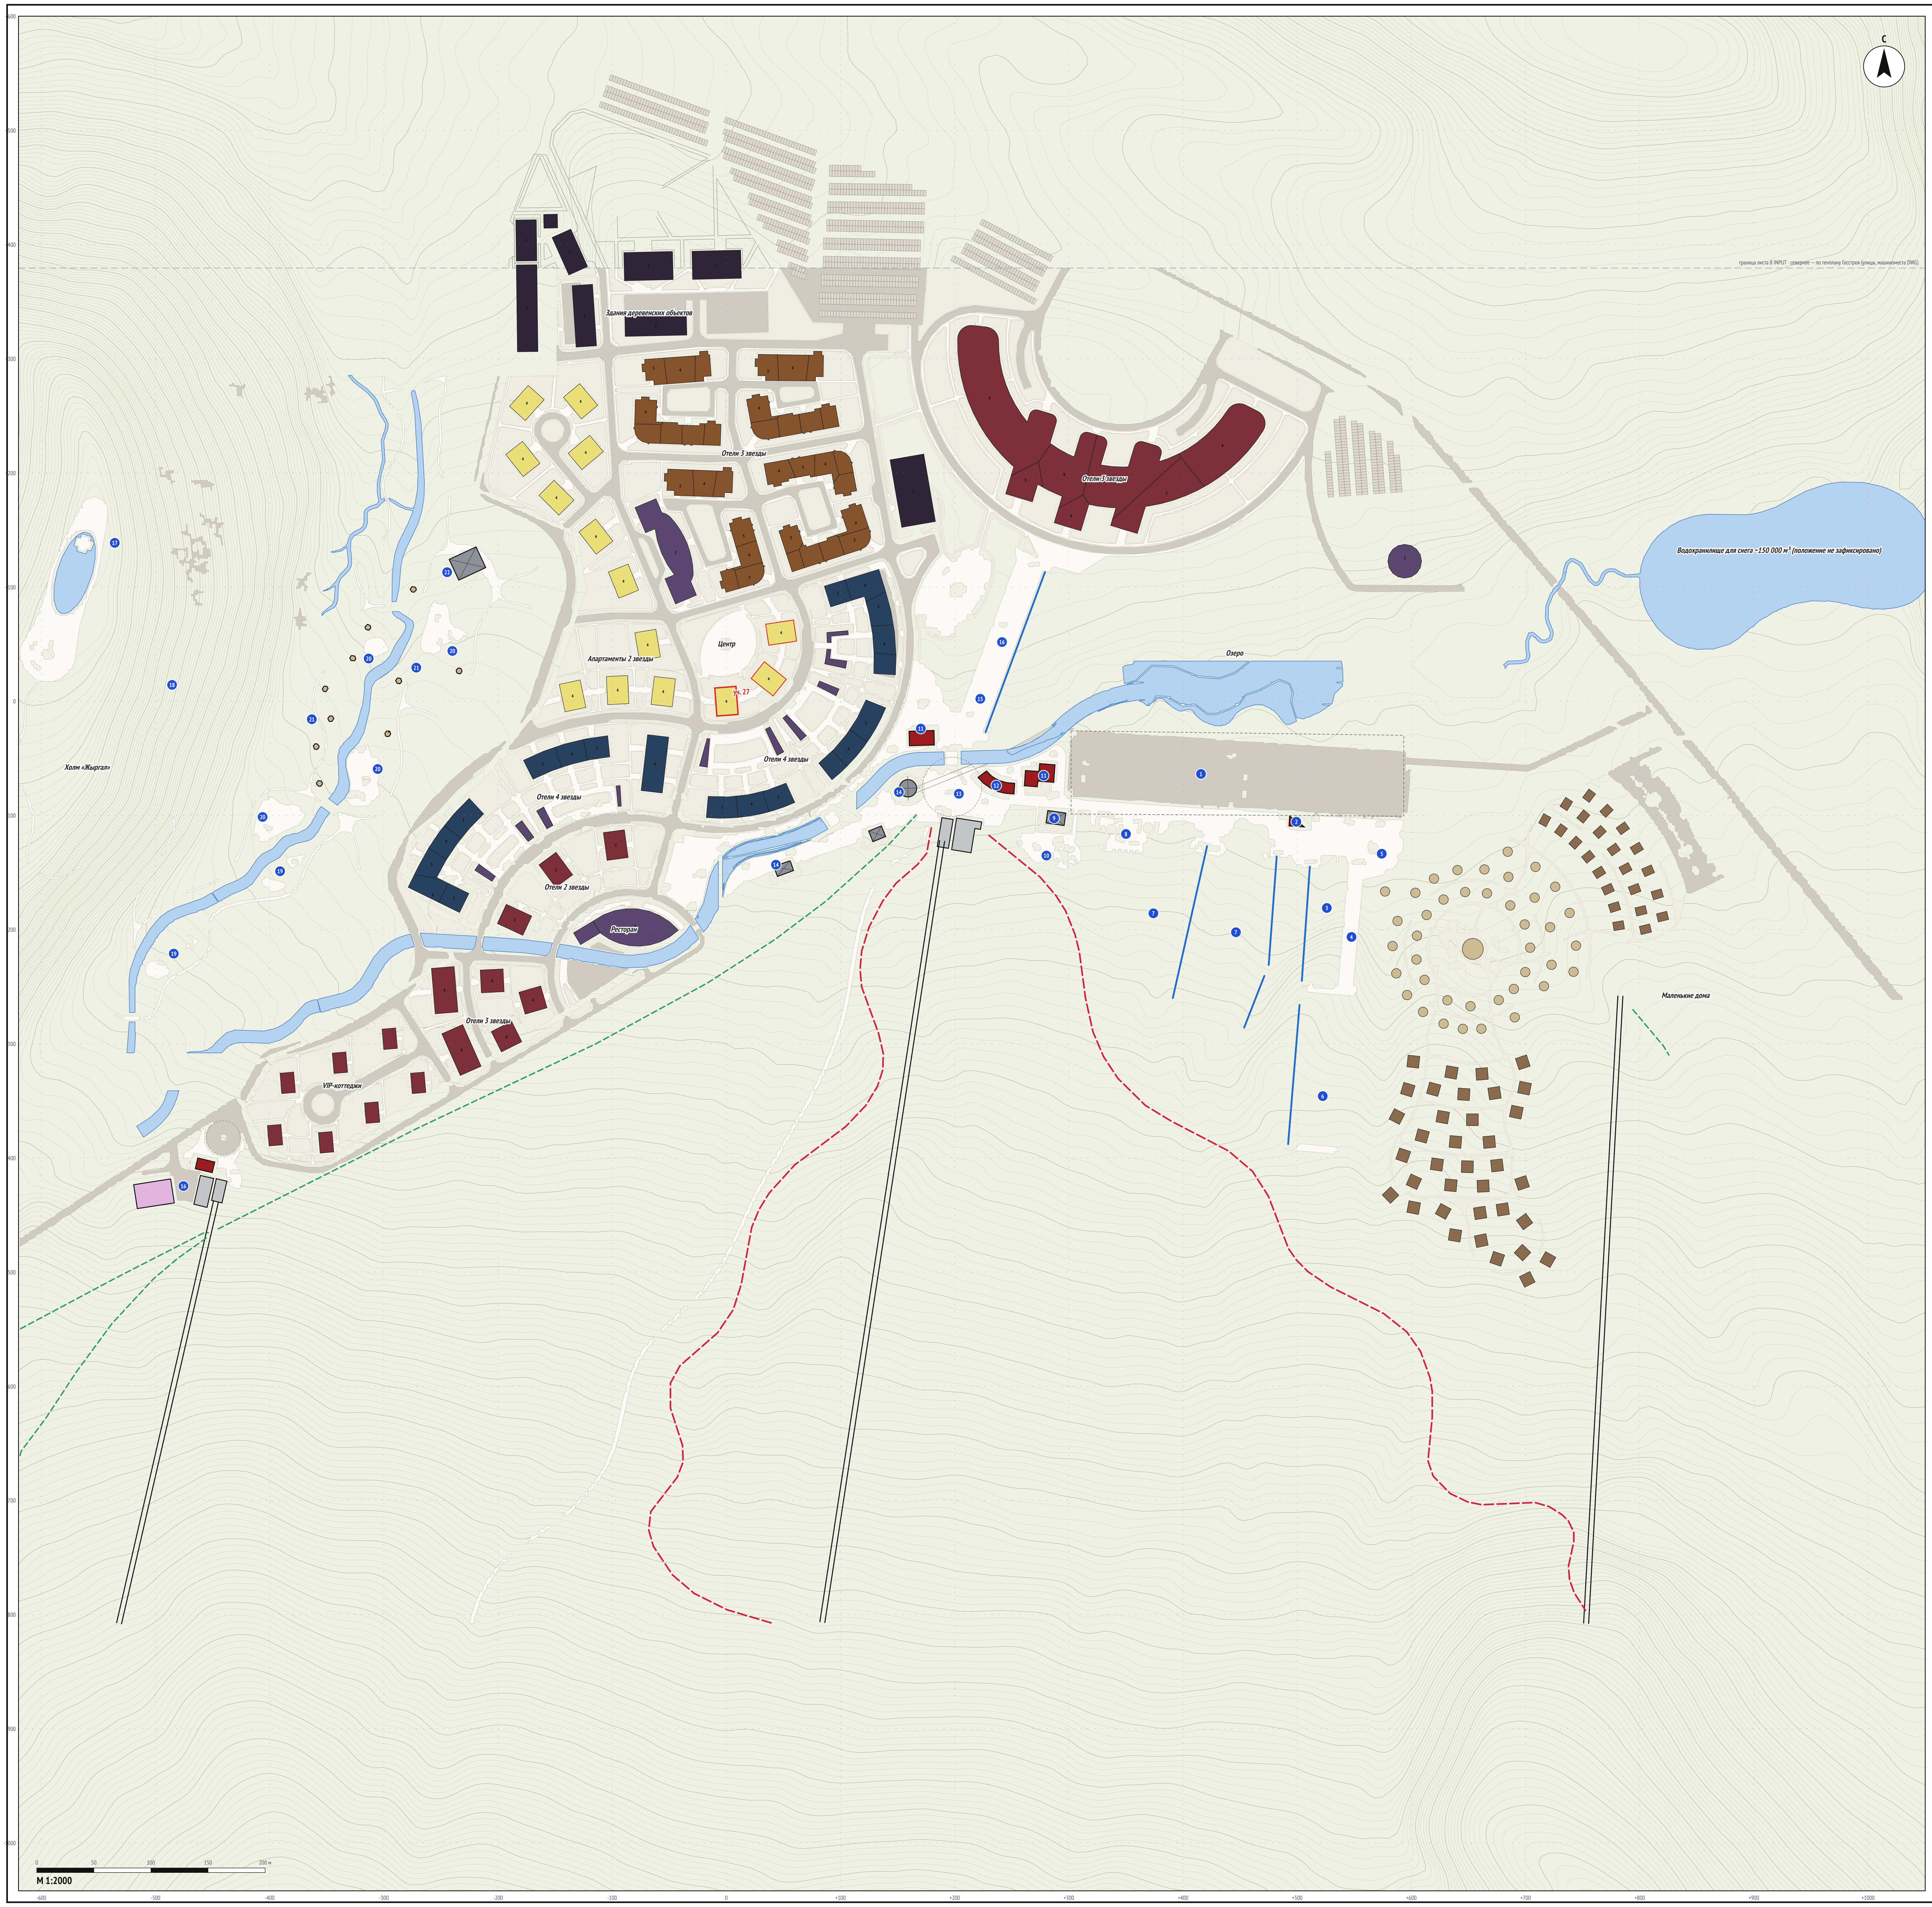

ГЕНЕРАЛЬНЫЙ ПЛАН ДЕРЕВНИ · КОНЦЕПЦИЯ INPUT

Вся деревня, нижняя зона курорта, М 1:2000

Перерисовка мастер-плана INPUT («Jyrgalan Conceptual Masterplans & Zooms», сентябрь 2025, листы 8–12) в координатах генплана Госстроя «1903 13-6» (DWG). Привязка листа 8 по зданиям генплана — совпадение 81 %, листы-увеличения 9–12 — по точкам; контроль: нижняя станция B1 совпадает с генпланом с точностью ~2 м.

Условные обозначения

Здания по генплану Госстроя

- ■ Проектируемые гостиничные комплексы 5*
- ■ Проектируемые гостиничные комплексы 4*
- ■ Проектируемые гостиничные комплексы 3*
- ■ Апартаменты (лоты 458 м²)
- ■ Общественные здания
- ■ Общежитие и хозяйственные сооружения
- ■ Глэмпинг: коттеджи
- ■ Глэмпинг: юрты

цифра в контуре — этажность по генплану

Предложения INPUT, которых нет на генплане

- ■ Центры приветствия, кассы, прокат и депо (INPUT)
- ■ Бистро, рестораны, апрес-ски (INPUT)
- ■ Нижние станции и гаражи канатных дорог (INPUT)
- ■ Главный технический центр, гаражи ратраков (INPUT)
- ■ Беседки «Оазис» для пикников (INPUT)

Покрытия и рельеф

- ■ Участки, газоны и мощение кварталов
- ■ Проезды и парковки
- □ Площади, тротуары и прогулочные дорожки
- ■ Канал, озеро и пруды (INPUT)
- ■ Луг, склоны; горизонтали через 1 м (утолщённые — через 5 м)
- — Участки 27, 28, 29 (консорциум)
- — Канатные дороги (B1, F, C)
- — Ковровые подъёмники, детский подъёмник, связь с 5*
- - - Велосипедные тропы 1, 2
- - - Конная тропа

Экспликация INPUT (номера на плане)

1. Парковка для дневных посетителей
2. Детская зона, центр приветствия
3. Летние и зимние тюбинги
4. Зимний спуск / контакт со снегом
5. Зона для игр со снегом
6. Зона для начинающих лыжников
7. Летняя и зимняя зона для начинающих
8. Памп-трек
9. Бистро / ресторан с террасой
10. Игровые площадки
11. Спортивное оборудование: магазин, аренда и депо
12. Продажа билетов, туалеты, школа лыж, администрация
13. Главная площадь
14. Бистро и апрес-ски
15. Связь с 5* отелем
16. Нижняя станция, центр приветствия и главный технический центр
17. Монумент на вершине холма «Эпос Манаса»
18. Знак «Джыргалан»
19. Игровые площадки для ловкости
20. Песочные площадки «Охота за сокровищами»
21. Оазис — места для пикников и барбекю
22. Ресторан «Оазис» с террасой

Примечания

1. Кварталы деревни у INPUT совпадают с генпланом Госстроя; INPUT подписывает категории иначе: «полумесяц» — «Отели 3 звезды» (на генплане — основная гостиница 5*, №1); кварталы юго-западнее площади №14 — «Отели 2 звезды» и «Отели 3 звезды» (на генплане — малые гостиницы 5*); виллы на юго-западе — «VIP-коттеджи». Цвета зданий на листе — по генплану Госстроя.
2. INPUT добавляет то, чего нет в генплане: канал от холма к озеру, базу B1 с главной площадью, центром приветствия, прокатом, бистро и апрес-ски; зону новичков с коврами и тюбингом; холм «Жыргал» с монументом, площадками и оазисами; станцию F с кольцом шаттла и техцентром.
3. Лыжная база и станция подъёмника генплана не показаны: на их месте — постройки INPUT.
4. Севернее пунктира листы INPUT ничего не показывают: там улицы и машиноместа генплана Госстроя — северная парковка ~1 200 мест и парковка у мечети ~200 мест по разметке DWG.
5. Координаты сетки — локальные, м: 0;0 — центр участка 27; E = x + 332 968,5; N = y + 4 720 510,3 (UTM 44N).
6. Рельеф — топосъёмка генплана и Copernicus GLO-30. Лист 13 INPUT (станция H) за пределами деревни, не показан.

					Ала-Тоо Резорт · Жыргалан · деревня всесезонного курорта Генеральный план: концепция INPUT в координатах генплана			
					Исходная концепция для сравнения с предложением консорциума			
Изм.	Кол.	Лист	№док	Подп. Дата		Стадия	Лист	Листов
Разраб.		ИИ-ассист.		10.26	**ГЕНЕРАЛЬНЫЙ ПЛАН ДЕРЕВНИ** Вся деревня, нижняя зона курорта, М 1:2000	**Конц.**	**1**	**2**
Рук. пр.		Аюпов Р.		10.26				
ГАП				10.26	**ГП-1**	**М 1:2000**		
Н. контр.				10.26				

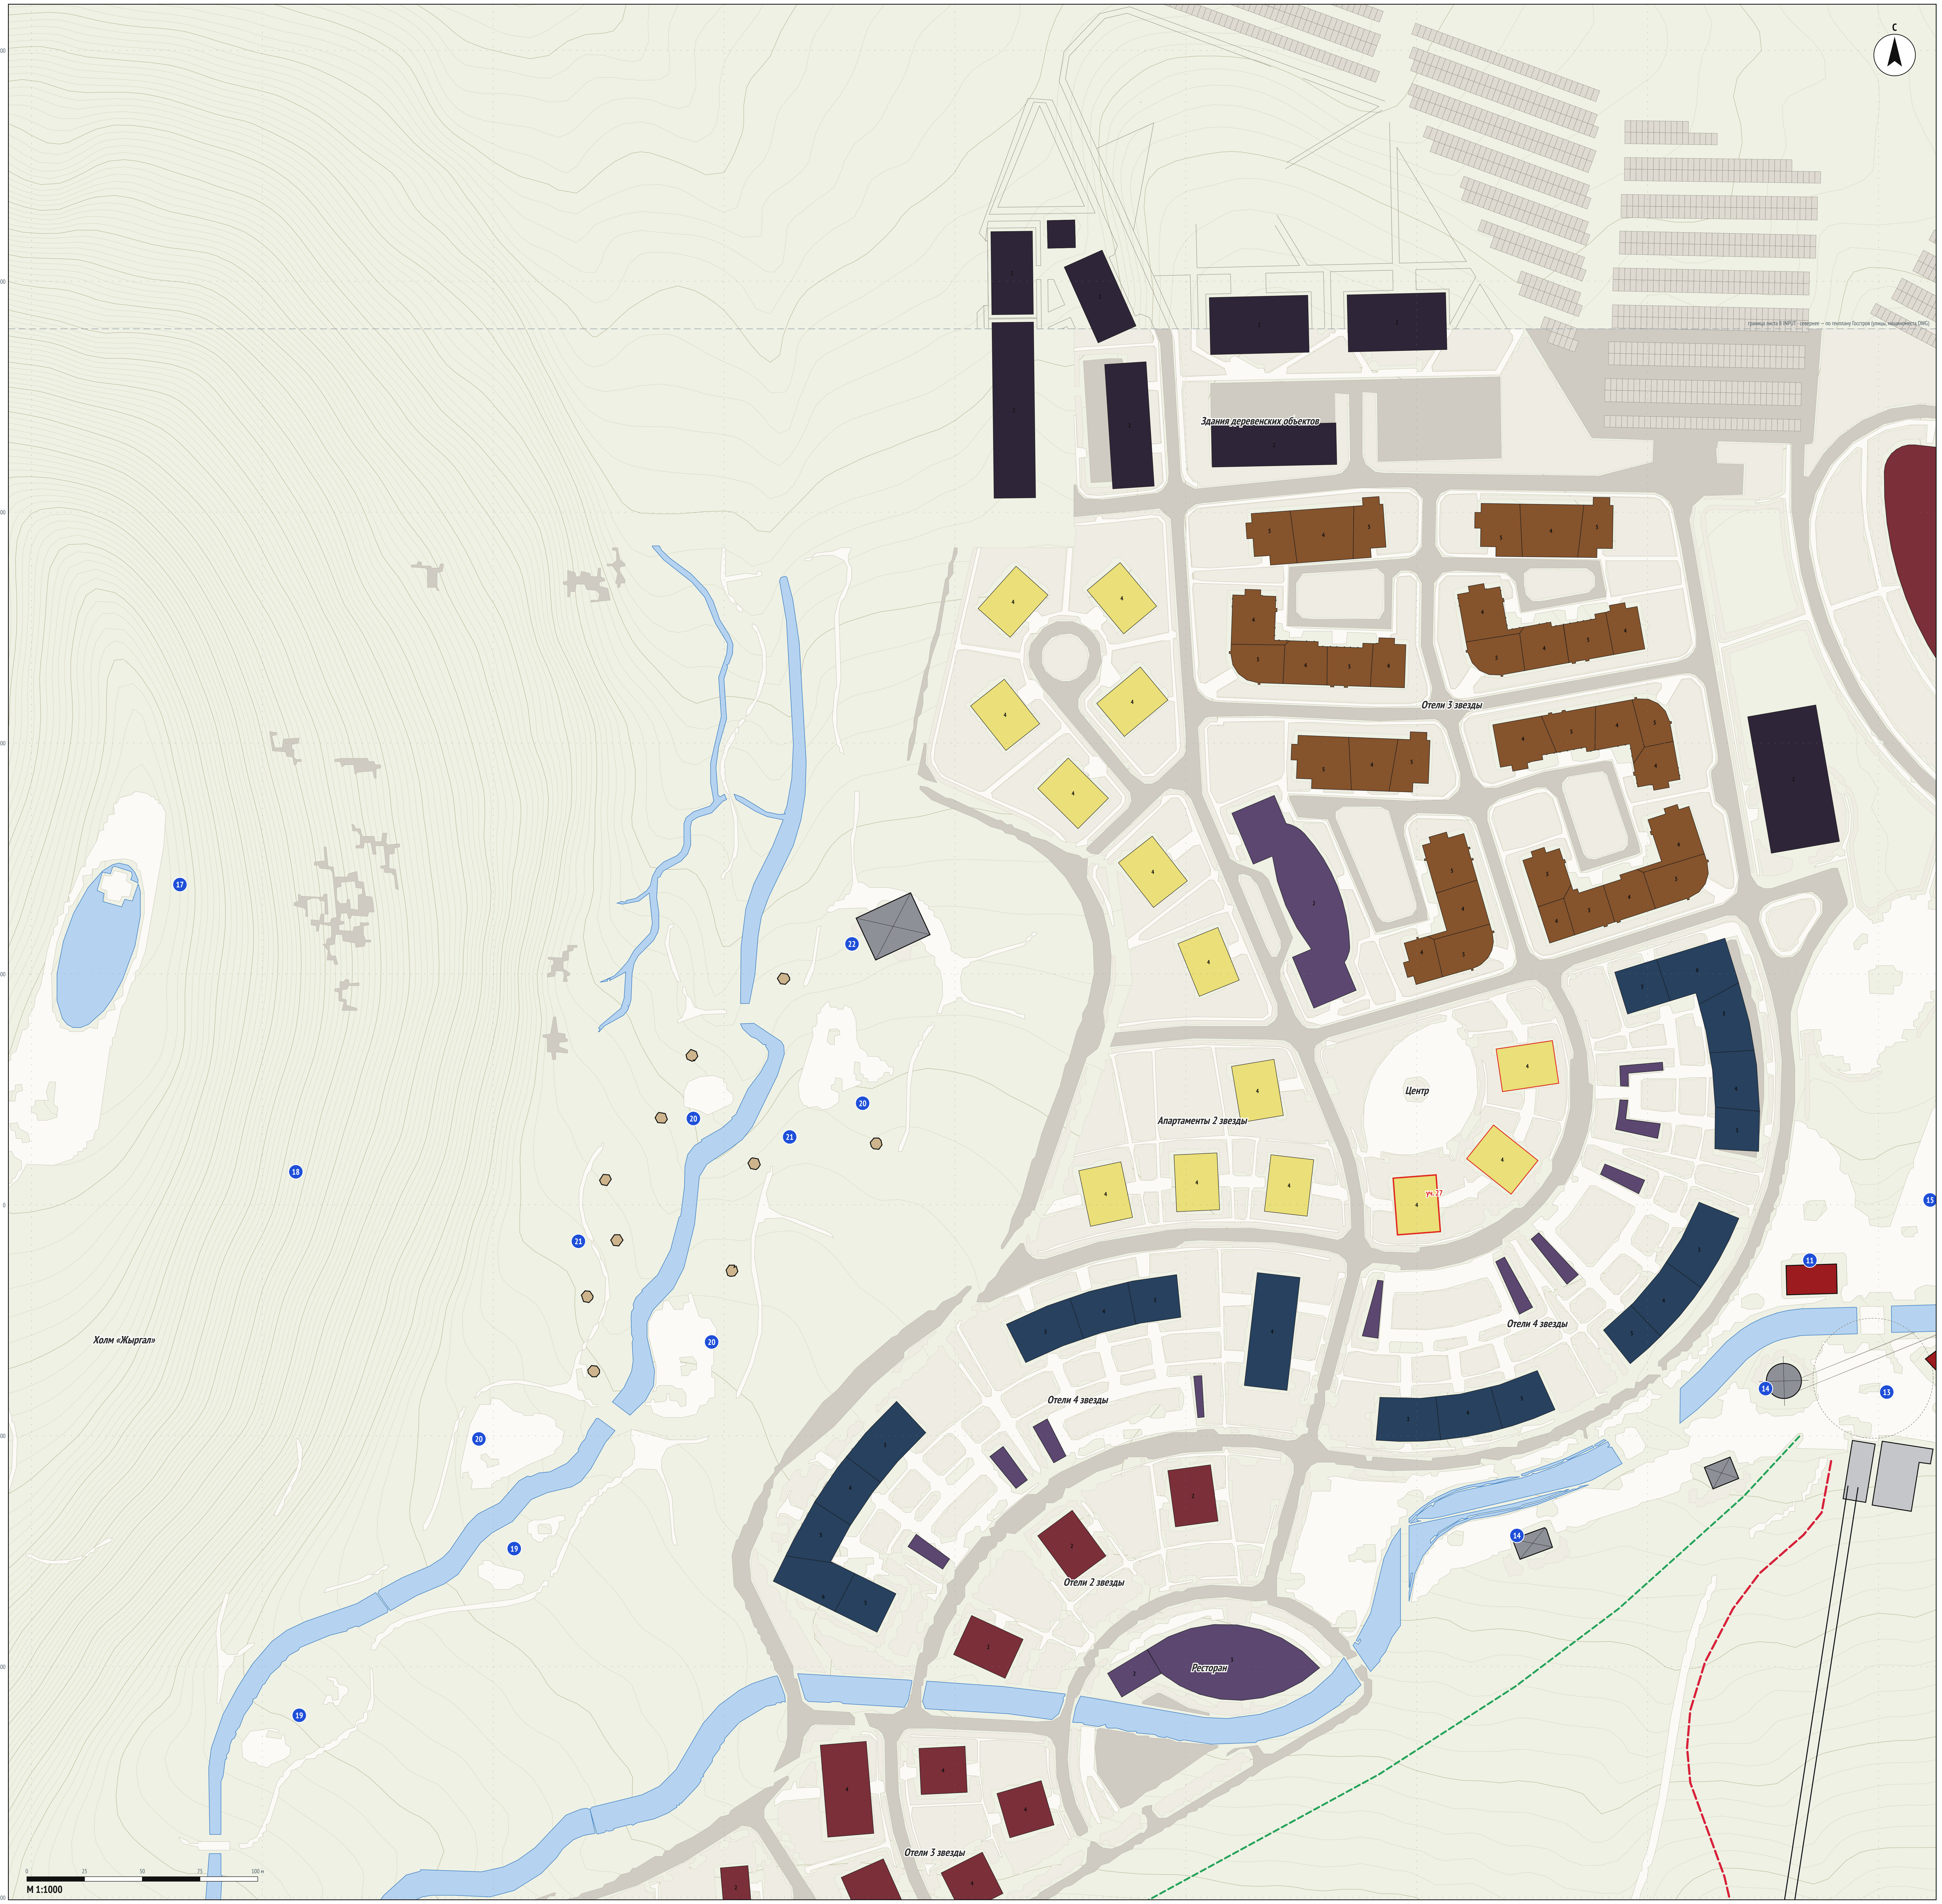

СЕВЕРО-ЗАПАДНАЯ ЗОНА И БАЗА B1 · КОНЦЕПЦИЯ INPUT

Фрагмент: холм «Жыргал», площадь №14, база B1, М 1:1000

Перерисовка мастер-плана INPUT («Jyrgalan Conceptual Masterplans & Zooms», сентябрь 2025, листы 8–12)
в координатах генплана Госстроя «1903 13-6» (DWG). Привязка листа 8 по зданиям генплана — совпадение 81 %,
листы-увеличения 9–12 — по точкам; контроль: нижняя станция B1 совпадает с генпланом с точностью ~2 м.

Условные обозначения

Здания по генплану Госстроя

🟥	Проектируемые гостиничные комплексы 5*
🟦	Проектируемые гостиничные комплексы 4*
🟫	Проектируемые гостиничные комплексы 3*
🟨	Апартаменты (лоты 458 м²)
🟪	Общественные здания
⬛	Общежитие и хозяйственные сооружения
🟫	Глэмпинг: коттеджи
🟫	Глэмпинг: юрты

цифра в контуре — этажность по генплану

Предложения INPUT, которых нет на генплане

🟥	Центры приветствия, кассы, прокат и депо (INPUT)
⬛	Бистро, рестораны, апрес-ски (INPUT)
⬜	Нижние станции и гаражи канатных дорог (INPUT)
🟪	Главный технический центр, гаражи ратраков (INPUT)
🟫	Беседки «Оазис» для пикников (INPUT)

Покрытия и рельеф

⬜	Участки, газоны и мощение кварталов
⬜	Проезды и парковки
⬜	Площади, тротуары и прогулочные дорожки
🟦	Канал, озеро и пруды (INPUT)
⬜	Луг, склоны; горизонтали через 1 м (утолщённые — через 5 м)
—	Участки 27, 28, 29 (консорциум)
—	Канатные дороги (B1, F, C)
—	Ковровые подъёмники, детский подъёмник, связь с 5*
– –	Велосипедные тропы 1, 2
– – ·	Конная тропа

Экспликация INPUT (номера на плане)

1	Парковка для дневных посетителей
2	Детская зона, центр приветствия
3	Летние и зимние тюбинги
4	Зимний спуск / контакт со снегом
5	Зона для игр со снегом
6	Зона для начинающих лыжников
7	Летняя и зимняя зона для начинающих
8	Памп-трек
9	Бистро / ресторан с террасой
10	Игровые площадки
11	Спортивное оборудование: магазин, аренда и депо
12	Продажа билетов, туалеты, школа лыж, администрация
13	Главная площадь
14	Бистро и апрес-ски
15	Связь с 5* отелем
16	Нижняя станция, центр приветствия и главный технический центр
17	Монумент на вершине холма «Эпос Манаса»
18	Знак «Джыргалан»
19	Игровые площадки для ловкости
20	Песочные площадки «Охота за сокровищами»
21	Оазис — места для пикников и барбекю
22	Ресторан «Оазис» с террасой

Примечания

1. Кварталы деревни у INPUT совпадают с генпланом Госстроя; INPUT подписывает категории иначе: «полумесяц» — «Отели 3 звезды» (на генплане — основная гостиница 5*, №1); кварталы юго-западнее площади №14 — «Отели 2 звезды» и «Отели 3 звезды» (на генплане — малые гостиницы 5*); виллы на юго-западе — «VIP-коттеджи». Цвета зданий на листе — по генплану Госстроя.
2. INPUT добавляет то, чего нет в генплане: канал от холма к озеру, базу B1 с главной площадью, центром приветствия, прокатом, бистро и апрес-ски; зону новичков с коврами и тюбингом; холм «Жыргал» с монументом, площадками и оазисами; станцию F с кольцом шаттла и техцентром.
3. Лыжная база и станция подъёмника генплана не показаны: на их месте — постройки INPUT.
4. Севернее пунктира листы INPUT ничего не показывают: там улицы и машиноместа генплана Госстроя — северная парковка ~1 200 мест и парковка у мечети ~200 мест по разметке DWG.
5. Координаты сетки — локальные, м: 0;0 — центр участка 27; E = x + 332 968,5; N = y + 4 720 510,3 (UTM 44N).
6. Рельеф — топосъёмка генплана и Copernicus GLO-30. Лист 13 INPUT (станция H) за пределами деревни, не показан.

Изм.	Кол.	Лист	№док	Подп. Дата	
Разраб.		ИИ-ассист.		10.26	
Рук. пр.		Аюпов Р.		10.26	
ГАП				10.26	
Н. контр.				10.26	

Ала-Тоо Резорт · Жыргалан · деревня всесезонного курорта
Генеральный план: концепция INPUT в координатах генплана

Исходная концепция для сравнения с предложением консорциума

СЕВЕРО-ЗАПАДНАЯ ЗОНА И БАЗА B1
Фрагмент: холм «Жыргал», площадь №14, база B1, М 1:1000

Стадия	Лист	Листов
Конц.	**2**	**2**

ГП-2

М 1:1000