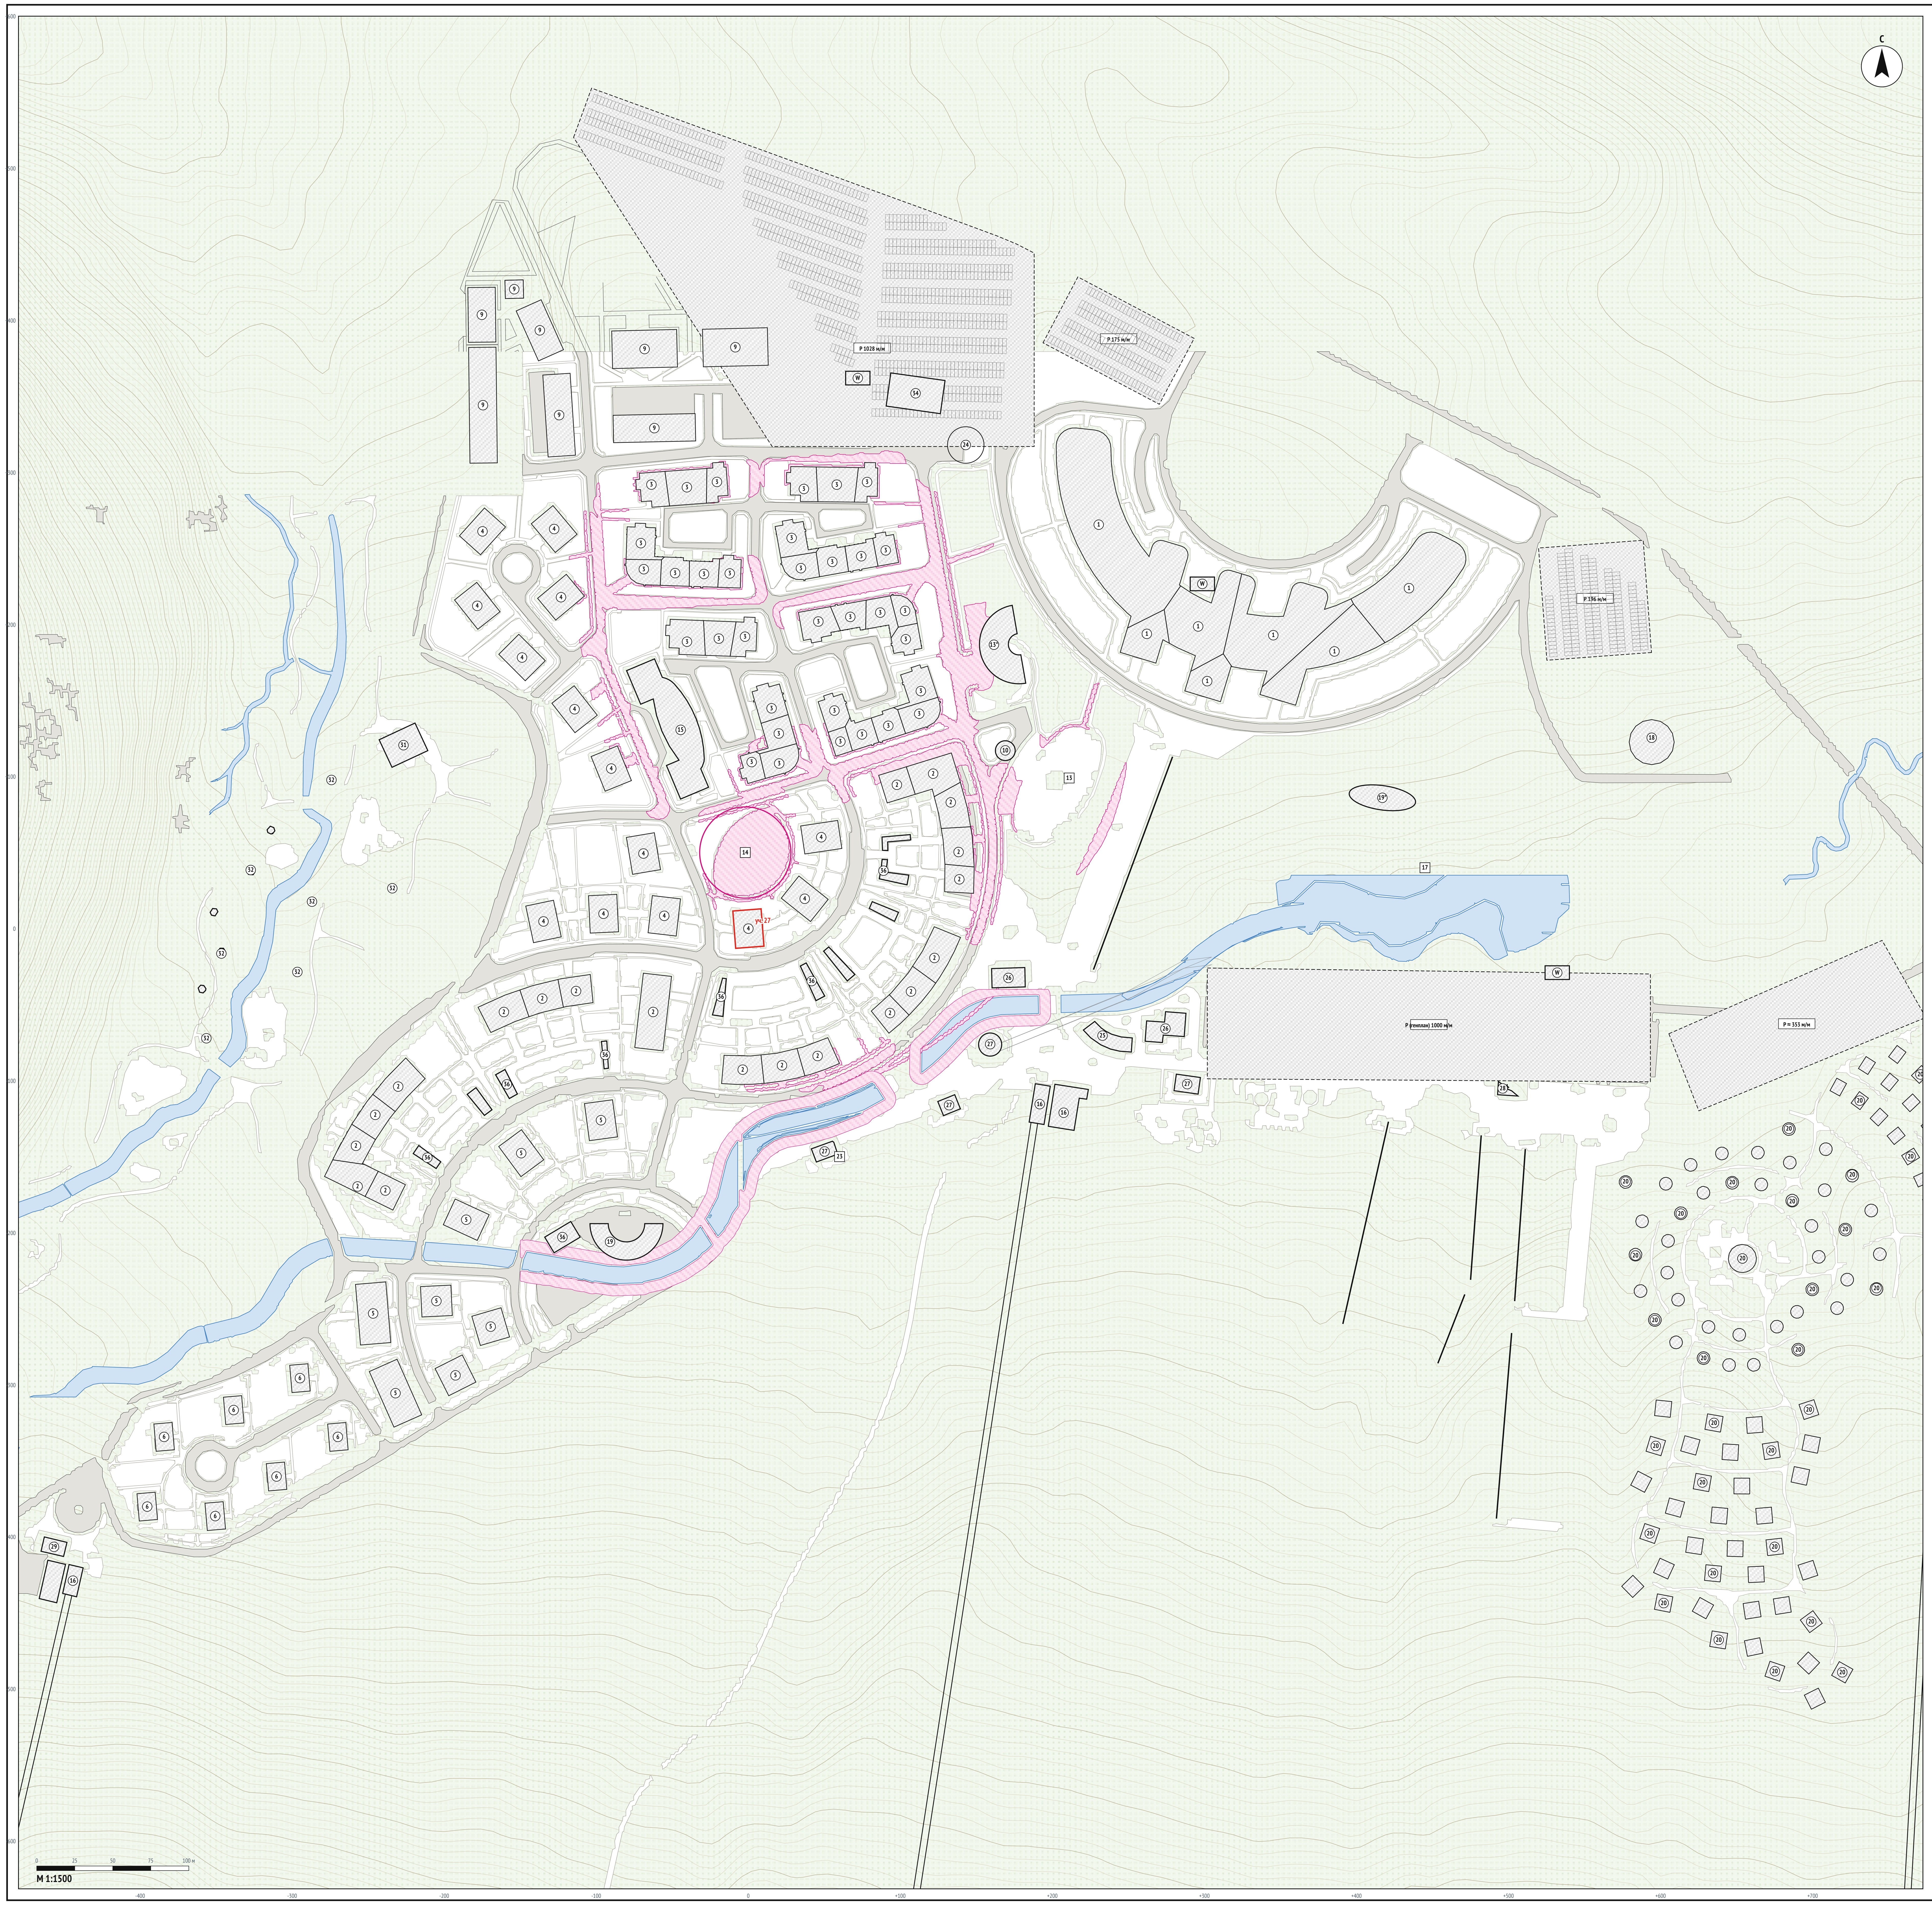

ГЕНЕРАЛЬНЫЙ ПЛАН ДЕРЕВНИ · ПРЕДЛОЖЕНИЕ

Чертёж по ГОСТ 21.508, стадия концепции, М 1:1500

Экспликация зданий и сооружений

№	Наименование	Этажн.	Кол-во	Пл. застр., м²	Источник
1	Основная гостиница 5*	4–6	7	15 661	генплан
2	Гостиницы 4*	3–6	20	9 712	генплан
3	Гостиницы 3*	4–5	34	12 575	генплан
4	Апартаменты. Гостиницы 2*	4	14	6 425	генплан
5	Гостиницы 5*	2–4	8	4 177	генплан
6	VIP-коттеджи	2	7	1 513	генплан
9	Здания для персонала, хозяйственные	2	9	7 008	генплан
10	Прокат, продажа и ремонт снаряжения	1	1	133	предложение
11	Административные и общественные здания	2	1	236	генплан
13*	Концертная площадка	1	1	984	предложение
15	КДЦ: кинотеатр, технопарк, зал	1	1	1 997	предложение
16	Нижние станции и гаражи канатных дорог B1, F	1	4	1 260	INPUT
18	Мечеть	2	1	672	генплан
19	Велнес-зона с рестораном	1	1	678	предложение
19*	Велнес у озера	1	1	553	предложение
20	Юрточный городок, глэмпинг	1	100	7 856	генплан
24	Стела «Жыргалан» на въездном кольце	1	1	4	предложение
25	Центр приветствия B1: кассы, школа, администрация	1	1	299	INPUT
26	Магазин, аренда и депо снаряжения	1	2	644	INPUT
27	Бистро, апрес-ски	1	4	617	INPUT
28	Детская зона, центр приветствия	1	1	60	INPUT
29	Центр приёма гостей F	1	1	147	INPUT
30	Главный технический центр, гаражи ратраков	1	1	694	INPUT
31	Ресторан «Оазис»	1	1	520	INPUT
32	Беседки «Оазис» для пикников	1	10	182	INPUT
34	Пункт прибытия: заселение, лаунж, багаж, душевые, прокат, кафе	2	1	792	путь гостя
36	Павильоны променада: кофейня, стритфуд, сервис, ремёсла	1	16	1 996	предложение
W	Welcome-павильоны	1	4	576	предложение
12	Гостевые автостоянки (число мест — на плане)				генплан
13	Открытый каток				генплан
14	Событийная площадь с ёлкой (бывшая концертная №14)				предложение
17	Искусственный пруд, озеро				генплан
23	Благоустроенная набережная				предложение
35	Лыжехранилище у станции B1 (в составе 25)				предложение

Технико-экономические показатели

Курортный посёлок (зона)	**24.3 га**
Территория отеля 5*	**7.0 га**
Парк-отель	**16.4 га**
Административно-хозяйственная зона	**3.7 га**
Площадь застройки (все здания на плане)	**77 971 м²**
Торговый променад / квартал	**2.21 га**
Благоустроенная набережная	**≈ 324 м по каналу**
Гостевые автостоянки, всего	**≈ 2 939 м/м**
Пешком от Пункта прибытия до площади 14 / уч. 27 / B1	**410 / 447 / 544 м**
Ось деревни (стела ⟶ площадь ⟶ B1)	**шаттл, доставка, экстренные службы**

Условные обозначения

▨	Проектируемые здания; в кружке — номер по экспликации, этажность — в таблице
🟪	Торговый променад / квартал, набережная (предложение)
▨	Проезды; ось деревни — только шаттл, доставка, экстренные службы
☐	Тротуары, площади, участки
⬚	Гостевые автостоянки с числом мест
🟩	Озеленение, луг; горизонтали через 1 м
🟦	Канал, пруды, озеро

1. Основа — генплан Госстроя «1903 13-6» (DWG), концепция INPUT (сентябрь 2025) и «Жыргалан 2.0» (апрель 2026).
2. Ресторан-«линза» генплана заменён велнес-зоной 19 с рестораном; здание №19 (ресторан, фитнес, спа) – КДЦ 15.
3. Лыжная база и станция генплана заменены базой B1 по INPUT (25–28, 16).
4. Парковки 1 030, 175 и 200 м/м — по разметке DWG; новые у глэмпинга — оценка по площади (25 м² на место).
5. Координаты сетки — локальные, м: 0;0 — центр уч. 27; E = x + 332 968,5; N = y + 4 720 510,3 (UTM 44N).

					Ала-Тоо Резорт · Жыргалан · деревня всесезонного курорта Предложение консорциума по развитию курортной среды
					на основе генплана «1903 13-6», концепции INPUT и «Жыргалан 2.0»
Изм.	Кол.	Лист	№док	Подп. Дата	
Разраб.		ИИ-ассист.		10.26	**Генеральный план. Предложение** Чертёж, экспликация, ТЭП, М 1:1500
Рук. пр.		Аюпов Р.		10.26	
ГАП				10.26	**ГП-1**
Н. контр.				10.26	

Стадия	Лист	Листов
Конц.	**1**	**2**

М 1:1500

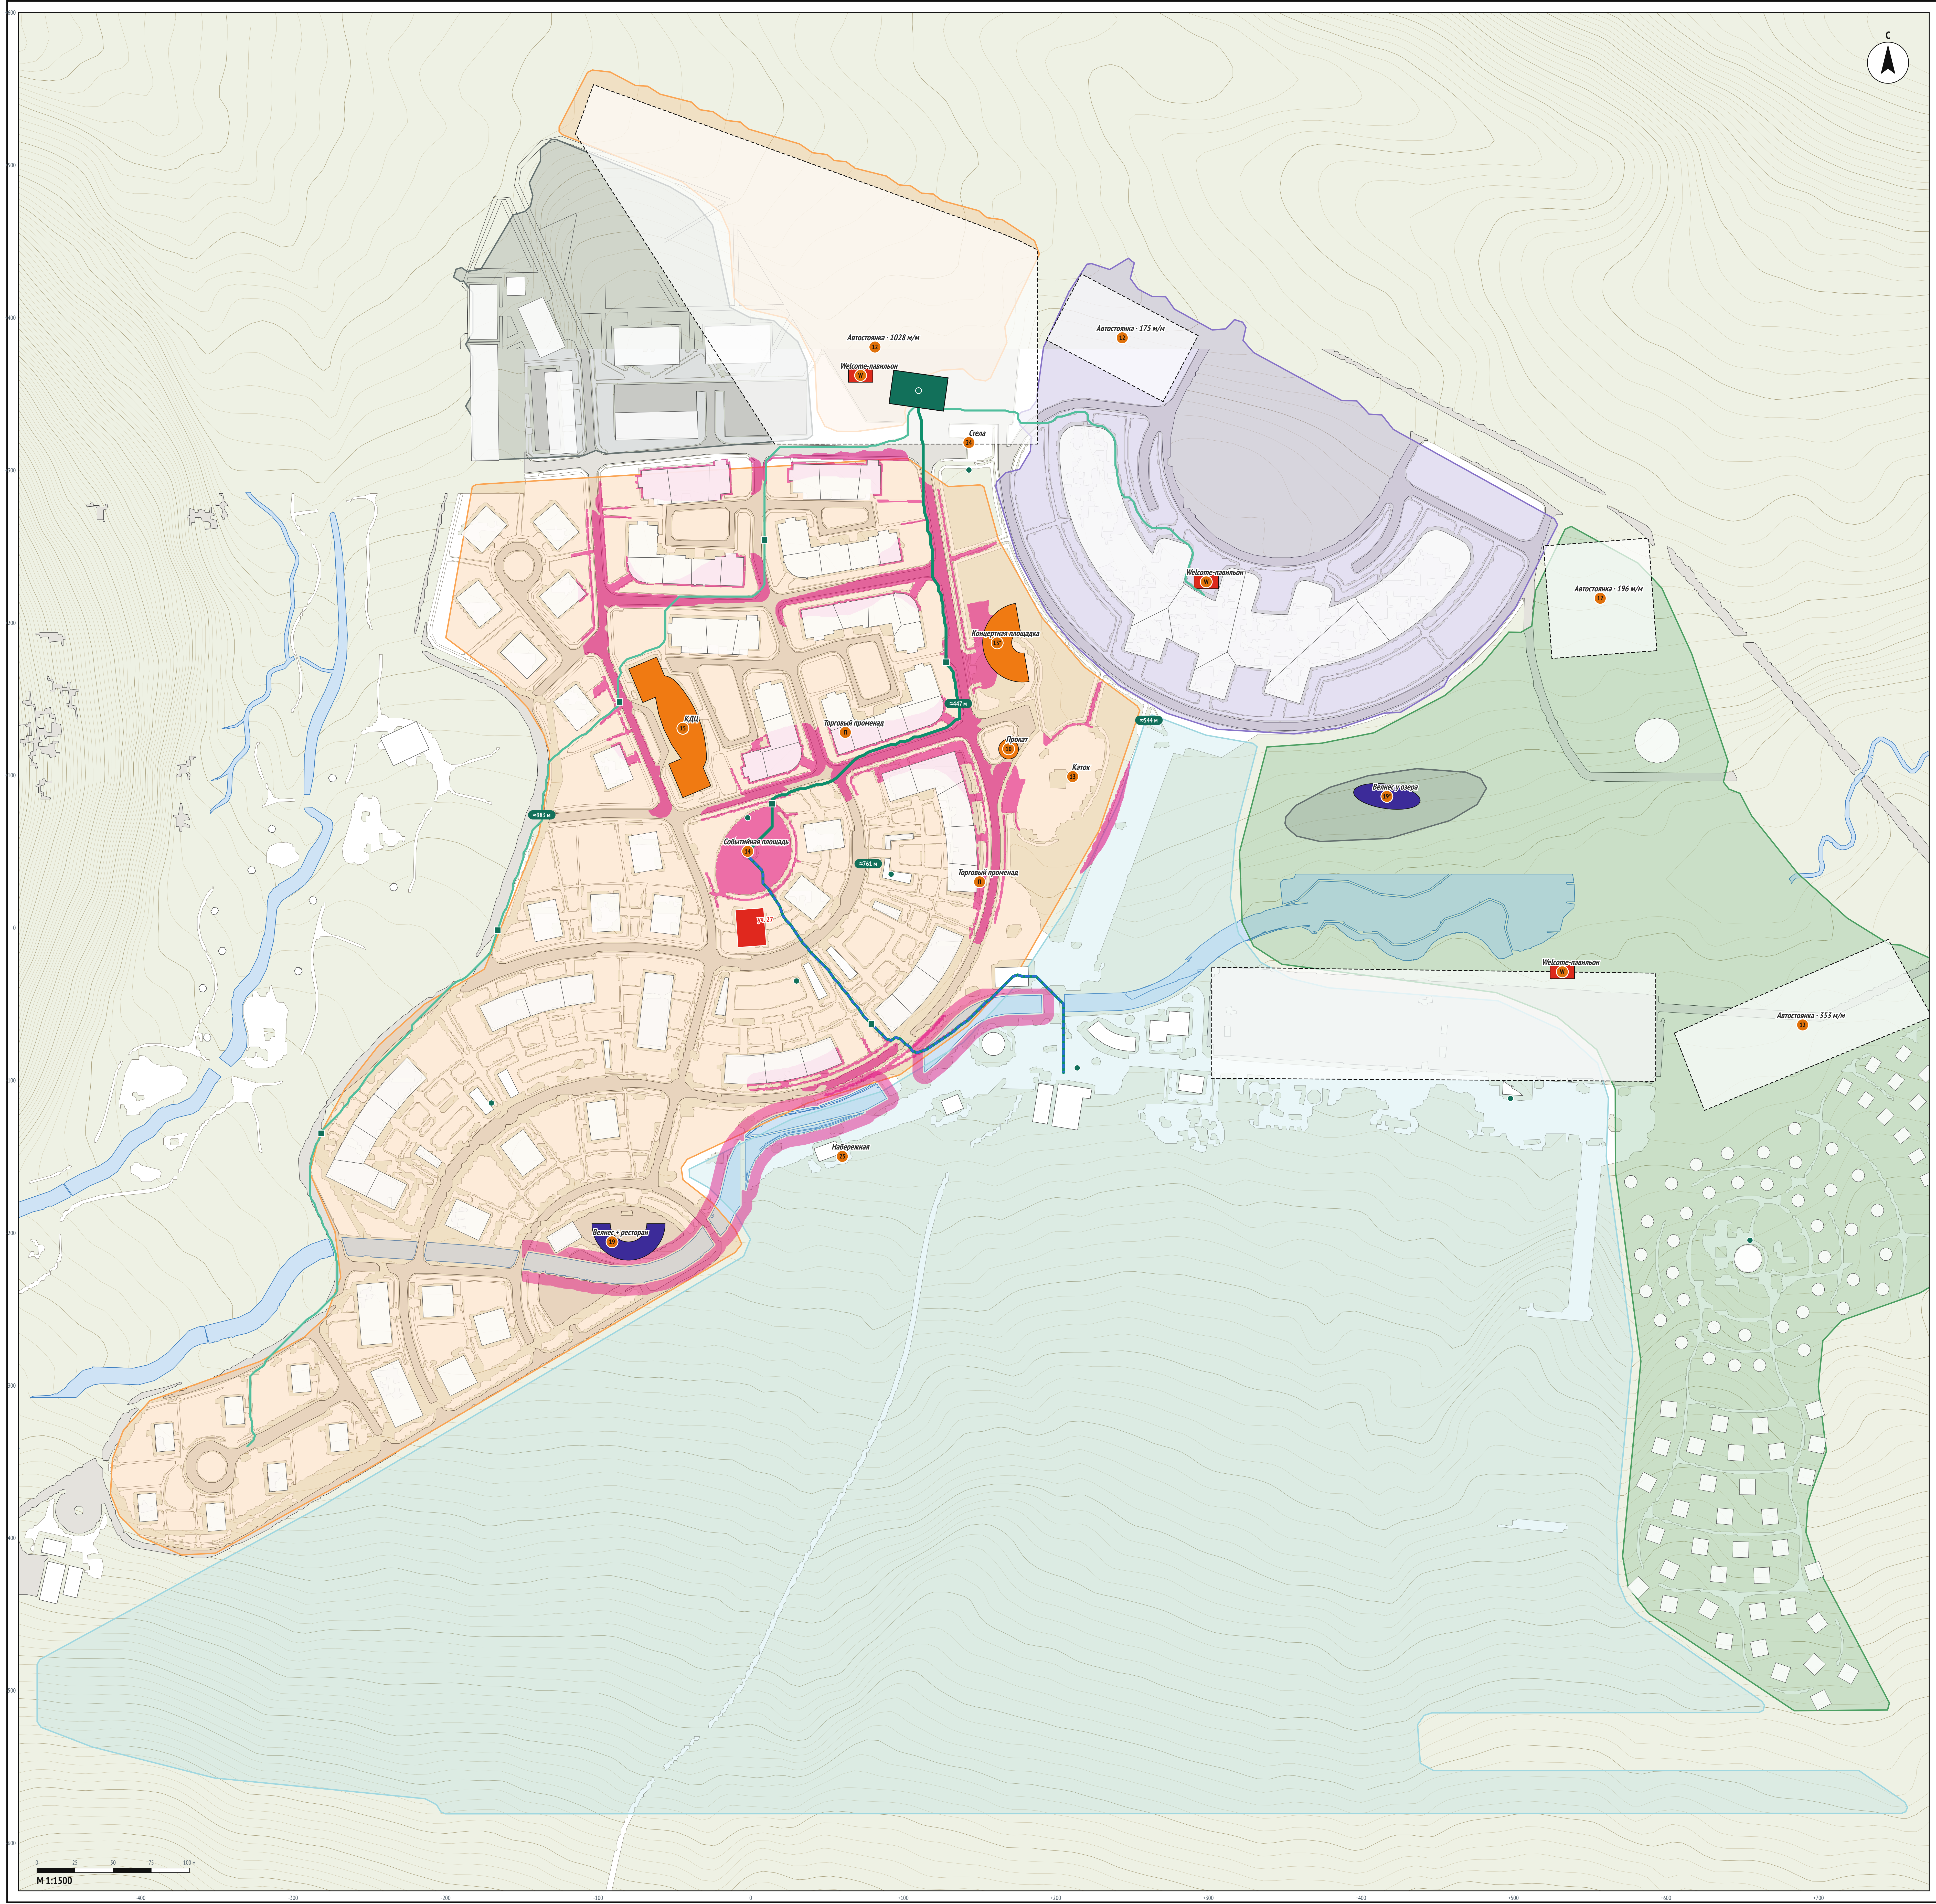
С
Автостоянка · 1028 м/м
12
Welcome-павильон
W
Стела
24
Автостоянка · 175 м/м
12
Welcome-павильон
W
Концертная площадка
13*
КДЦ
15
Торговый променад
П
≈447 м
Прокат
10
Каток
13
≈544 м
Событийная площадь
14
≈761 м
Торговый променад
П
уч. 27
≈985 м
Набережная
23
Велнес + ресторан
19
Автостоянка · 196 м/м
12
Велнес у озера
19*
Welcome-павильон
W
Автостоянка · 353 м/м
12
0
25
50
75
100 м
М 1:1500
-400
-300
-200
-100
0
+100
+200
+300
+400
+500
+600
+700

СХЕМА ПРЕДЛОЖЕНИЯ · ДЕРЕВНЯ ЖЫРГАЛАН

Зонирование, променад, магистрали, путь гостя · М 1:1500

Функциональное зонирование

- ▭ Курортный посёлок
- ▭ Отель 5*
- ▭ Парк-отель
- ▭ Горный массив
- ▭ Административно-хозяйственная зона

Структура «Жыргалан 2.0»

- ■ Торговый променад — улицы квартала по генплану; набережная 23
- 🟥 Welcome-павильоны (W)
- 🟧 КДЦ 15, концертная площадка 13*, прокат 10
- ■ Велнес 19 (с рестораном) и 19*
- 🟩 Стела 24 на въездном кольце

Путь гостя (консорциум)

- 🟩 Пункт прибытия у стелы: заселение, лаунж, багаж, прокат
- — Шаттл по оси: стела → площадь 14 → набережная → В1
- — Электрокары: к велнесу 19 и виллам, к «полумесяцу»
- — Лыжная улица: площадь 14 → В1
- 🟩 Тёплые остановки (квадрат), сервисы (точка)

Объекты предложения

- 24 Стела «Жыргалан» на въездном кольце
- П Торговый променад / квартал — мощение улиц внутри квартала; ось деревни — только шаттл, доставка, экстренные службы
- 14 Событийная площадь с ёлкой (бывшая концертная №14)
- 15 КДЦ: кинотеатр, технопарк, зал (в контуре здания №19)
- 13* Концертная площадка — амфитеатр со сценой
- 13 Открытый каток
- 10 Прокат, продажа и ремонт снаряжения
- 19 Велнес-зона с рестораном (вместо ресторана-«линзы»)
- 19* Велнес у озера
- 23 Благоустроенная набережная вдоль канала
- W Welcome-павильоны: у стелы, у «полумесяца», у озера, на восточном въезде
- 12 Гостевые автостоянки: 3 по генплану и 2 новые (у глэмпинга, у восточного въезда)

Путь гостя: 10 точек

1. Дорога: сообщения за 48 и за 3 часа, трансфер из Бишкека и Алматы, предзаказ ски-пасса и проката
2. Въезд: стела и кольцо 24 — первая точка, указатели «Прибытие» / «Дневные лыжники — к базе В1» / «Служебный въезд»
3. Парковка: северная стоянка, высадка на кольце, багаж принимает служба и везёт в номер
4. Пункт прибытия: заселение у стойки или терминала, ключ в телефон, лаунж и душ, если номер не готов
5. Пока номер не готов: прокат и катание, обед, прогулка по променаду, каток, спа
6. Первое утро: шаттл к базе В1 каждые 10–15 минут, прокат по предзаказу, «3 урока» для новичков
7. К подъёмнику: лыжная улица от площади 14, тёплые остановки каждые ~180 м, лыжехранилище у станции
8. Некатающимся: детский клуб, велнес 19 и 19*, юрта с национальной кухней, КДЦ
9. Вечер: торговый променад, событийная площадь с ёлкой, концерты на 13*, рестораны
10. Выезд: лаунж и душ после катания, багаж к машине на кольце высадки

Шумовые зоны (слайд 6 «Жыргалан 2.0»)

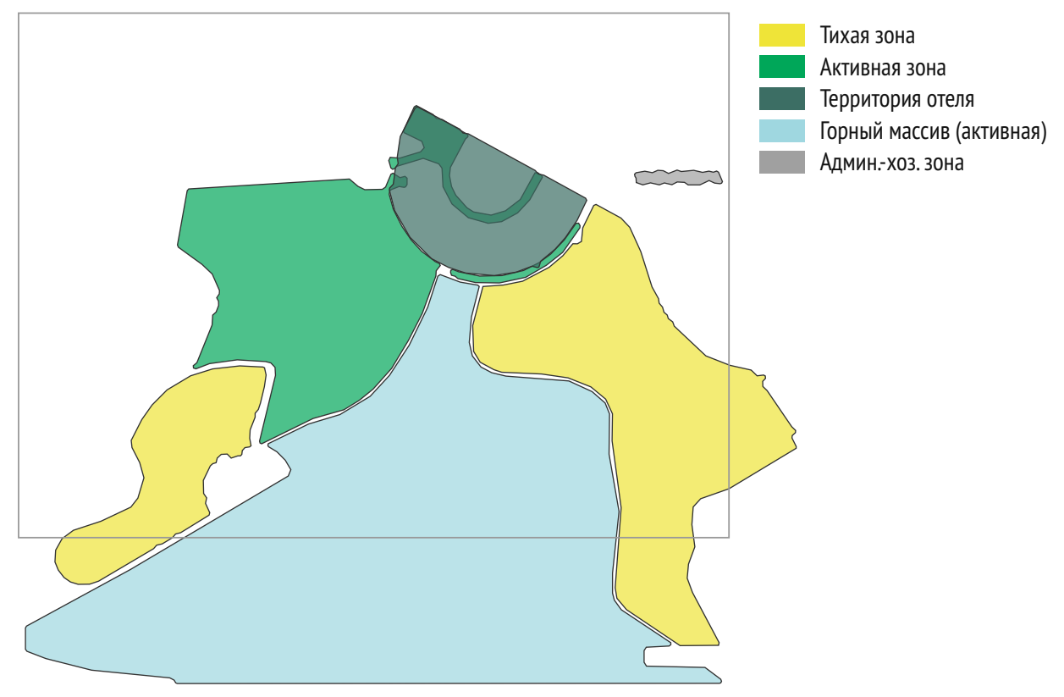
Тихая зона
Активная зона
Территория отеля
Горный массив (активная)
Админ.-хоз. зона

					Ала-Тоо Резорт · Жыргалан · деревня всесезонного курорта Предложение консорциума по развитию курортной среды
					на основе генплана «1903 13-6», концепции INPUT и «Жыргалан 2.0»
Изм.	Кол.	Лист	№док	Подп. Дата	
Разраб.		ИИ-ассист.		10.26	**Схема предложения** Зонирование, променад, путь гостя, М 1:1500
Рук. пр.		Аюпов Р.		10.26	
ГАП				10.26	**ГП-2**
Н. контр.				10.26	

Стадия	Лист	Листов
Конц.	**2**	**2**

М 1:1500