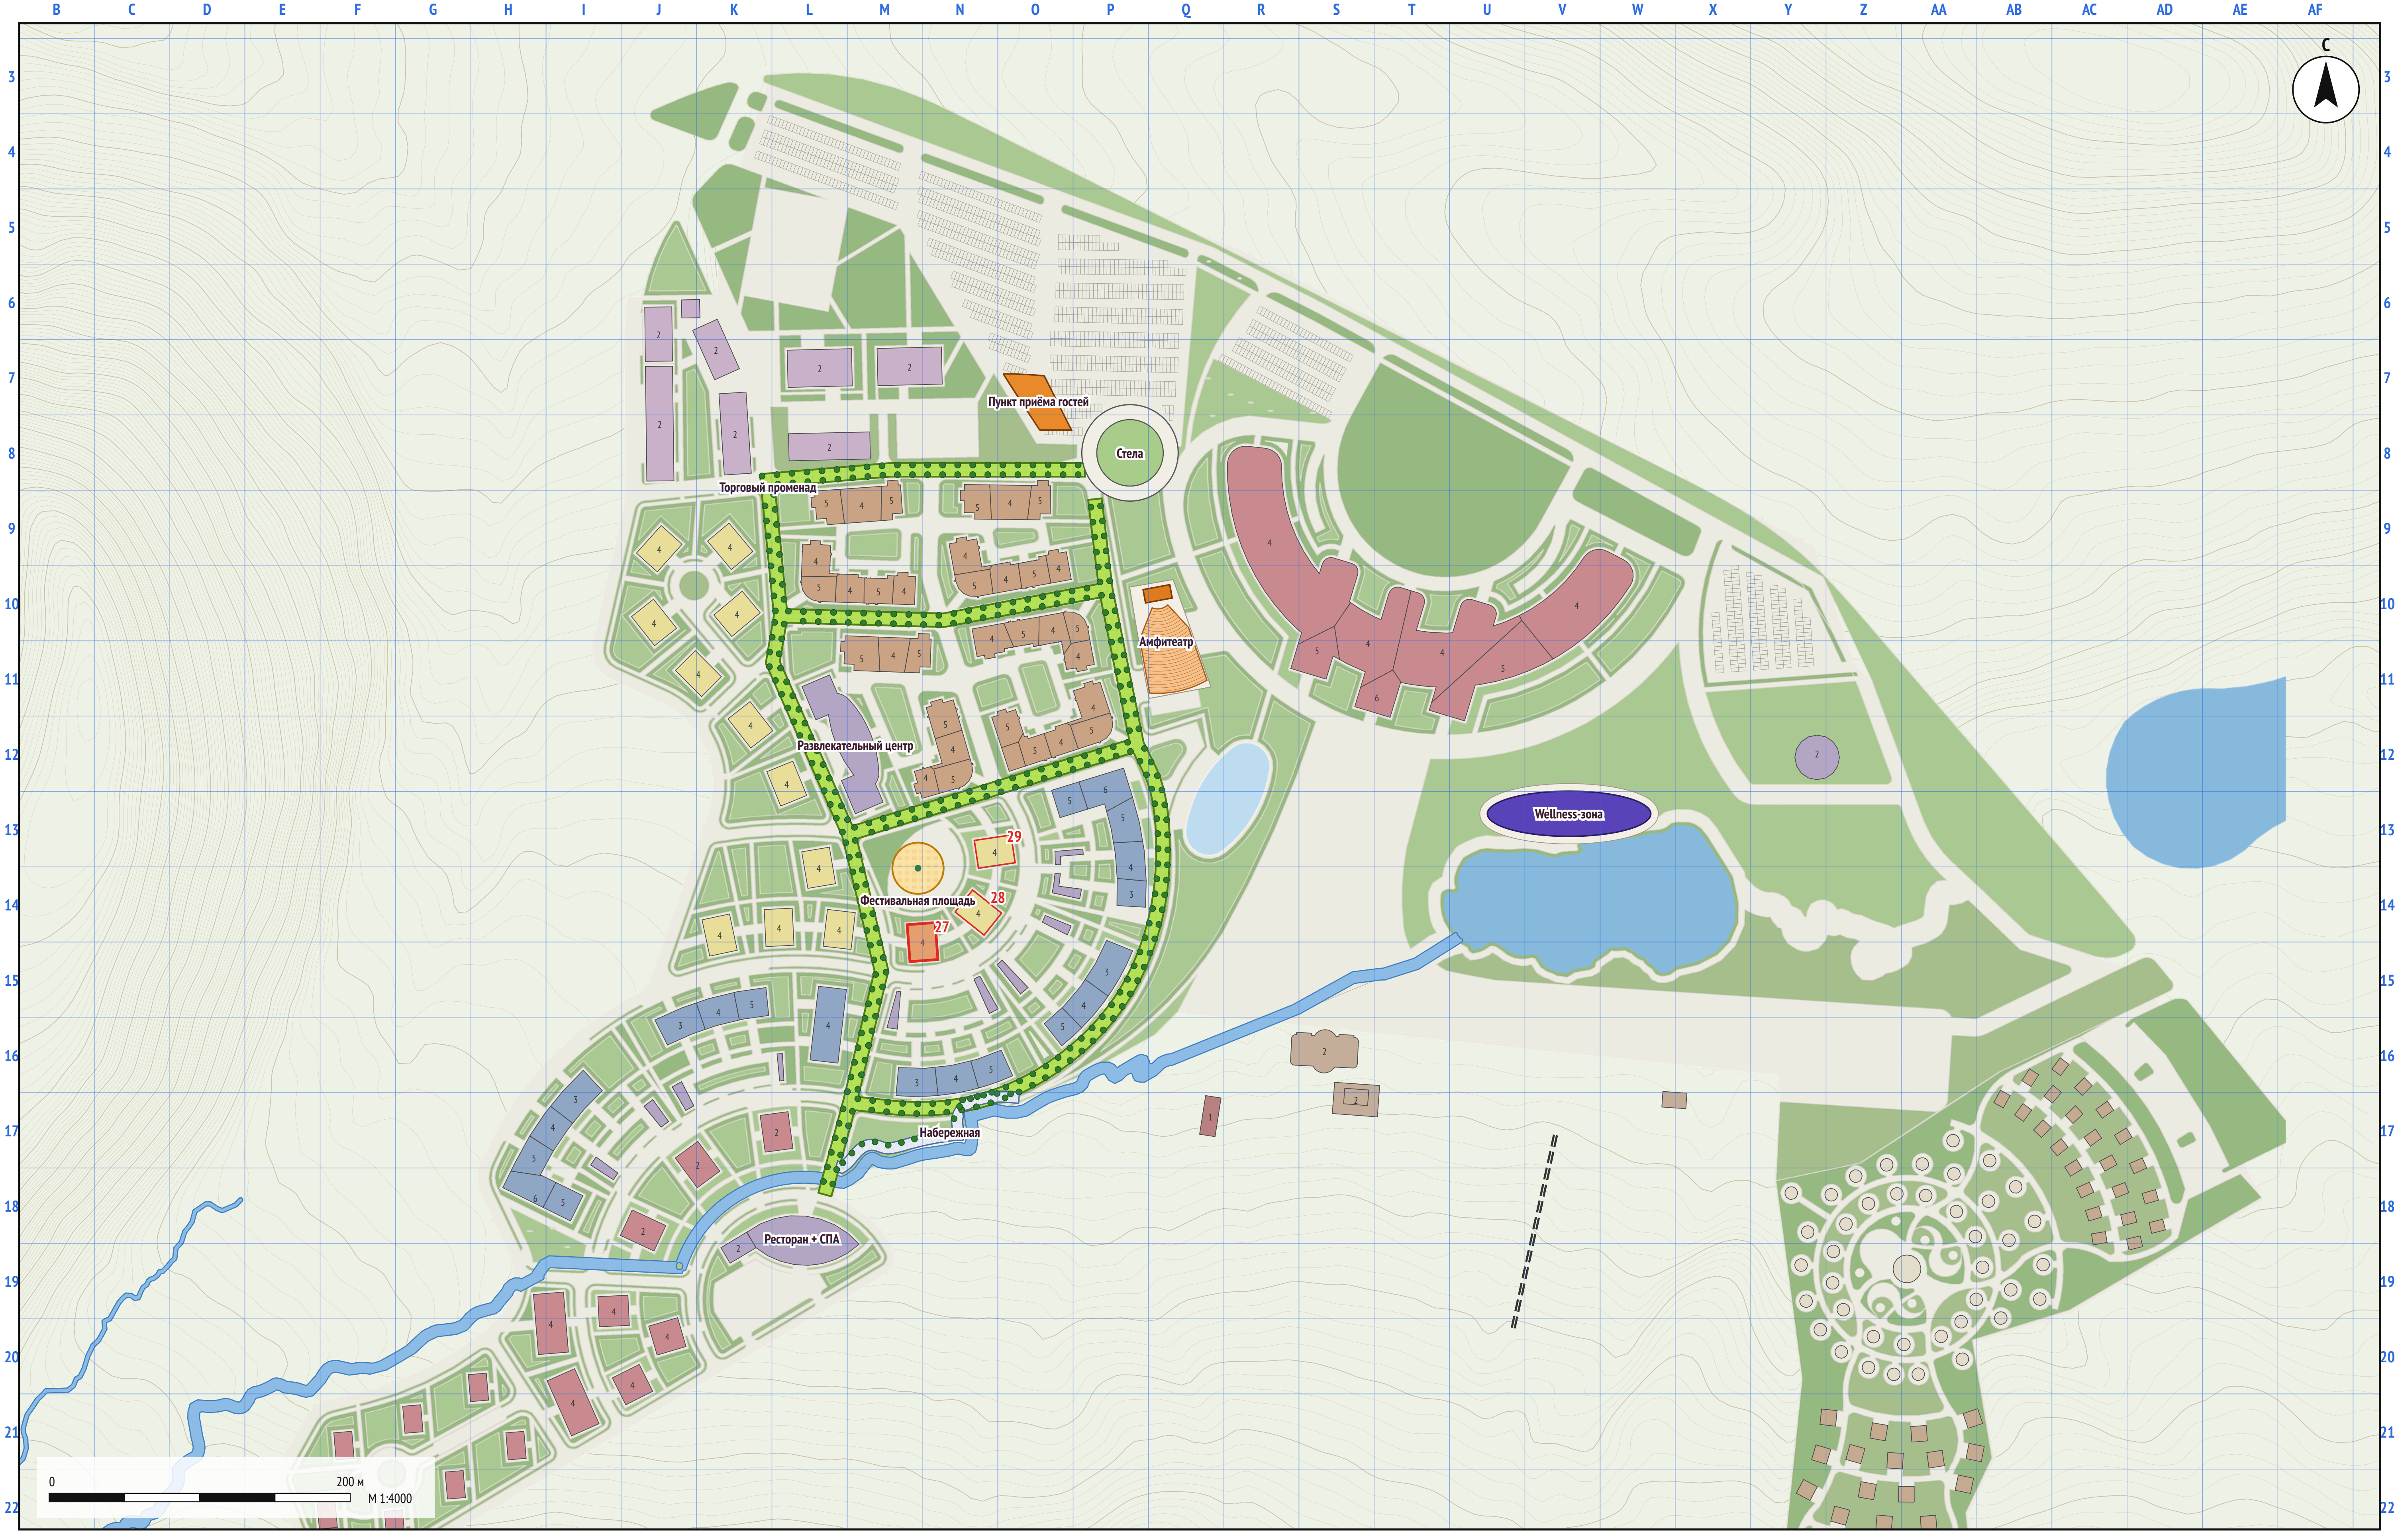

ГЕНПЛАН · ПРЕДЛОЖЕНИЕ КОНСОРЦИУМА · ВЕСЬ ПОСЁЛОК

На основе генплана Госстроя · М 1:4000 · формат А3

- 🟩 Торговый променад с деревьями
- 🟧 Пункт приёма гостей
- ▨ Набережная
- ⬜ Кольцо со стелой
- ▨ Фестивальная площадь
- 🟪 Wellness-зона
- 🟧 Амфитеатр со сценой
- 🟦 Река (по DWG)

- 🟥 Гостиницы 5*
- 🟪 Персонал, хозяйственные
- 🟦 Гостиницы 4*
- 🟫 Лыжная база, прокат
- 🟫 Гостиницы 3*
- 🟥 Станция подъёмника
- 🟨 Апартаменты, гостиницы 2*
- ⬜ Глэмпинг
- 🟪 Общественные здания

Основа – генплан Госстроя «1903 13-6» (DWG); предложение консорциума по разметке 20.10.2026; цифра в здании – этажность; сетка 50 м как на подложке ГП-0. Ала-Тоо Резорт · Жыргалан · ГП-1

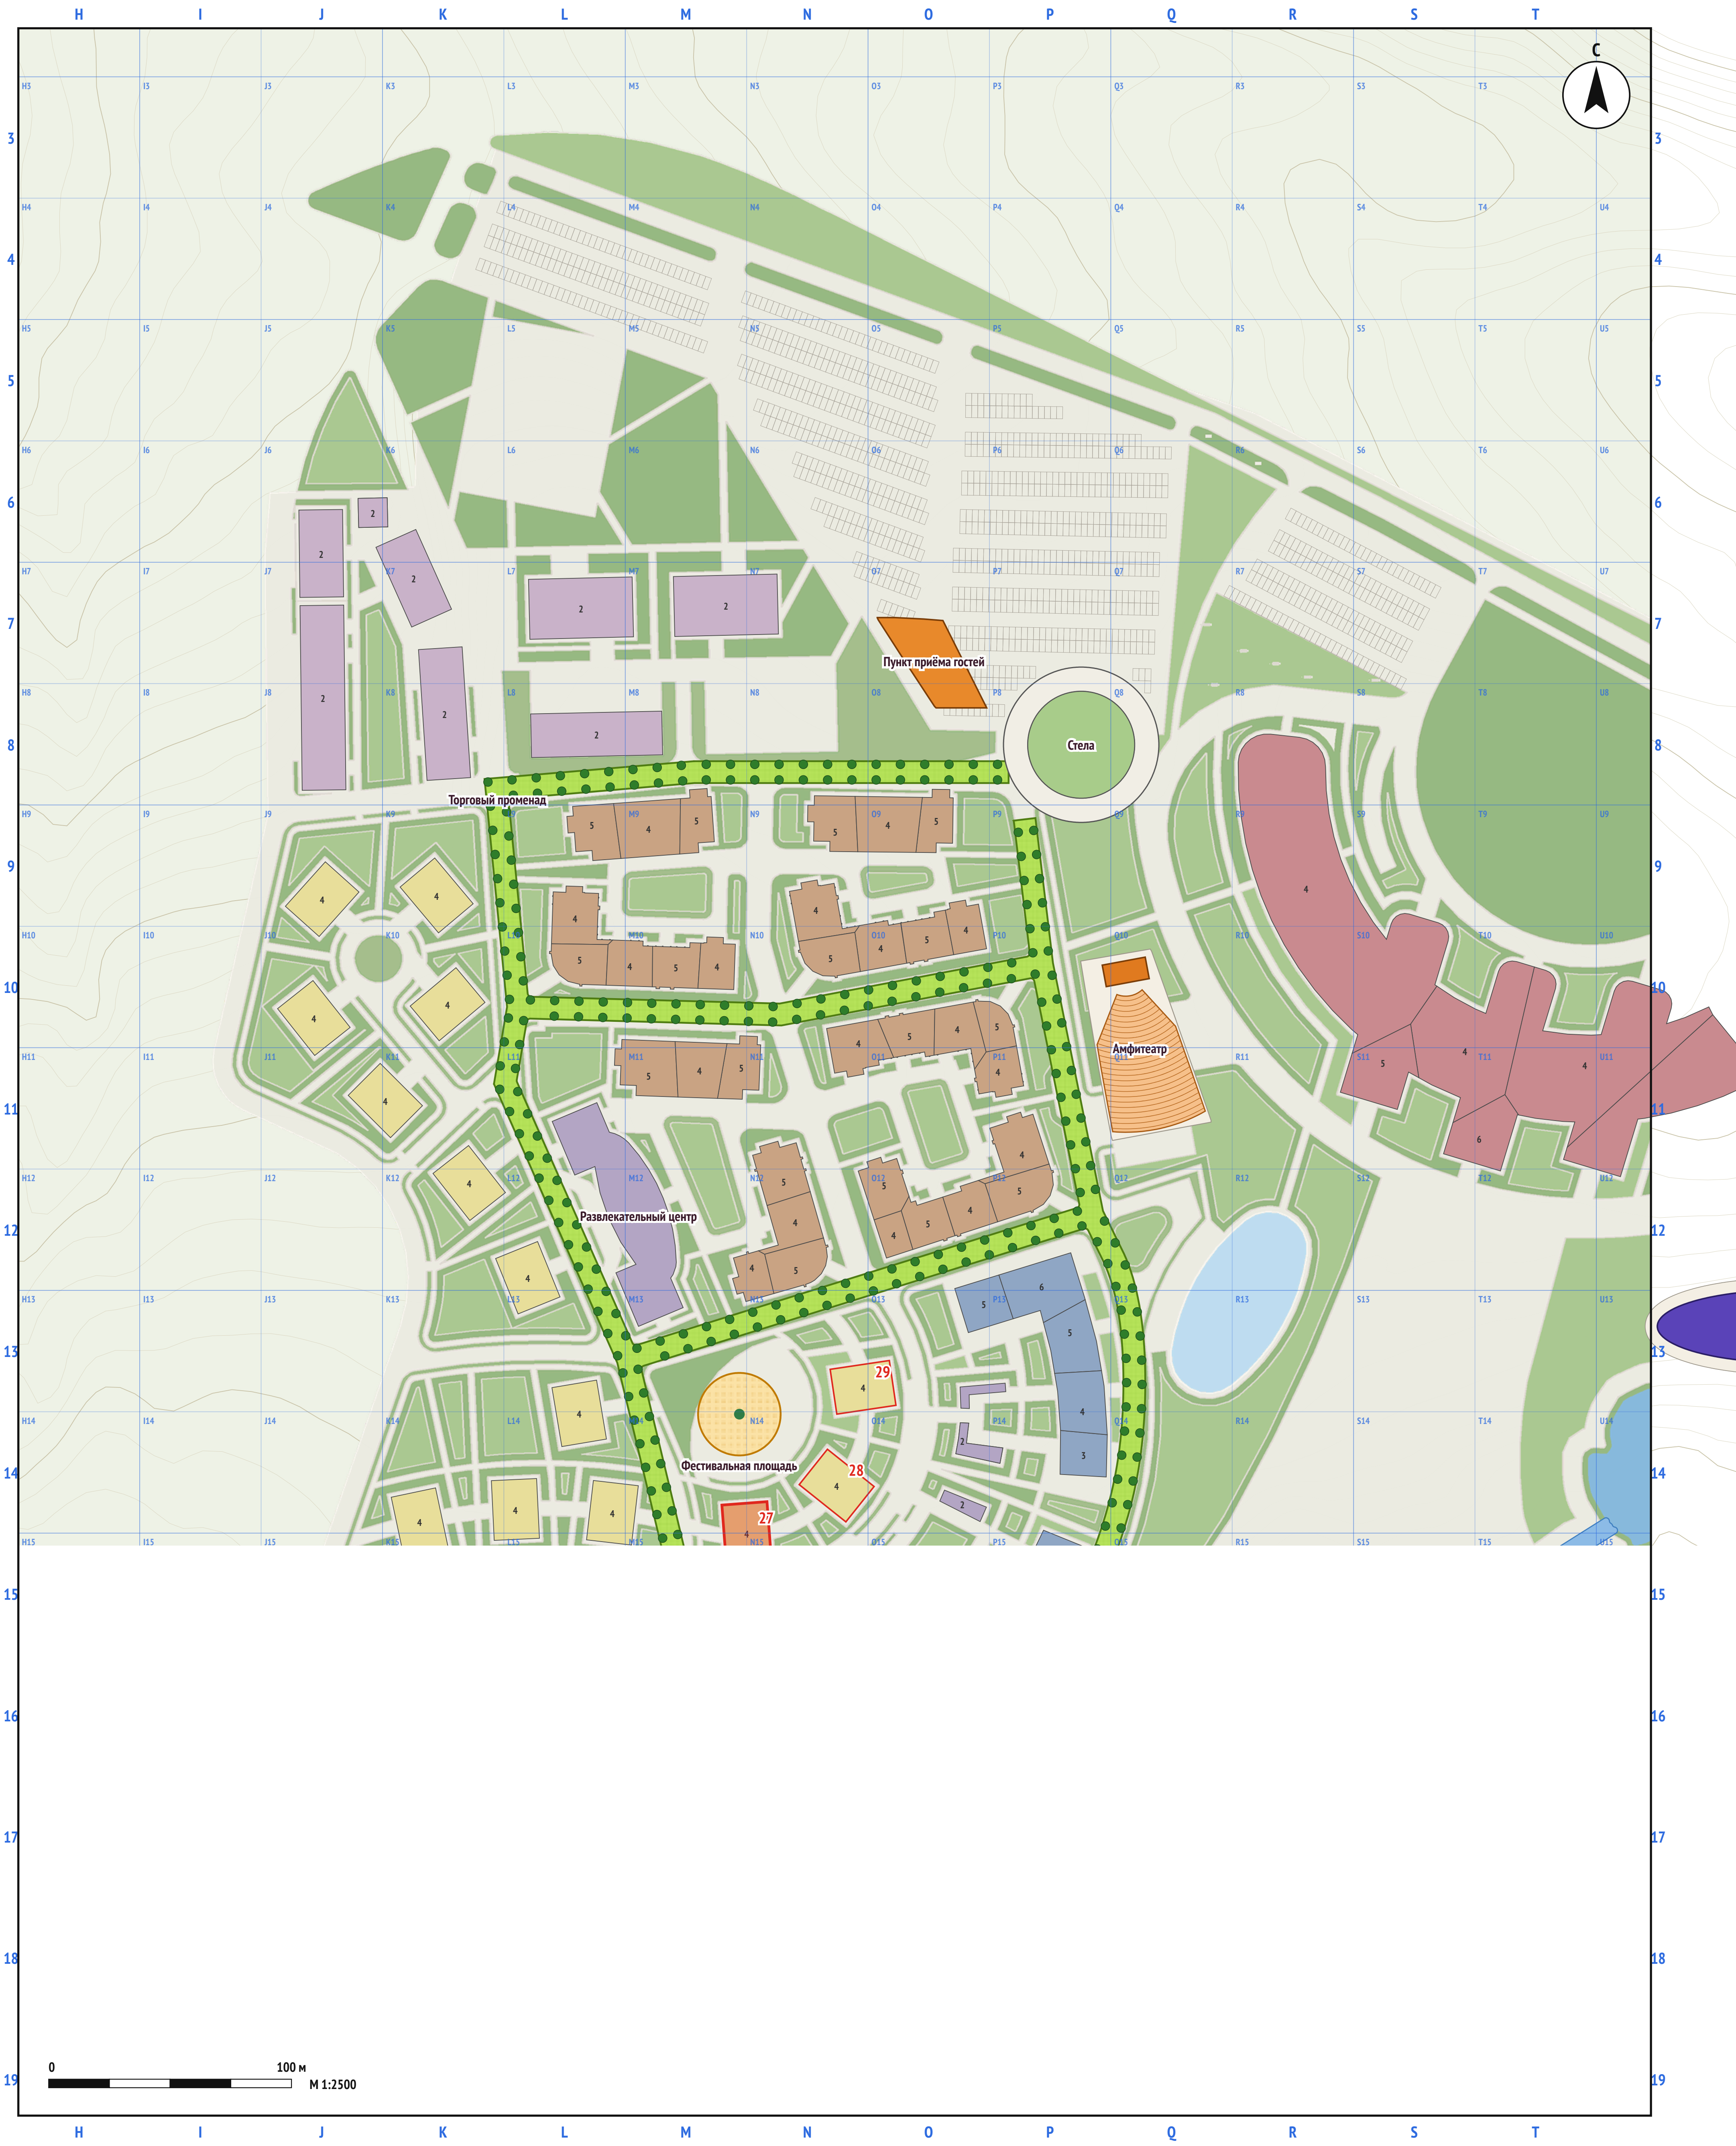

ГЕНПЛАН · ПРЕДЛОЖЕНИЕ · СЕВЕРО-ЗАПАДНАЯ ЗОНА

На основе генплана Госстроя · М 1:2500 · формат А3

- 🟩 Торговый променад с деревьями
- 🟧 Амфитеатр со сценой
- 🟪 Wellness-зона
- ⬜ Набережная
- 🟧 Пункт приёма гостей
- 🟦 Река (по DWG)
- 🟨 Фестивальная площадь
- ⬜ Кольцо со стелой

- 🟥 Гостиницы 5*
- 🟨 Апартаменты, гостиницы 2*
- 🟫 Лыжная база, прокат
- 🟦 Гостиницы 4*
- 🟪 Общественные здания
- 🟥 Станция подъёмника
- 🟫 Гостиницы 3*
- 🟪 Персонал, хозяйственные
- ⬜ Глэмпинг

Основа — генплан Госстроя «1903 13-6» (DWG); предложение консорциума по разметке 20.10.2026; цифра в здании — этажность; сетка 50 м как на подложке ГП-0. Ала-Тоо Резорт · Жыргалан · ГП-2

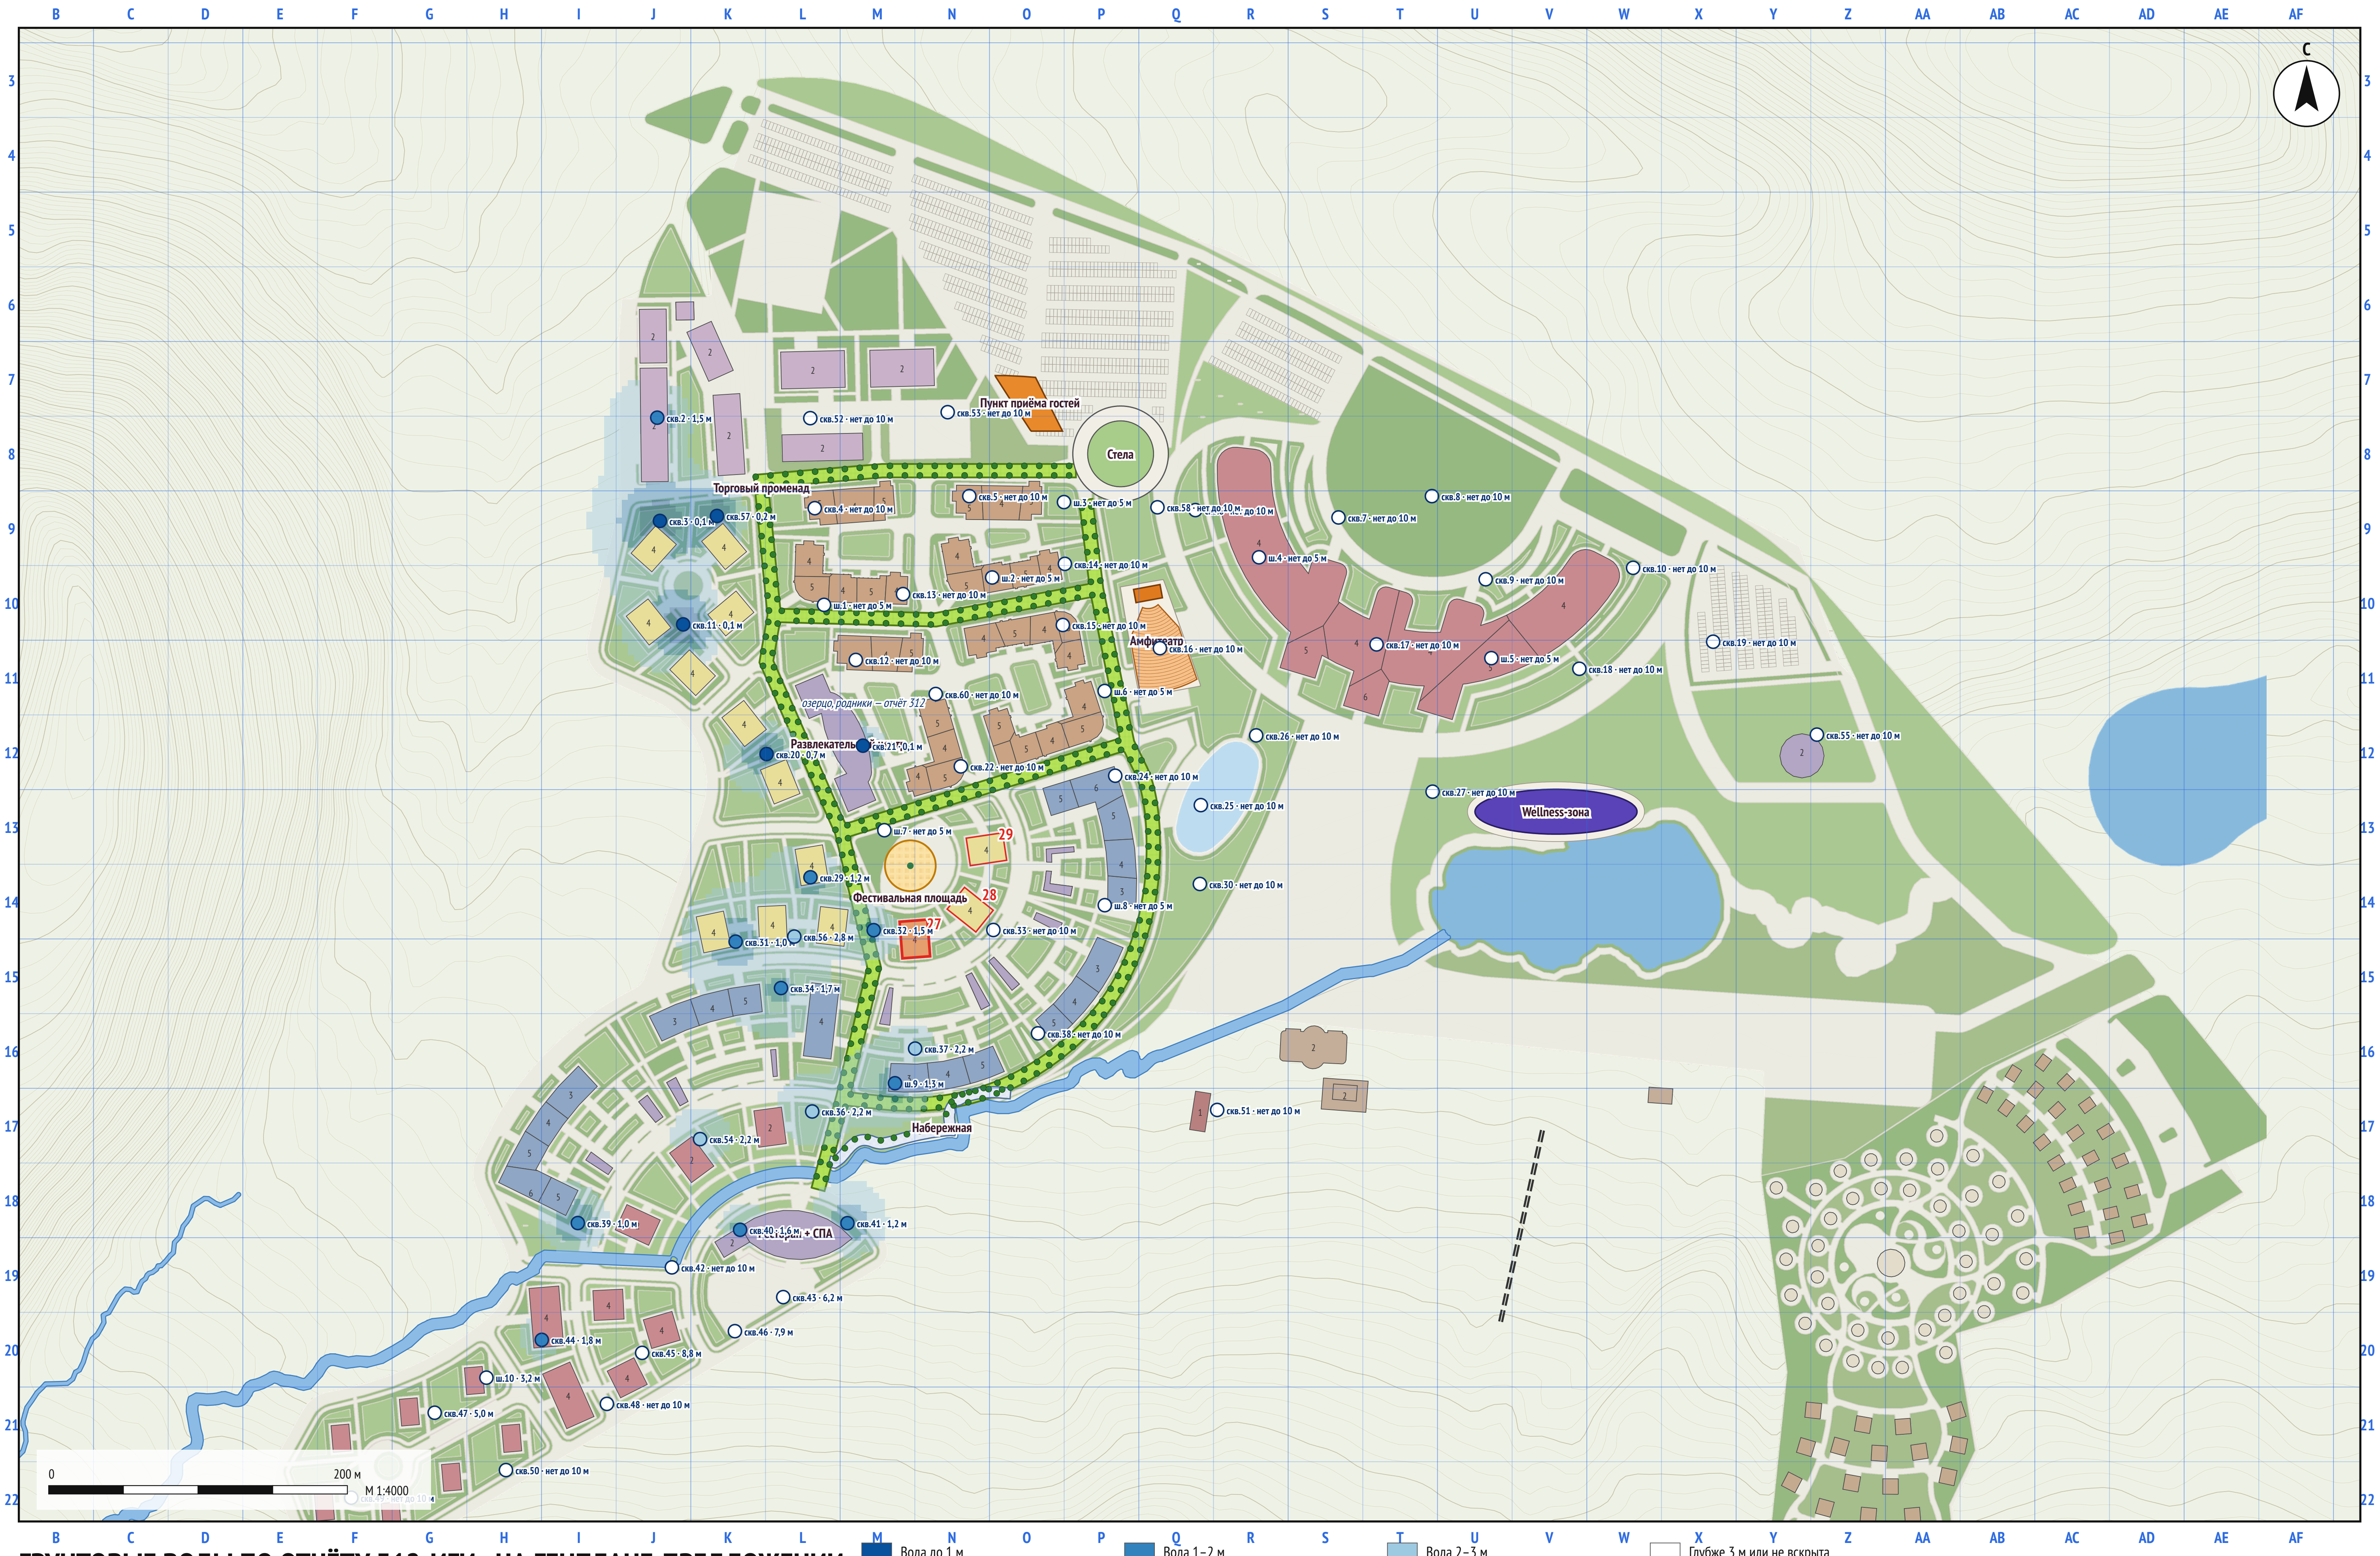

ГРУНТОВЫЕ ВОДЫ ПО ОТЧЁТУ 312-ИГИ · НА ГЕНПЛАНЕ-ПРЕДЛОЖЕНИИ

Глубина появления воды от поверхности, сентябрь 2024 · М 1:4000 · формат А3

- 🟦 Вода до 1 м
- 🟦 Вода 1–2 м
- 🟦 Вода 2–3 м
- ☐ Глубже 3 м или не вскрыта
- 🟩 Торговый променад
- ▨ Набережная
- 🟧 Амфитеатр
- 🟪 Wellness-зона

- 🟥 Гостиницы 5*
- ▨ Персонал, хозяйственные
- 🟦 Гостиницы 4*
- ▨ Лыжная база, прокат
- 🟫 Гостиницы 3*
- 🟥 Станция подъёмника
- 🟨 Апартаменты, гостиницы 2*
- ☐ Глэмпинг
- 🟪 Общественные здания

Уровни — появившиеся при бурении 23–25.09.2024 (межень), отчёт 312-ИГИ «Изыскатель»; в июне выше до 1,5 м. Между скважинами — интерполяция, не замер. Скв.23, 28, 35, 59 не нанесены: ошибка Y в каталоге. ГП-3