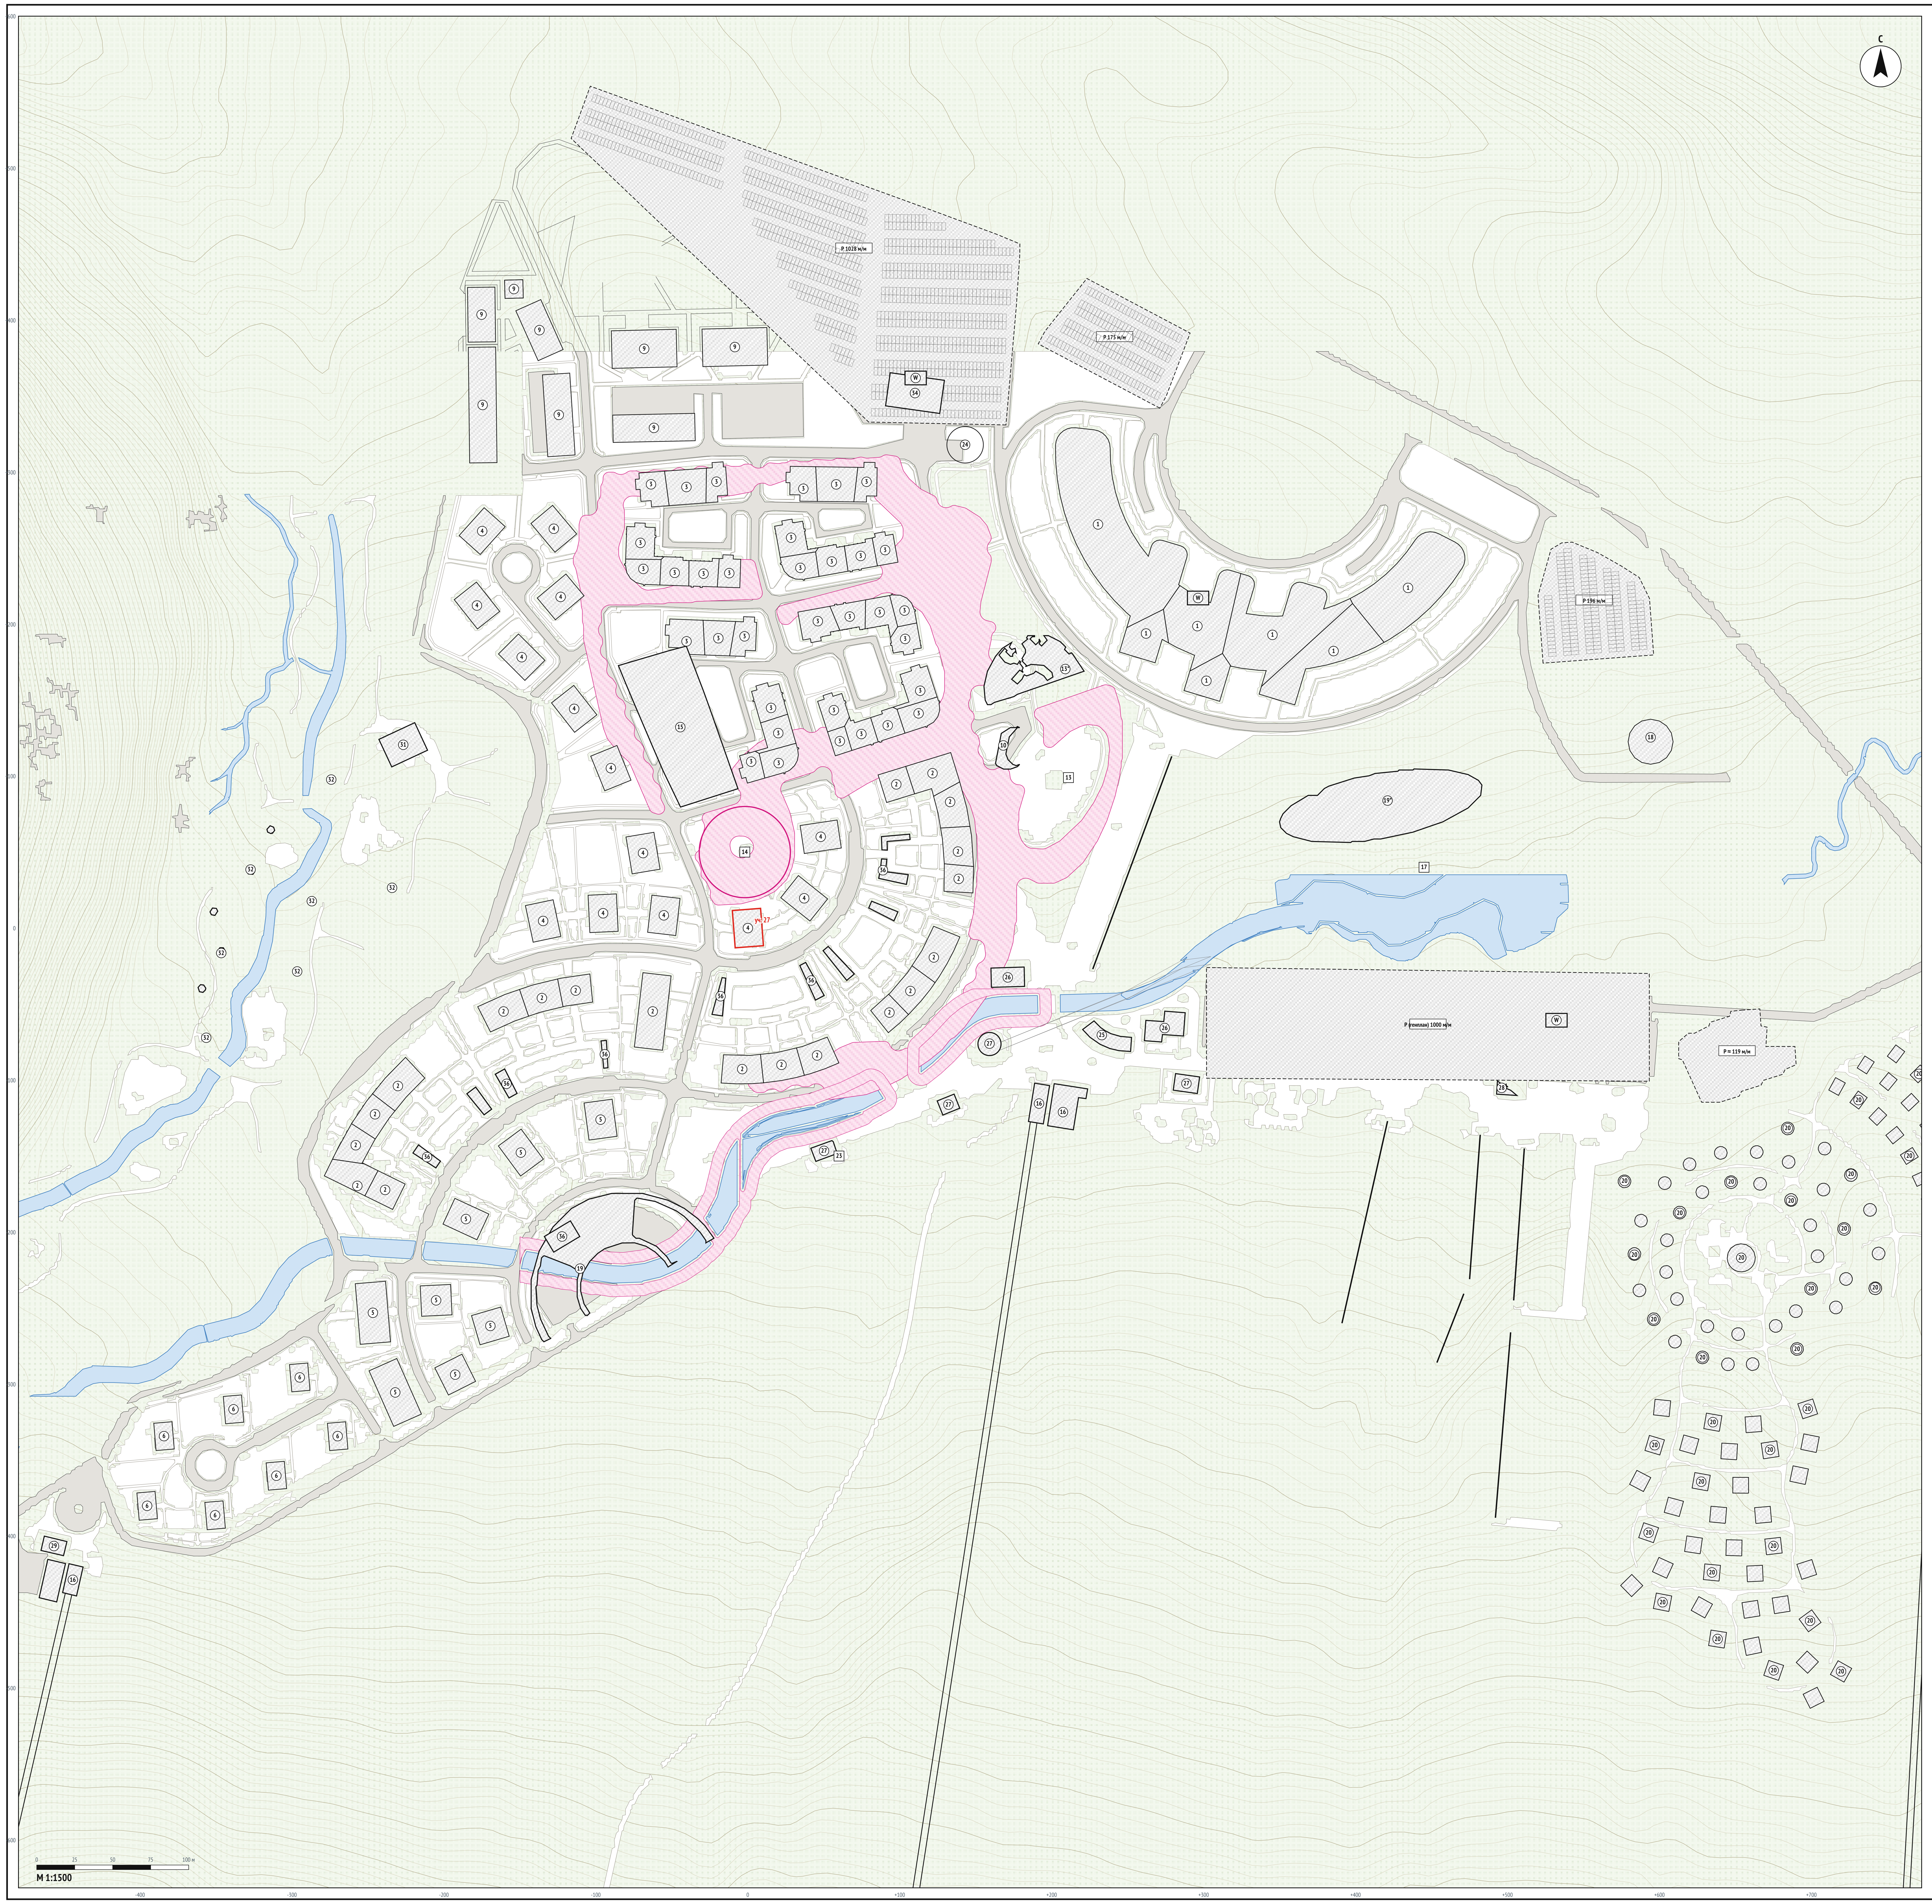

# ГЕНЕРАЛЬНЫЙ ПЛАН ДЕРЕВНИ · ПРЕДЛОЖЕНИЕ

Чертёж по ГОСТ 21.508, стадия концепции, М 1:1500

## Экспликация зданий и сооружений

| № | Наименование | Этажн. | Кол-во | Пл. застр., м² | Источник |
|---|---|---|---|---|---|
| 1 | Основная гостиница 5* | 4–6 | 7 | 15 661 | генплан |
| 2 | Гостиницы 4* | 3–6 | 20 | 9 712 | генплан |
| 3 | Гостиницы 3* | 4–5 | 34 | 12 575 | генплан |
| 4 | Апартаменты. Гостиницы 2* | 4 | 14 | 6 425 | генплан |
| 5 | Гостиницы 5* | 2–4 | 8 | 4 177 | генплан |
| 6 | VIP-коттеджи | 2 | 7 | 1 513 | генплан |
| 9 | Здания для персонала, хозяйственные | 2 | 9 | 7 008 | генплан |
| 10 | Прокат, продажа и ремонт снаряжения | 1 | 1 | 190 | предложение |
| 11 | Административные и общественные здания | 2 | 1 | 236 | генплан |
| 13* | Концертная площадка | 1 | 1 | 1 417 | предложение |
| 15 | КДЦ: кинотеатр, технопарк, зал | 1 | 1 | 4 414 | предложение |
| 16 | Нижние станции и гаражи канатных дорог B1, F | 1 | 4 | 1 260 | INPUT |
| 18 | Мечеть | 2 | 1 | 672 | генплан |
| 19 | Велнес-зона с рестораном | 1 | 1 | 2 662 | предложение |
| 19* | Велнес у озера | 1 | 1 | 4 466 | предложение |
| 20 | Юрточный городок, глэмпинг | 1 | 100 | 7 856 | генплан |
| 24 | Стела «Жыргалан» на въездном кольце | 1 | 1 | 4 | предложение |
| 25 | Центр приветствия B1: кассы, школа, администрация | 1 | 1 | 299 | INPUT |
| 26 | Магазин, аренда и депо снаряжения | 1 | 2 | 644 | INPUT |
| 27 | Бистро, апрес-ски | 1 | 4 | 617 | INPUT |
| 28 | Детская зона, центр приветствия | 1 | 1 | 60 | INPUT |
| 29 | Центр приёма гостей F | 1 | 1 | 147 | INPUT |
| 30 | Главный технический центр, гаражи ратраков | 1 | 1 | 694 | INPUT |
| 31 | Ресторан «Оазис» | 1 | 1 | 520 | INPUT |
| 32 | Беседки «Оазис» для пикников | 1 | 10 | 182 | INPUT |
| 34 | Пункт прибытия: заселение, лаунж, багаж, душевые, прокат, кафе | 2 | 1 | 792 | путь гостя |
| 36 | Павильоны променада: кофейня, стритфуд, сервис, ремёсла | 1 | 16 | 1 996 | предложение |
| W | Welcome-павильоны | 1 | 4 | 504 | предложение |
| 12 | Гостевые автостоянки (число мест — на плане) | | | | генплан |
| 13 | Открытый каток | | | | генплан |
| 14 | Событийная площадь с ёлкой (бывшая концертная №14) | | | | предложение |
| 17 | Искусственный пруд, озеро | | | | генплан |
| 23 | Благоустроенная набережная | | | | предложение |
| 35 | Лыжехранилище у станции B1 (в составе 25) | | | | предложение |

## Технико-экономические показатели

| | |
|---|---|
| Курортный посёлок (зона) | **24.3 га** |
| Территория отеля 5* | **7.0 га** |
| Парк-отель | **15.9 га** |
| Административно-хозяйственная зона | **3.7 га** |
| Площадь застройки (все здания на плане) | **86 703 м²** |
| Торговый променад / квартал | **3.56 га** |
| Благоустроенная набережная | **≈ 351 м по каналу** |
| Гостевые автостоянки, всего | **≈ 2 630 м/м** |
| Пешком от Пункта прибытия до площади 14 / уч. 27 / B1 | **410 / 447 / 544 м** |
| Ось деревни (стела ⟶ площадь ⟶ B1) | **шаттл, доставка, экстренные службы** |

## Условные обозначения

| | |
|---|---|
| ▨ | Проектируемые здания; в кружке — номер по экспликации, этажность — в таблице |
| 🟪 | Торговый променад / квартал, набережная (предложение) |
| ▩ | Проезды; ось деревни — только шаттл, доставка, экстренные службы |
| ☐ | Тротуары, площади, участки |
| ⬚ | Гостевые автостоянки с числом мест |
| 🟩 | Озеленение, луг; горизонтали через 1 м |
| 🟦 | Канал, пруды, озеро |

1. Основа — генплан Госстроя «1903 13-6» (DWG), концепция INPUT (сентябрь 2025) и «Жыргалан 2.0» (апрель 2026).
2. Ресторан-«линза» генплана заменён велнес-зоной 19 с рестораном; здание №19 (ресторан, фитнес, спа) — КДЦ 15.
3. Лыжная база и станция генплана заменены базой B1 по INPUT (25–28, 16).
4. Парковки 1 030, 175 и 200 м/м — по разметке DWG; новые у глэмпинга — оценка по площади (25 м² на место).
5. Координаты сетки — локальные, м: 0;0 — центр уч. 27; E = x + 332 968,5; N = y + 4 720 510,3 (UTM 44N).

| | | | | | | |
|---|---|---|---|---|---|---|
| | | | | | **Ала-Тоо Резорт · Жыргалан · деревня всесезонного курорта**<br>Предложение консорциума по развитию курортной среды | |
| | | | | | на основе генплана «1903 13-6», концепции INPUT и «Жыргалан 2.0» | |
| Изм. | Кол. | Лист | №док | Подп. Дата | | Стадия / Лист / Листов |
| Разраб. | | ИИ-ассист. | | 10.26 | **Генеральный план. Предложение**<br>Чертёж, экспликация, ТЭП, М 1:1500 | **Конц.** / **1** / **2** |
| Рук. пр. | | Аюпов Р. | | 10.26 | | |
| ГАП | | | | 10.26 | **ГП-1** | **М 1:1500** |
| Н. контр. | | | | 10.26 | | |

# СХЕМА ПРЕДЛОЖЕНИЯ · ДЕРЕВНЯ ЖЫРГАЛАН

Зонирование, променад, магистрали, путь гостя · М 1:1500

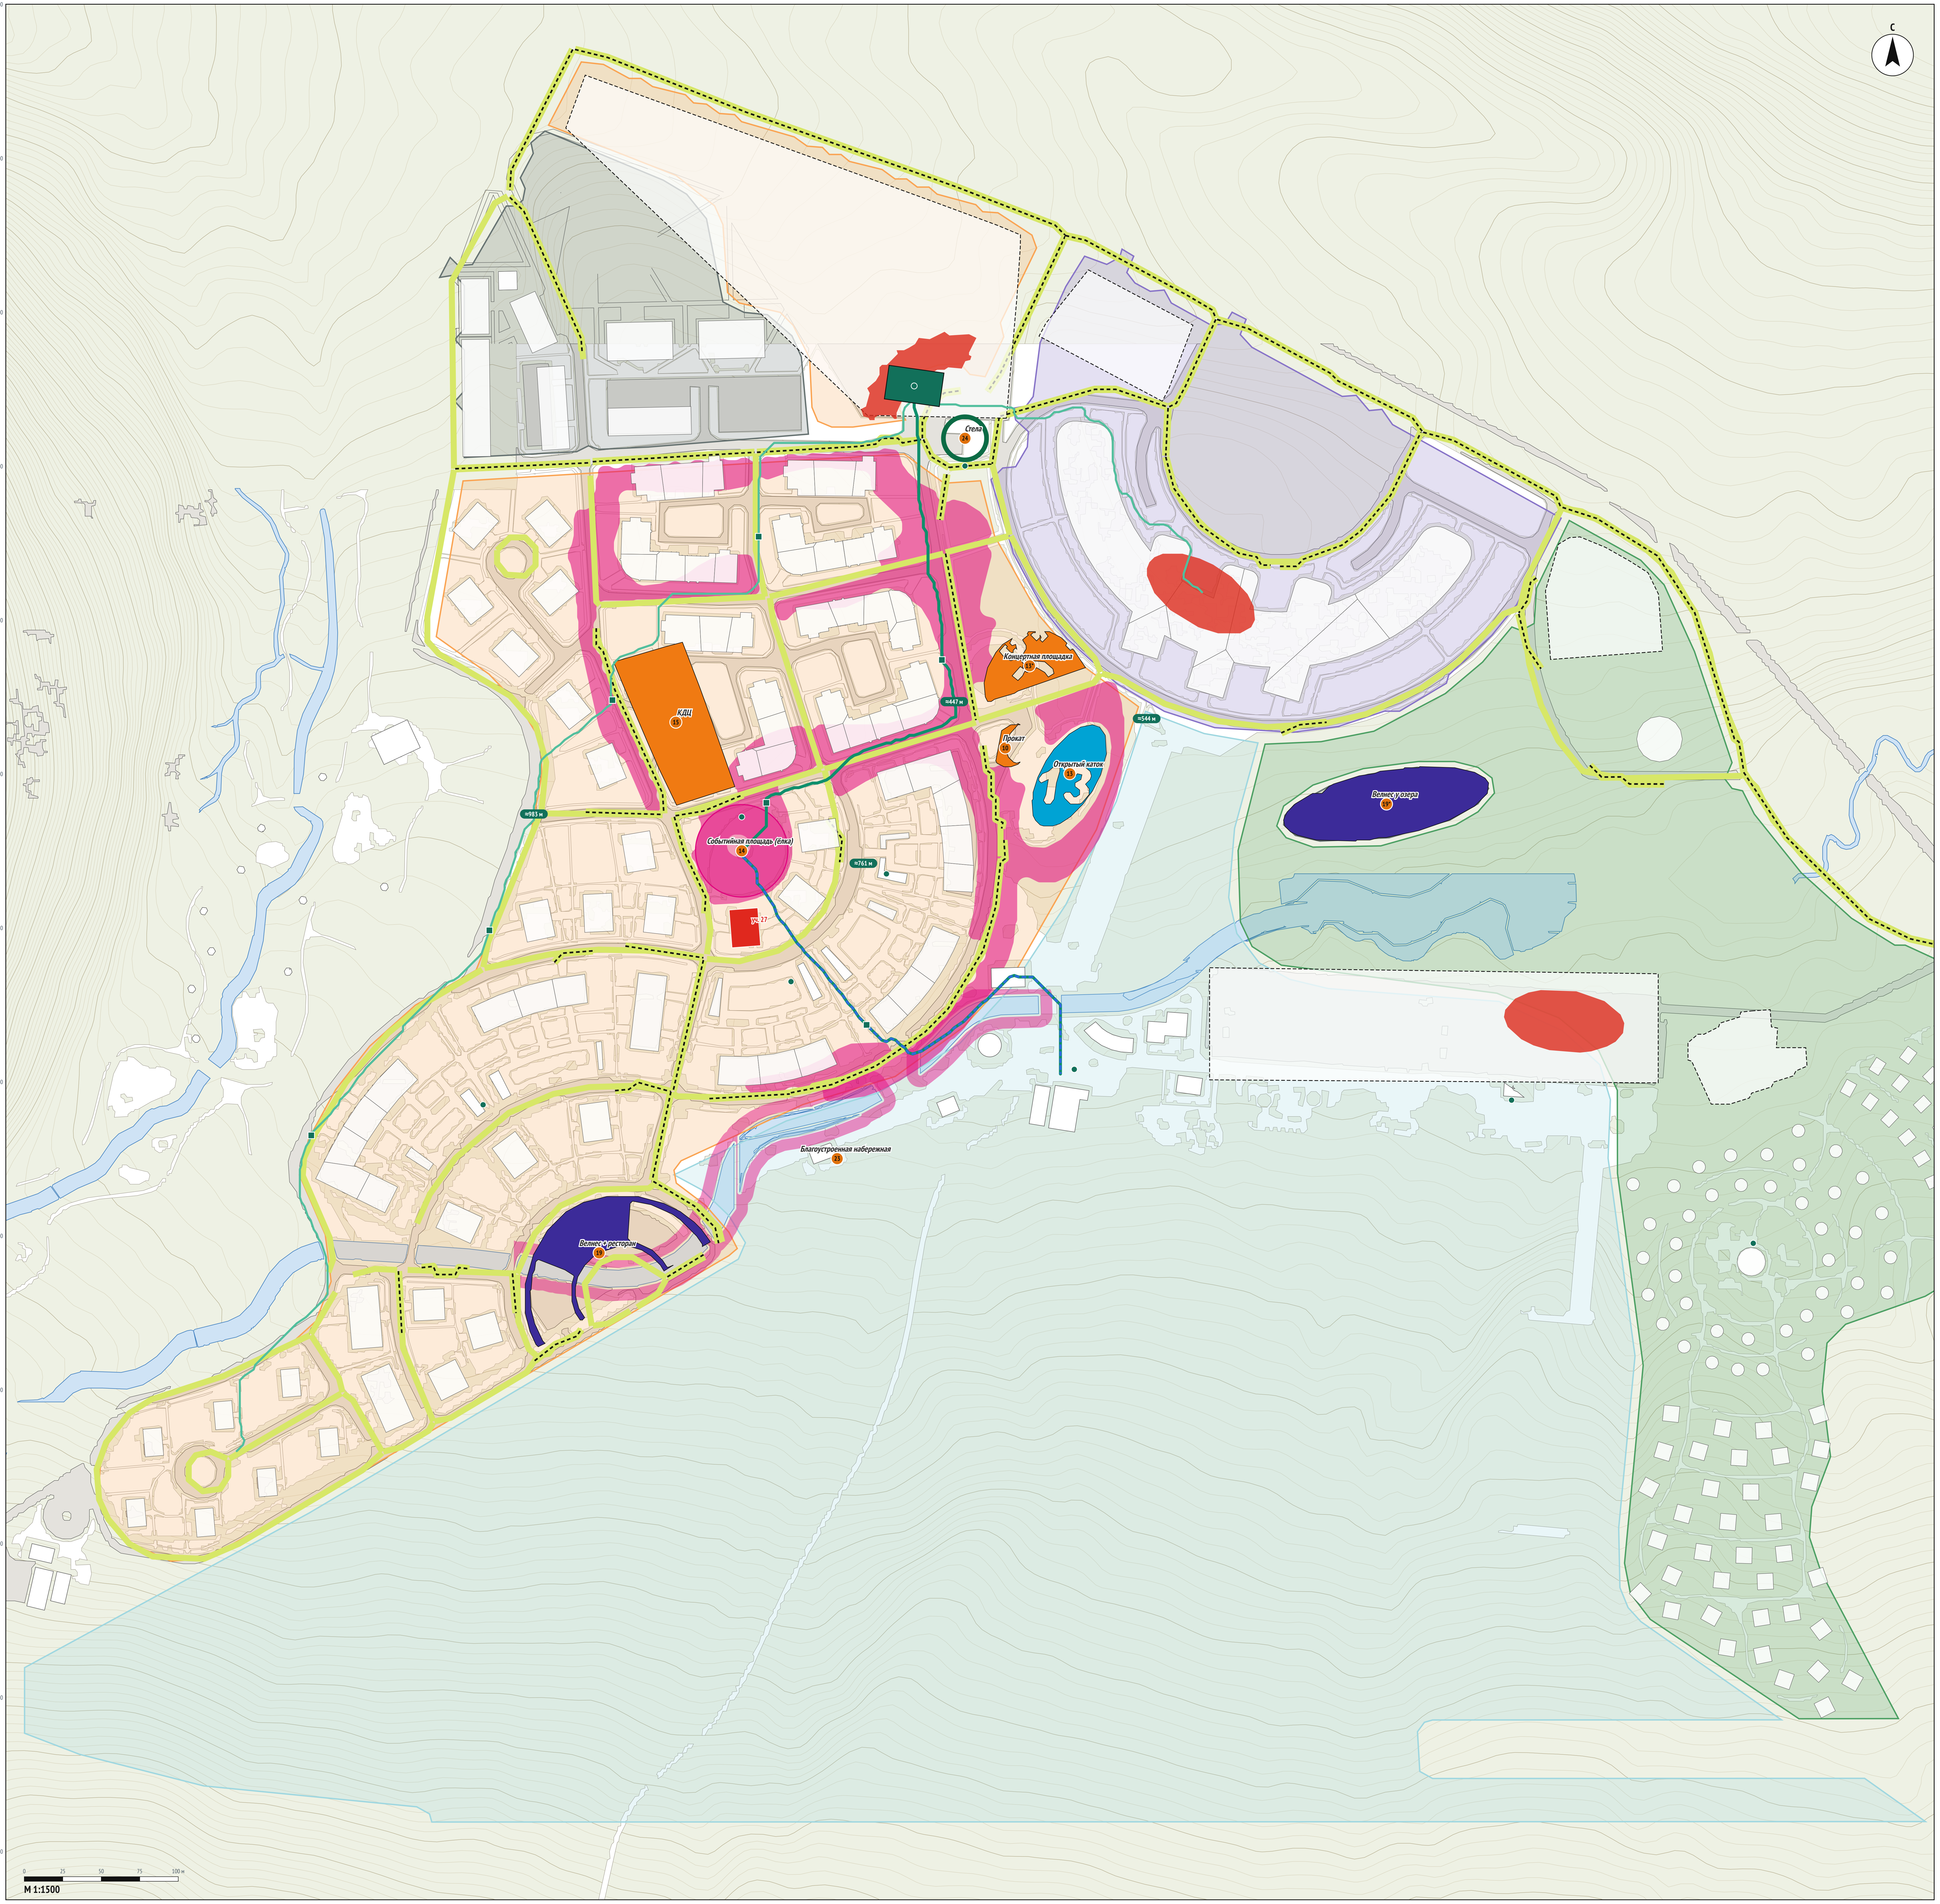

**Функциональное зонирование**

- 🟧 Курортный посёлок
- 🟪 Отель 5*
- 🟩 Парк-отель
- ▭ Горный массив
- ▨ Административно-хозяйственная зона

**Структура «Жыргалан 2.0»**

- 🟪 Торговый променад / квартал, набережная 23
- 🟨 Транспортные магистрали; с пунктиром — основные
- 🟥 Welcome-зоны
- 🟧 КДЦ 15, концертная площадка 13*, прокат 10
- 🟦 Велнес 19 (с рестораном) и 19*
- 🟦 Открытый каток 13
- 🟩 Стела 24 на въездном кольце

**Путь гостя (консорциум)**

- 🟩 Пункт прибытия у стелы: заселение, лаунж, багаж, прокат
- — Шаттл по оси: стела ⟶ площадь 14 ⟶ набережная ⟶ В1
- — Электрокары: к велнесу 19 и виллам, к «полумесяцу»
- — Лыжная улица: площадь 14 ⟶ В1
- 🟩 Тёплые остановки (квадрат), сервисы (точка)

## Объекты предложения

| | |
|---|---|
| 24 | Стела на въездном кольце, ориентир и точка высадки |
| 14 | Событийная площадь (ёлка) — бывшая концертная площадь №14 |
| 15 | КДЦ: кинотеатр, технопарк, зал |
| 13* | Концертная площадка |
| 13 | Открытый каток |
| 10 | Прокат, продажа и ремонт снаряжения |
| 19 | Велнес-зона с рестораном |
| 19* | Велнес у озера |
| 23 | Благоустроенная набережная |
| 12 | Гостевые автостоянки |
| W | Welcome-зоны: у стелы, у «полумесяца», у озера, на восточном въезде |
| – | Торговый променад / квартал (розовый); ось деревни — только шаттл, доставка, экстренные службы |

## Путь гостя: 10 точек

1. Дорога: сообщения за 48 и за 3 часа, трансфер из Бишкека и Алматы, предзаказ ски-пасса и проката
2. Въезд: стела и кольцо 24 — первая точка, указатели «Прибытие» / «Дневные лыжники — к базе В1» / «Служебный въезд»
3. Парковка: северная стоянка, высадка на кольце, багаж принимает служба и везёт в номер
4. Пункт прибытия: заселение у стойки или терминала, ключ в телефон, лаунж и душ, если номер не готов
5. Пока номер не готов: прокат и катание, обед, прогулка по променаду, каток, спа
6. Первое утро: шаттл к базе В1 каждые 10–15 минут, прокат по предзаказу, «3 урока» для новичков
7. К подъёмнику: лыжная улица от площади 14, тёплые остановки каждые ~180 м, лыжехранилище у станции
8. Некатающимся: детский клуб, велнес 19 и 19*, юрта с национальной кухней, КДЦ
9. Вечер: торговый променад, событийная площадь с ёлкой, концерты на 13*, рестораны
10. Выезд: лаунж и душ после катания, багаж к машине на кольце высадки

## Шумовые зоны (слайд 6 «Жыргалан 2.0»)

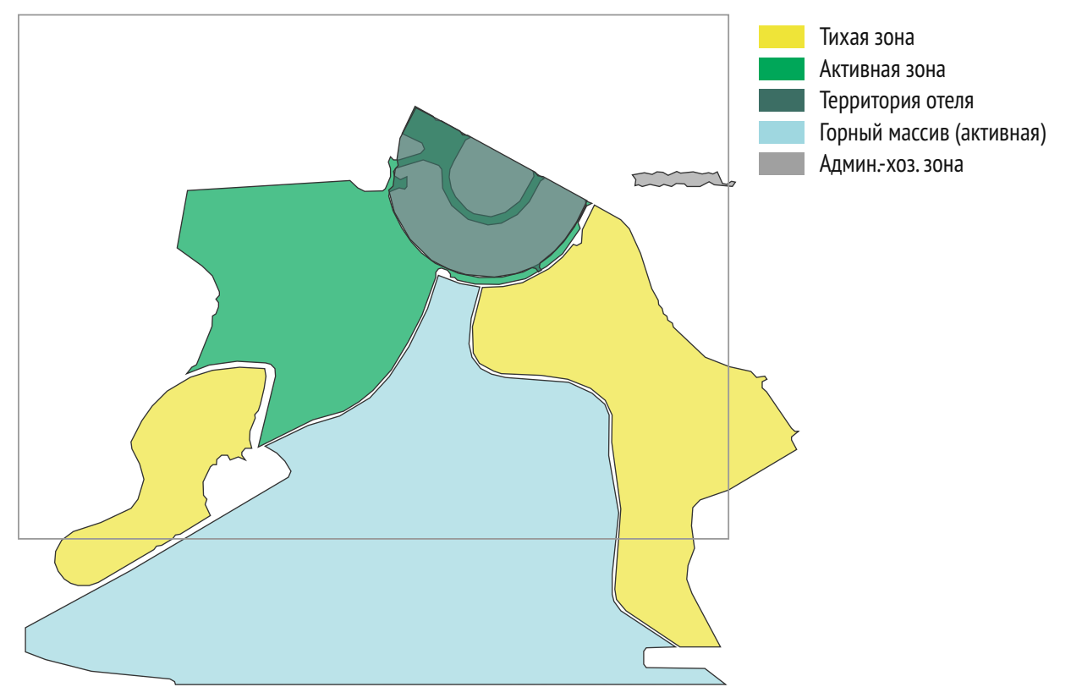

| Изм. | Кол. | Лист | №док | Подп. Дата |
|---|---|---|---|---|
| Разраб. | | ИИ-ассист. | | 10.26 |
| Рук. пр. | | Аюпов Р. | | 10.26 |
| ГАП | | | | 10.26 |
| Н. контр. | | | | 10.26 |

**Ала-Тоо Резорт · Жыргалан · деревня всесезонного курорта**

Предложение консорциума по развитию курортной среды

на основе генплана «1903 13-6», концепции INPUT и «Жыргалан 2.0»

**Схема предложения**

Зонирование, променад, путь гостя, М 1:1500

| Стадия | Лист | Листов |
|---|---|---|
| **Конц.** | **2** | **2** |

**ГП-2**

**М 1:1500**